
MASTERPLAN KAWASAN PETERNAKAN AYAM KUB SEMI UMBARAN

skala 1 : 500 · lahan 100 x 400 m = 4 ha · bentuk sungai mengikuti sketsa pemilik, ukur ulang sebelum pematokan

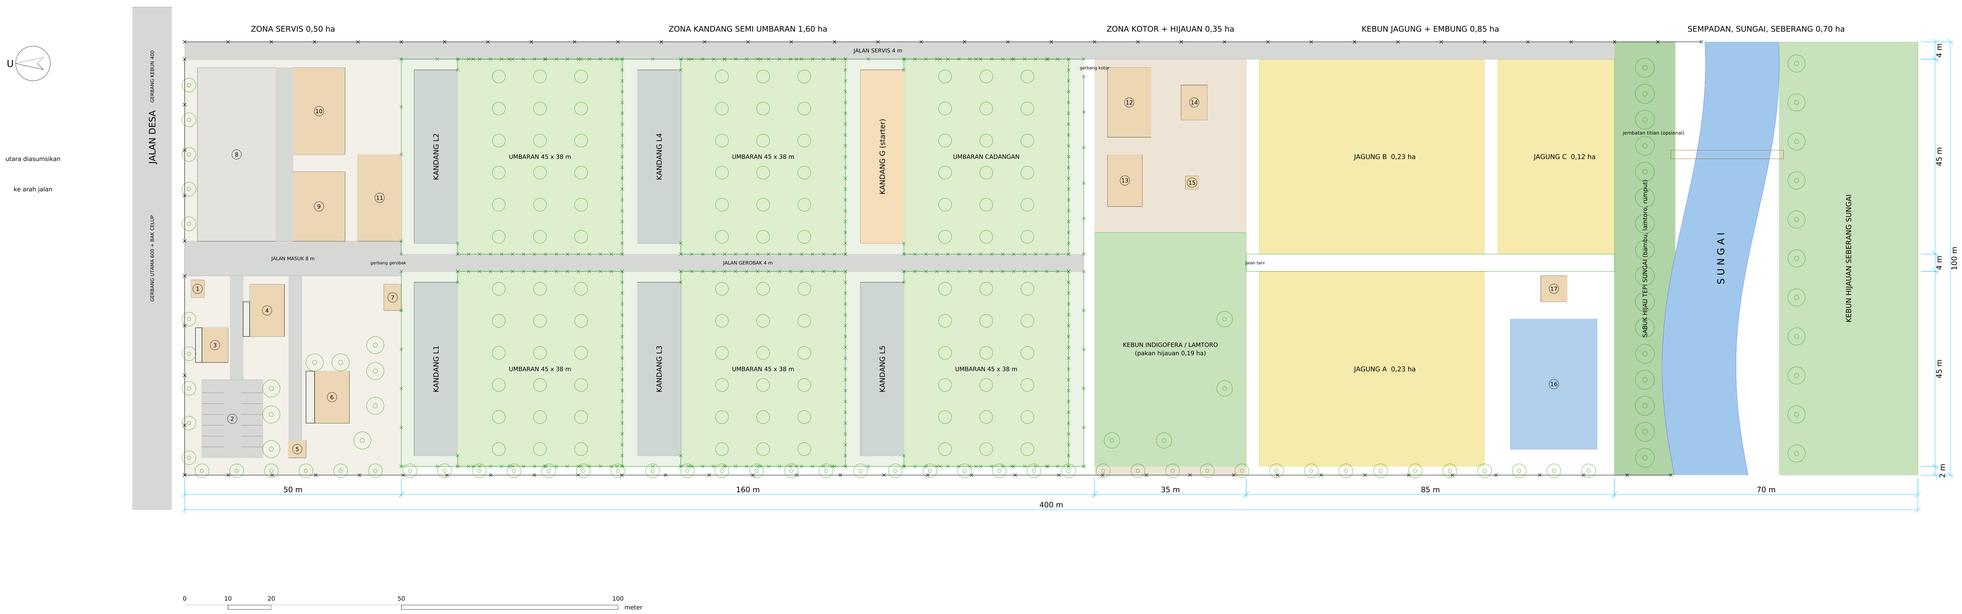

KETERANGAN BANGUNAN

		UKURAN	GAMBAR
1	Pos jaga	4 x 3 m	B-01
2	Parkir tamu & pembeli	18 x 14 m	MP-02
3	Kantor	8 x 6 m	B-02
4	Rumah telur (sortir & simpan)	12 x 8 m	B-04
5	Sumur bor + menara tandon	4 x 4 m	GT-03
6	Mes anak kandang	12 x 8 m	B-03
7	Ruang ganti + celup kaki	6 x 4 m	GT-03
8	Lantai jemur jagung	40 x 18 m	GT-03
9	Rumah pakan (olah & campur)	16 x 12 m	B-05
10	Gudang jagung	20 x 12 m	GT-03
11	Gudang pakan jadi	20 x 10 m	B-06
12	Rumah kompos	16 x 10 m	B-07
13	Rumah maggot BSF	12 x 8 m	B-08
14	Kandang karantina	8 x 6 m	GT-03
15	Insinerator	3 x 3 m	-
16	Embung 30 x 20 m	30 x 20 m	GT-03
17	Rumah pompa air sungai	6 x 6 m	GT-03

L1-L5 kandang layer 10 x 40 m, G kandang starter (GT-01)
Umbaran 45 x 38 m per kandang, pagar harmonika (GT-02)

SIMBOL

- Pagar keliling kawat harmonika 180 cm
- Pagar zona kandang & umbaran
- Jalan sirtu / perkerasan
- Pohon peneduh (mahoni, ketapang, gamal)
- Zona servis (bersih, terbuka untuk tamu)
- Umbaran rumput + pohon peneduh
- Zona kotor (kompos, maggot, karantina)
- Air: embung, sungai

KONSEP TAPAK


1. Urutan dari jalan ke sungai: servis (bersih, untuk tamu) - kandang (paling dijaga) - zona kotor - kebun - sungai.
2. Tamu, pembeli telur dan truk pakan berhenti di zona servis; tidak masuk zona kandang.
3. Pekerja masuk zona kandang hanya lewat ruang ganti + celup kaki; pakan lewat gudang pakan di garis pagar.
4. Jalan servis 4 m di sisi timur menuju zona kotor dan kebun tanpa melewati zona kandang.
5. Kandang dan kompos >100 m dari sungai; air minum ayam dari sumur bor, air sungai untuk irigasi.
6. Kompos dan maggot mengolah kotoran menjadi pupuk kebun dan protein pakan.

NERACA LAHAN

ZONA	JARAK DARI JALAN	LUAS (m²)	HA	%	ISI UTAMA
Zona servis	0 - 50 m	5.000	0,50	12,5	pos jaga, kantor, rumah telur, mes, parkir, jemur, rumah pakan, gudang
Zona kandang semi umbaran	50 - 210 m	16.000	1,60	40,0	6 kandang 10 x 40 m = 6 umbaran 45 x 38 m, jalan gerobak
Zona kotor + hijauan	210 - 245 m	3.500	0,35	8,8	rumah kompos, maggot BSF, karantina, insinerator, indigofera
Kebun jagung + embung	245 - 330 m	8.500	0,85	21,2	jagung A, B, C (0,58 ha), embung 30 x 20 m, rumah pompa
Sempadan, sungai, seberang	330 - 400 m	7.000	0,70	17,5	sabuk hijau, sungai, kebun hijauan seberang
JUMLAH		40.000	4,00	100,0	

POTONGAN SKEMATIK MEMANJANG KAWASAN (DIPROYEKSIKAN)

horizontal 1 : 500, vertikal 1 : 250 · kontur tanah belum diukur, kedalaman sungai perkiraan

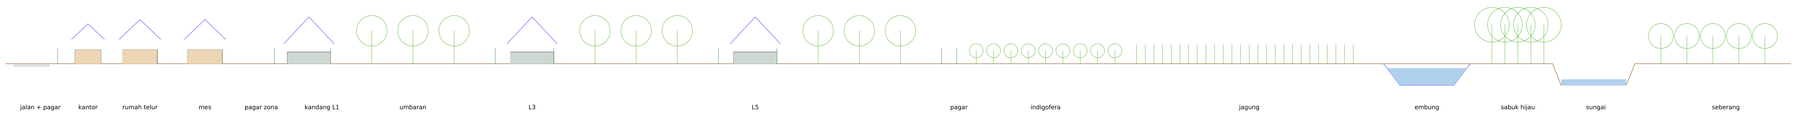

POTONGAN MELINTANG ZONA KANDANG

horizontal 1 : 500, vertikal 1 : 250 · lebar lahan 100 m



CATATAN

- Gambar ini acuan tata letak; ukuran bangunan detail lihat GT-01 (kandang), GT-03 dan GT-04 (bangunan pendukung).
- Koordinat pematokan zona servis: MP-02. Jalur air, listrik dan drainase: MP-03.
- Batas lahan dan posisi sungai mengikuti sketsa SITE PLAN LOKASI 1; lakukan pengukuran batas dan kontur sebelum pembangunan.
- Jarak sempadan sungai mengikuti ketentuan Dinas PUPR/BWS setempat.

PROYEK
PETERNAKAN AYAM KUB PETELUR SEMI UMBARAN 10.000 EKOR
ADEVA FARM – KAB. KONAWE SELATAN, SULAWESI TENGGARA

KERTAS A0

JUDUL GAMBAR
MASTERPLAN KAWASAN PETERNAKAN 4 HA

CATATAN
Satuan cm, elevasi terhadap lantai (±0).
Periksa ulang oleh ahli sipil.

SKALA
1 : 500

TANGGAL
OKTOBER 2026

STATUS
GAMBAR PERENCANAAN

NO. GAMBAR
MP-01

RENCANA TAPAK ZONA SERVIS

skala 1 : 200 · koordinat pematokan pada tabel; ukuran dalam meter pada tabel, dimensi gambar dalam cm



grid patok bantu 10 x 10 m (angka = meter dari sudut barat daya pagar)

KOORDINAT PEMATOKAN (as dinding / tepi, meter)

NO	BANGUNAN	x	y	P	L	GAMBAR
1	Pos jaga	41	1,5	4	3	B-01
2	Parkir tamu & pembeli	4	4	18	14	MP-02
3	Kantor	26	4	8	6	B-02
4	Rumah telur (sortir & simpan)	32	15	12	8	B-04
5	Sumur bor + menara tandon	4	24	4	4	GT-03
6	Mes anak kandang	12	30	12	8	B-03
7	Ruang ganti + celup kaki	38	46	6	4	GT-03
8	Lantai jemur jagung	54	3	40	18	GT-03
9	Rumah pakan (olah & campur)	54	25	16	12	B-05
10	Gudang jagung	74	25	20	12	GT-03
11	Gudang pakan jadi	54	40	20	10	B-06

x dari pagar barat, y dari pagar depan (sudut barat daya bangunan); P = panjang arah x, L = lebar arah y.

CATATAN PELAKSANAAN


- Patok bantu dipasang tiap 10 m dari sudut barat daya pagar; sudut bangunan diukur dari patok terdekat.
- Periksa siku dengan diagonal (3-4-5) sebelum memasang bouwplank.
- Peil lantai: kantor, mes, rumah telur +45; pos jaga, gudang, rumah pakan +30 dari tanah asli rata-rata.
- Teras kantor 1,5 m, mes 2 m, rumah telur 1,5 m di sisi selatan (sudah tergambar).
- Gudang pakan jadi dan ruang ganti berdiri di garis pagar zona kandang; pintu utara hanya dibuka dari dalam.
- Jarak septic tank ke sumur bor minimal 10 m (sumur di x 4-8, y 24-28).
- Jalan masuk, jalan parkir, jalan lingkungan, apron: sirtu dipadatkan t = 12 cm.
- Pohon peneduh ditanam 1 m dari pagar, jarak 8 m.

U

PROYEK	KERTAS A1
PETERNAKAN AYAM KUB PETELUR SEMI UMBARAN 10.000 EKOR ADEVA FARM - KAB. KONAWE SELATAN, SULAWESI TENGGARA	
JUDUL GAMBAR	
RENCANA TAPAK ZONA SERVIS (PEMATOKAN)	
CATATAN Satuan cm, elevasi terhadap lantai (±0). Periksa ulang oleh ahli sipil.	SKALA 1 : 200
TANGGAL OKTOBER 2026	STATUS GAMBAR PERENCANAAN
	NO. GAMBAR MP-02

RENCANA SIRKULASI DAN JARINGAN UTILITAS

skala 1 : 500 · lahan seberang sungai tidak digambar · jalur pipa dan kabel skematik, sesuaikan di lapangan

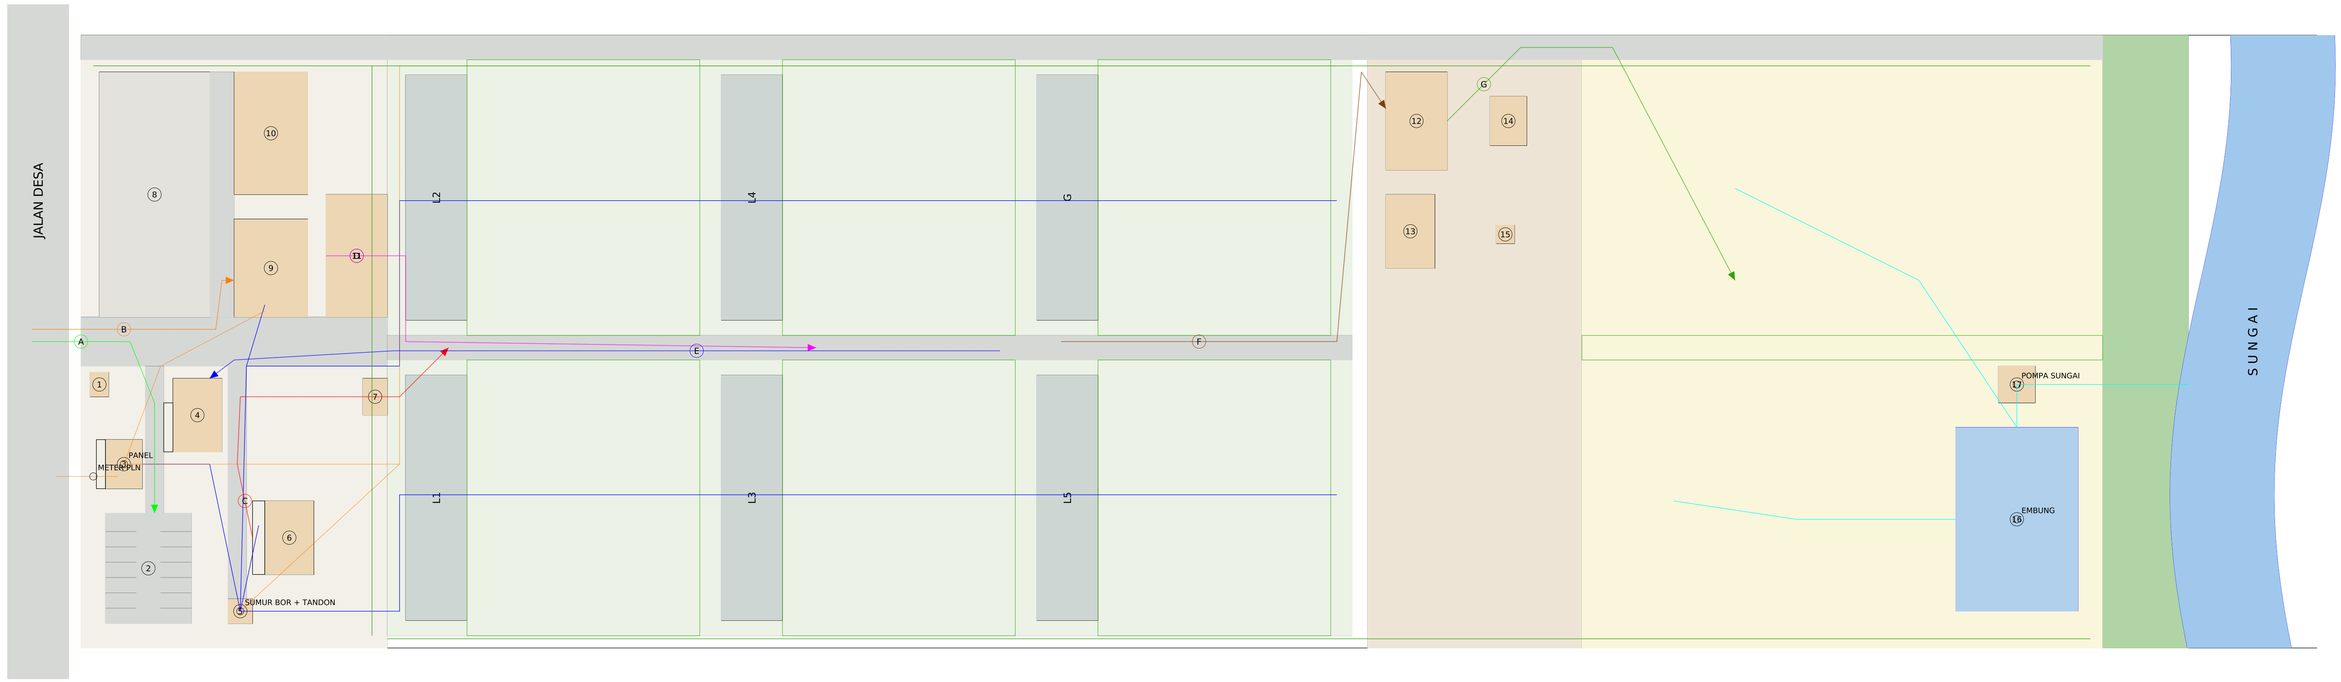

SIRKULASI (panah)

- A — Tamu & pembeli telur
- B — Truk pakan / bahan baku
- C — Pekerja: mes - ruang ganti - kandang
- D — Pakan jadi ke kandang
- E — Telur ke rumah telur
- F — Kotoran ke kompos & maggot
- G — Kompos ke kebun

UTILITAS

- Pipa air bersih PVC 1,5" (sumur bor - tandon - kandang & bangunan)
- Pipa air sungai PVC 3" (pompa - embung - kebun)
- Kabel listrik NYY 4x6 (PLN - panel kantor - zona kandang, rumah pakan, pompa)
- Saluran drainase tanah 40 x 40 (ke sungai melalui sabuk hijau)

CATATAN

- Alur bersih (tamu, pakan, telur) tidak berpotongan dengan alur kotor (kotoran, bangkai) yang lewat jalan servis timur.
- Air minum ayam dari sumur bor lewat menara tandon; tandon kecil + pipa paralon di tiap kandang.
- Air sungai hanya untuk embung dan irigasi kebun, tidak untuk ayam.
- Kabel listrik tanam kedalaman 60 cm dalam pipa PVC, diberi patok tanda.
- Drainase permukaan mengikuti kemiringan tanah menuju sungai; buat bak kontrol sebelum sabuk hijau.
- Posisi jalur perlu disesuaikan dengan kontur hasil pengukuran.

U

utara diasumsikan

ke arah jalan

PROYEK: PETERNAKAN AYAM KUB PETELUR SEMI UMBARAN 10.000 EKOR ADEVA FARM - KAB. KONAWE SELATAN, SULAWESI TENGGARA			KERTAS A1
JUDUL GAMBAR: RENCANA SIRKULASI DAN JARINGAN UTILITAS			
CATATAN: Satuan cm, elevasi terhadap lantai (±0). Periksa ulang oleh ahli sipil.		SKALA: 1 : 500	
TANGGAL: OKTOBER 2026	STATUS: GAMBAR PERENCANAAN		NO. GAMBAR: MP-03