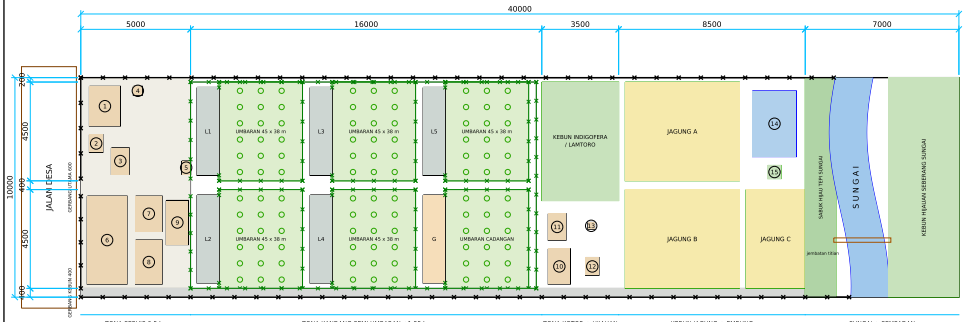


U

arah utara diasumsikan ke jalan - mohon dicek

KETERANGAN BANGUNAN

1. Parkir tamu & pembeli
2. Kantor + pos jaga
3. Gudang telur & sortir
4. Sumur bor + menara tandon
5. Ruang ganti + celup kaki
6. Lantai jemur jagung
7. Ruang olah pakan
8. Gudang jagung
9. Gudang pakan jadi
10. Rumah kompos
11. Unit maggot BSF
12. Kandang karantina
13. Insinerator
14. Embung 30 x 20 m
15. Rumah pompa air sungai

KONSEP TAPAK

1. Urutan dari jalan ke sungai: zona servis (bersih untuk tamu) - zona kandang (paling bersih, berpagar) - zona kotor - kebun - sungai.
2. Tamu, pembeli telur, dan truk pakan berhenti di zona servis; tidak masuk zona kandang.
3. Jalan servis 4 m di sisi timur menuju zona kotor dan kebun tanpa melewati zona kandang.
4. Kotoran dan bangkai keluar lewat gerbang belakang zona kandang ke zona kotor (kompos, maggot, insinerator).
5. Kandang dan kompos berjarak lebih dari 100 m dari sungai; air minum ayam dari sumur bor, air sungai untuk irigasi.
6. Tepi sungai dibiarkan hijau (bambu, lamtoro, rumput) untuk mencegah longsor dan pencemaran; ikuti ketentuan sempadan setempat.
7. Bentuk dan posisi sungai mengikuti sketsa pemilik; ukur ulang di lapangan sebelum pematokan.

PROYEK
PETERNAKAN AYAM KUB PETELUR SEMI UMBARAN 10.000 EKOR
ADEVA FARM - KAB. KONAWE SELATAN, SULAWESI TENGGARA

JUDUL GAMBAR
RENCANA TAPAK LAHAN 4 HA (100 X 400 M)


CATATAN
Satuan cm, elevasi terhadap lantai (±0).
Periksa ulang oleh ahli sipil.

SKALA
1 : 1000

TANGGAL
OKTOBER 2026

STATUS
GAMBAR PERENCANAAN


NO. GAMBAR
S-01

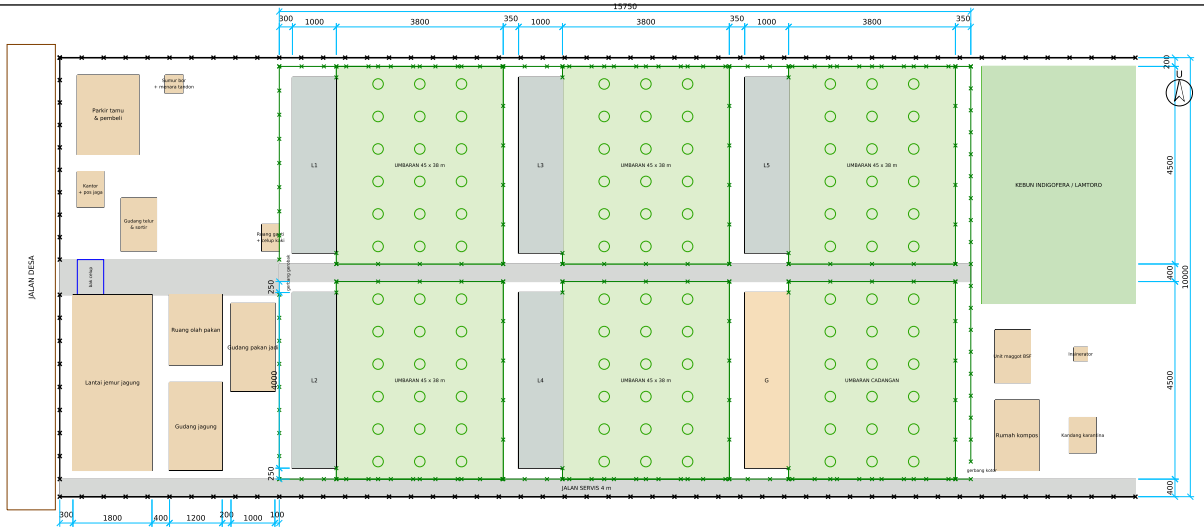

CATATAN

- Semua bangunan servis: struktur kolom beton 15/15, dinding bata, atap baja ringan + galvalum (lihat GT-03 fasilitas).
- Pagar zona kandang kawat harmonika 2" tinggi 180 cm + 30 cm ditanam, tiang beton pracetak 10/10 @250 (lihat P-01).
- Pagar sekat umbaran sama dengan pagar zona kandang, pintu umbaran 100 cm di sisi jalan gerobak.
- Ukuran dalam meter pada gambar ini (dimensi otomatis ditampilkan dalam cm).

PROYEK	PETERNAKAN AYAM KUB PETELUR SEMI UMBARAN 10.000 EKOR ADEVA FARM - KAB. KONAWE SELATAN, SULAWESI TENGGARA
JUDUL GAMBAR	TATA LETAK ZONA SERVIS, ZONA KANDANG DAN ZONA KOTOR
CATATAN Satuan cm, elevasi terhadap lantai (±0). Periksa ulang oleh ahli sipil.	SKALA 1 : 500
TANGGAL OKTOBER 2026	STATUS GAMBAR PERENCANAAN
	NO. GAMBAR S-02

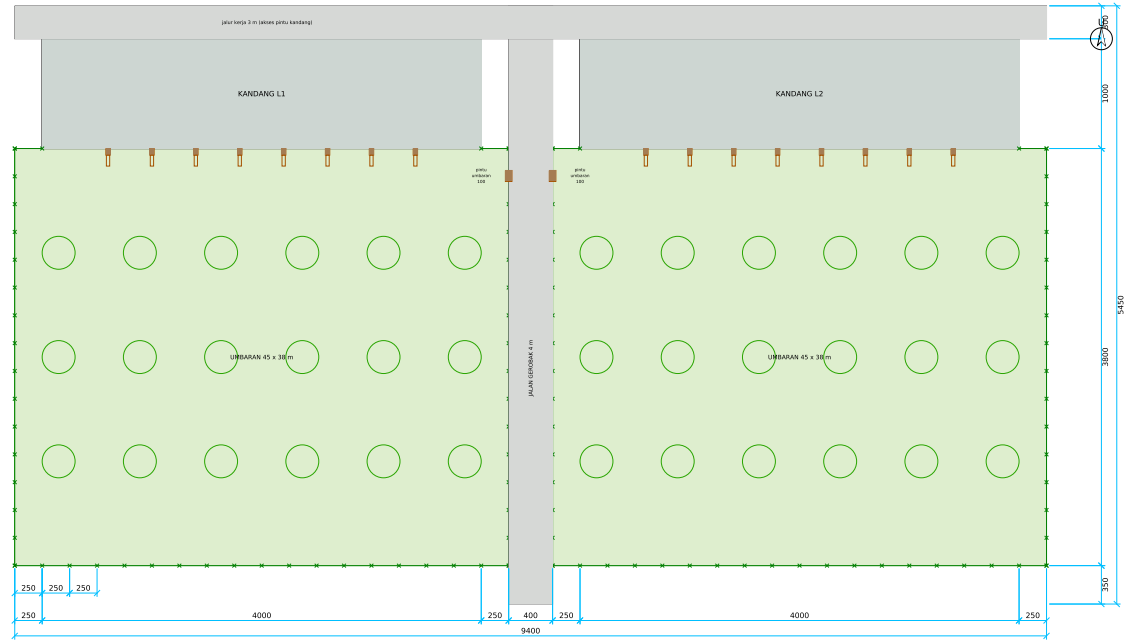


KETENTUAN UNIT

- Pagar umbaran: tiang beton pracetak 10/10 jarak 250 cm (titik pada gambar), kawat harmonika 2" BWG 12.
- Penedush 18 pohon per petak (3 baris x 6): lamtoro, indigofera, gamal, atau mangga/mangka; lindungi bibit dengan bronjong bambu 1 tahun pertama.
- Tanam rumput lokal/legum penutup tanah; petak yang gundul diistirahatkan dan diganti ke umbaran cadangan.
- Pintu umbaran ke kandang: 8 lubang 40 x 45 cm di dinding selatan (detail K-08).

PROYEK: PETERNAKAN AYAM KUB PETELUR SEMI UMBARAN 10.000 EKOR ADEVA FARM - KAB. KONAWE SELATAN, SULAWESI TENGGARA			
JUDUL GAMBAR: UNIT KANDANG DAN UMBARAN (TIPIKAL 1 BARIS)			
CATATAN: Satuan cm, elevasi terhadap lantai (±0). Periksa ulang oleh ahli sipil.		SKALA 1 : 200	
TANGGAL OKTOBER 2026	STATUS GAMBAR PERENCANAAN		NO. GAMBAR S-03


TAMPAK PAGAR 2 BENTANG

skala 1 : 20

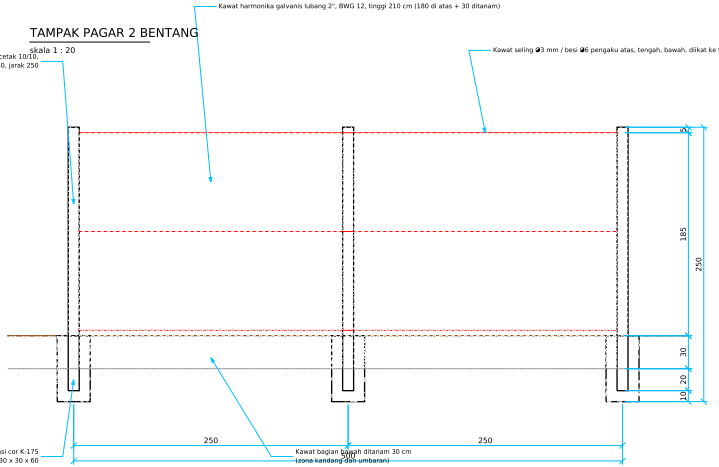

POTONGAN TIANG

skala 1 : 20

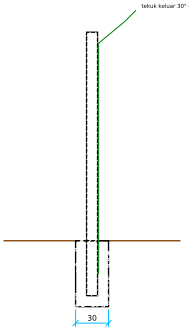

PENAMPANG TIANG



4 Ø6, sengkang Ø4-150, K-225


CATATAN PAGAR

- Tiang sudut dan setiap 25 m diberi skur (penopang miring) tiang beton yang sama.
- Pagar keliling lahan ±770 m, pagar zona kandang ±500 m, pagar sekat umbaran ±530 m.
- Tiang boleh dicor di lokasi dengan cetakan papan bila tidak ada pemasok pracetak.

PROYEK: PETERNAKAN AYAM KUB PETELUR SEMI UMBARAN 10.000 EKOR ADEVA FARM - KAB. KONAWE SELATAN, SULAWESI TENGGARA		
JUDUL GAMBAR: DETAIL PAGAR KAWAT HARMONIKA DAN TIANG BETON PRACETAK		
CATATAN: Satuan cm, elevasi terhadap lantai (±0). Periksa ulang oleh ahli sipil.	SKALA 1 : 20	
TANGGAL OKTOBER 2026	STATUS GAMBAR PERENCANAAN	NO. GAMBAR P-01


GERBANG UTAMA 600 cm (2 DAUN GESER/ENGSEL)


skala 1 : 50 · gerbang kebun 400 dan gerbang gerobak 300 sama, 1 atau 2 daun

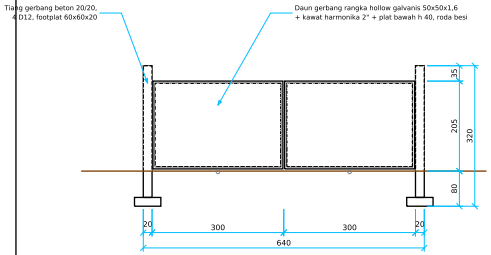

BAK CELUP KENDARAAN (DENAH + POTONGAN)

skala 1 : 50 · di gerbang utama

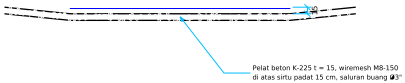

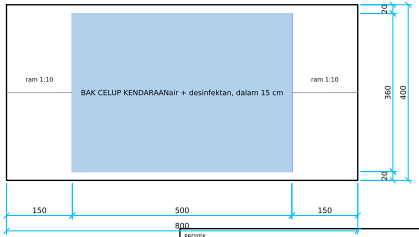

PROYEK: PETERNAKAN AYAM KUB PETELUR SEMI UMBARAN 10.000 EKOR ADEVA FARM - KAB. KONAWE SELATAN, SULAWESI TENGGARA			
JUDUL GAMBAR: DETAIL GERBANG DAN BAK CELUP KENDARAAN			
CATATAN: Satuan cm, elevasi terhadap lantai (±0). Periksa ulang oleh ahli sipil.		SKALA 1 : 50	
TANGGAL OKTOBER 2026	STATUS GAMBAR PERENCANAAN		NO. GAMBAR P-02