

DENAH GUDANG TIPIKAL

skala 1 : 100

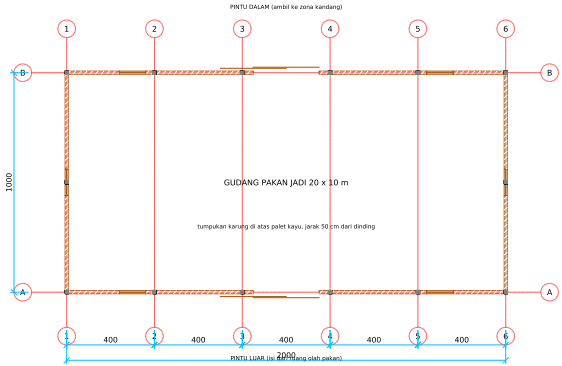

POTONGAN MELINTANG

skala 1 : 100

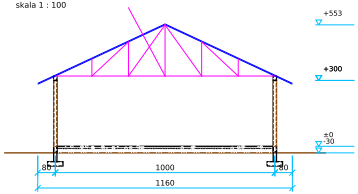

TABEL BANGUNAN FASILITAS (STRUKTUR TIPIKAL SAMA)


BANGUNAN	UKURAN (cm)	DINDING BATA	LANTAI	PINTU	KETERANGAN
Gudang pakan jadi	2000 x 1000	h 300 penuh	beton t=10	300 x 300 (2)	F-01
Ruang pengolahan pakan	1600 x 1200	h 150 + kawat	beton t=10	300 x 300 (2)	F-01 (dinding 150 + kawat)
Gudang jagung	2000 x 1200	h 300 penuh	beton t=10	300 x 300 (2)	F-01 (bentang 12 m)
Gudang telur & sortir	1200 x 800	h 300 penuh	beton t=10	120 x 210 (2)	F-01, plafon + ventilasi
Kantor + pos jaga	800 x 600	h 300 penuh	beton t=10	90 x 210 (2)	F-02
Ruang ganti + celup kaki	600 x 400	h 300 penuh	beton t=10	90 x 210 (2)	F-02
Rumah kompos	1600 x 1000	h 100 + kawat	beton t=10	terbuka	F-03
Unit maggot BSF	1200 x 800	h 100 + kawat	beton t=10	120 x 210 (1)	F-03
Kandang karantina	800 x 600	h 50 + kawat	beton t=7	90 x 200 (1)	F-03

SPESIFIKASI TIPIKAL FASILITAS
• Footplat 70x70x20, kolom 15/15, sloef 15/25, ring balk 15/20, beton K-225 (sama dengan kandang, K-05/K-06).
• Kolom jarak ±400 cm, tinggi kolom 300 cm dari lantai.
• Dinding bata 1/2 bata, plester + aci dua sisi, dicat.
• Lantai beton K-175 t = 10 di atas pasir 5 cm dan urugan dipadatkan; peil ±0 dari tanah.• Atap baja ringan C75 jarak 120, galvalum 0,30 TCT, kemiringan 25°, overstek 80.• Pintu gudang 300 x 300 geser: rangka hollow 40x40 + plat galvalum; jendela ventilasi kawat nyamuk + teralis.
• Gudang pakan/jagung: celah bawah pintu ditutup karet, lubang angin dipasang kawat (anti tikus dan burung).

PROYEK	PETERNAKAN AYAM KUB PETELUR SEMI UMBARAN 10.000 EKOR ADEVA FARM - KAB. KONAWE SELATAN, SULAWESI TENGGARA
JUDUL GAMBAR	GUDANG TIPIKAL (GUDANG PAKAN JADI 20 X 10 M)
CATATAN	Satuan cm, elevasi terhadap lantai (±0). Periksa ulang oleh ahli sipil.
SKALA	1 : 100
TANGGAL	OKTOBER 2026
STATUS	GAMBAR PERENCANAAN
NO. GAMBAR	F-01


DENAH KANTOR + POS JAGA 8 x 6 m

skala 1 : 50

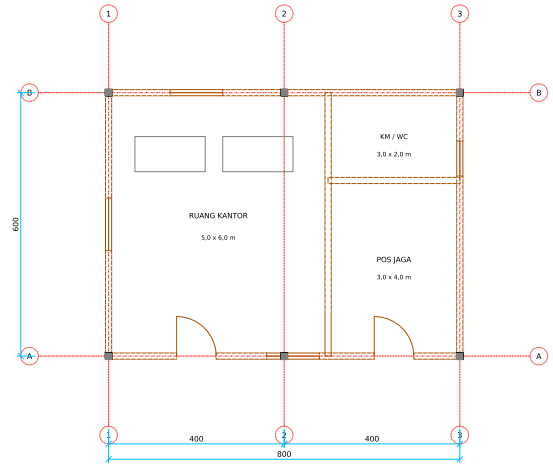

DENAH RUANG GANTI + CELUP KAKI 6 x 4 m

skala 1 : 50 · alur satu arah: luar - mandi - dalam

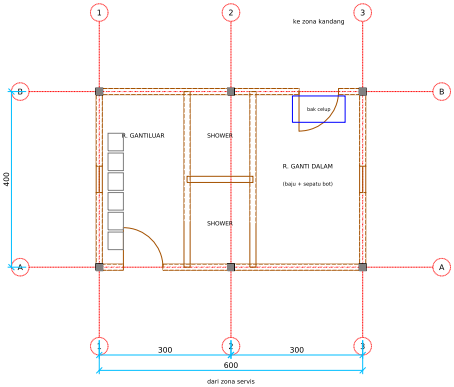


CATATAN

- Struktur dan atap sama dengan gudang tipikal F-01; lantai keramik 40x40 di kantor, lantai beton kasar + kemiringan 1% di ruang ganti.
- Plafon GRC 4 mm rangka hollow di kantor dan pos jaga; KM/WC dengan septic tank biofil 1 m³.
- Ruang ganti dibangun menempel pagar zona kandang: pintu luar dari zona servis, pintu dalam langsung ke zona kandang.
- Pakaian dan sepatu kandang tidak boleh dibawa keluar zona kandang.

PROYEK: PETERNAKAN AYAM KUB PETELUR SEMI UMBARAN 10.000 EKOR ADEVA FARM - KAB. KONAWE SELATAN, SULAWESI TENGGARA		
JUDUL GAMBAR: KANTOR + POS JAGA DAN RUANG GANTI + CELUP KAKI		
CATATAN: Satuan cm, elevasi terhadap lantai (±0). Periksa ulang oleh ahli sipil.	SKALA: 1 : 50	
TANGGAL: OKTOBER 2026	STATUS: GAMBAR PERENCANAAN	NO. GAMBAR: F-02


DENAH RUMAH KOMPOS 16 x 10 m

skala 1 : 100 · dinding bata h 100, 4 bak bergilir 1 minggu

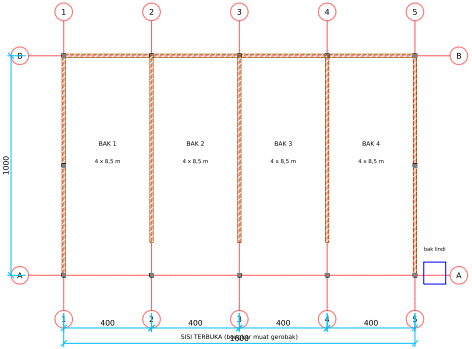


POTONGAN RUMAH KOMPOS

skala 1 : 100

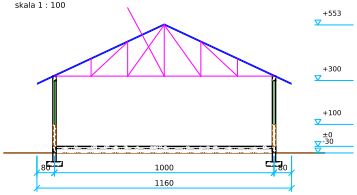


DENAH UNIT MAGGOT BSF 12 x 8 m

skala 1 : 100 · bata h 100 + kasa nyamuk di atasnya

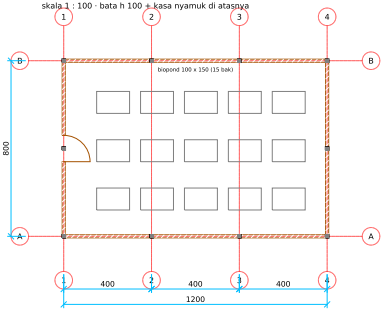

DENAH KANDANG KARANTINA 8 x 6 m

skala 1 : 100 · detail seperti kandang K-04/K-08

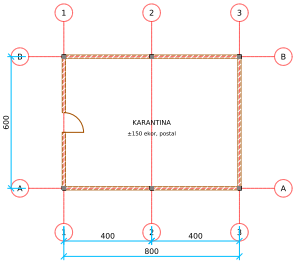


CATATAN

- Rumah kompos: lantai beton K-175 t=10 miring 1% ke saluran dan bak lindi 100x100x100; air lindi disiram kembali ke tumpukan.
- Atap rumah kompos menutup penuh agar kompos tidak kehujanan.
- Unit BSF: dinding bata 100 + kasa nyamuk sampai ring balk agar lalat BSF dewasa tidak lepas.
- Karantina untuk ayam baru/sakit, dijauhkan dari kandang utama, alat kerja tersendiri.

PROYEK	PETERNAKAN AYAM KUB PETELUR SEMI UMBARAN 10.000 EKOR ADEVA FARM · KAB. KONAWE SELATAN, SULAWESI TENGGARA		
JUDUL GAMBAR	RUMAH KOMPOS, UNIT MAGGOT BSF DAN KANDANG KARANTINA		
CATATAN Satuan cm, elevasi terhadap lantai (±0). Periksa ulang oleh ahli sipil.		SKALA 1 : 100	
TANGGAL OKTOBER 2026	STATUS GAMBAR PERENCANAAN		NO. GAMBAR F-03

DENAH LANTAI JEMUR 40 x 18 m

skala 1 : 100 · dilatasi tiap 300 cm (isi aspal/karet)

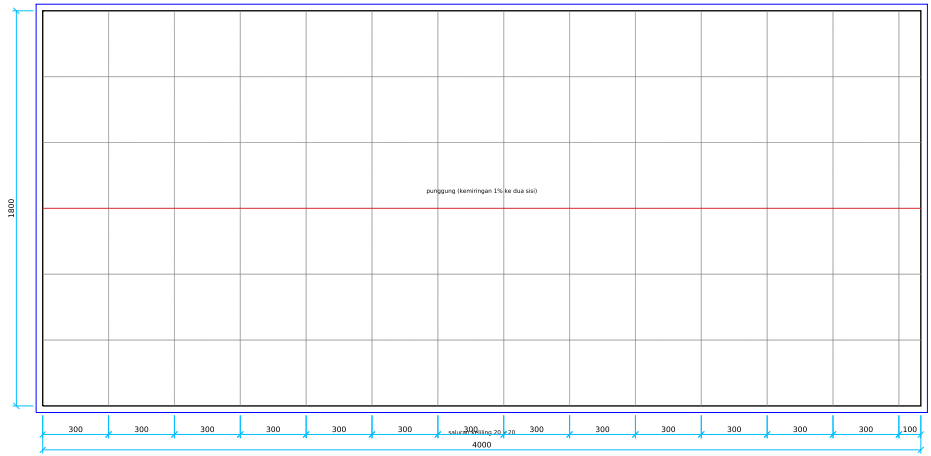


MENARA TANDON + SUMUR BOR

skala 1 : 100 · zona servis

POTONGAN LANTAI JEMUR (tebal digambar tanpa skala)



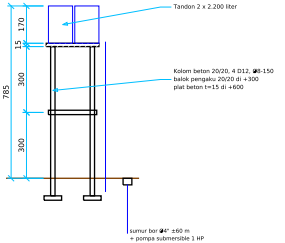


RUMAH POMPA AIR SUNGAI 3 x 3 m



PROYEK	PETERNAKAN AYAM KUB PETELUR SEMI UMBARAN 10.000 EKOR ADEVA FARM · KAB. KONAWE SELATAN, SULAWESI TENGGARA
JUDUL GAMBAR	LANTAI JEMUR JAGUNG, MENARA TANDON, SUMUR BOR DAN RUMAH POMPA
CATATAN	Satuan cm, elevasi terhadap lantai (±0). Periksa ulang oleh ahli sipil.
SKALA	1 : 100
TANGGAL	OKTOBER 2026
STATUS	GAMBAR PERENCANAAN
NO. GAMBAR	F-04

DENAH EMBUNG


skala 1 : 200

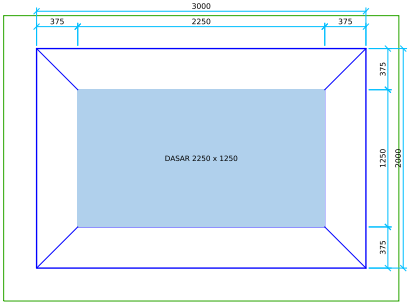

tanggul / jalan inspeksi lebar 300 ditanami rumput

POTONGAN EMBUNG

skala 1 : 200 · volume tampung ±1.000 m³

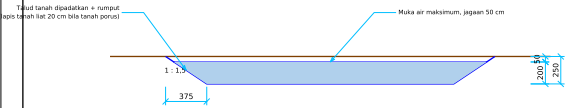

CATATAN
- Embung diisi pompa dari sungai saat musim hujan, dipakai untuk irigasi jagung musim kemarau.
- Air embung dan sungai tidak untuk minum ayam (pakai sumur bor).
- Pagar keliling embung kawat harmonika 120 cm untuk keselamatan anak dan ternak.
- Tanah galian dipakai untuk urugan peninggian lantai kandang dan bangunan.

PROYEK: PETERNAKAN AYAM KUB PETELUR SEMI UMBARAN 10.000 EKOR ADEVA FARM - KAB. KONAWE SELATAN, SULAWESI TENGGARA			
JUDUL GAMBAR: EMBUNG PENAMPUNG AIR 30 X 20 X 2,5 M			
CATATAN: Satuan cm, elevasi terhadap lantai (±0). Periksa ulang oleh ahli sipil.		SKALA: 1 : 200	
TANGGAL: OKTOBER 2026	STATUS: GAMBAR PERENCANAAN		NO. GAMBAR: F-05