
# RUMAH MAKAN "SELERA NUSANTARA"

GAMBAR RENCANA TEKNIS — RUMAH MAKAN 1 LANTAI · KAPASITAS ± 66 KURSI

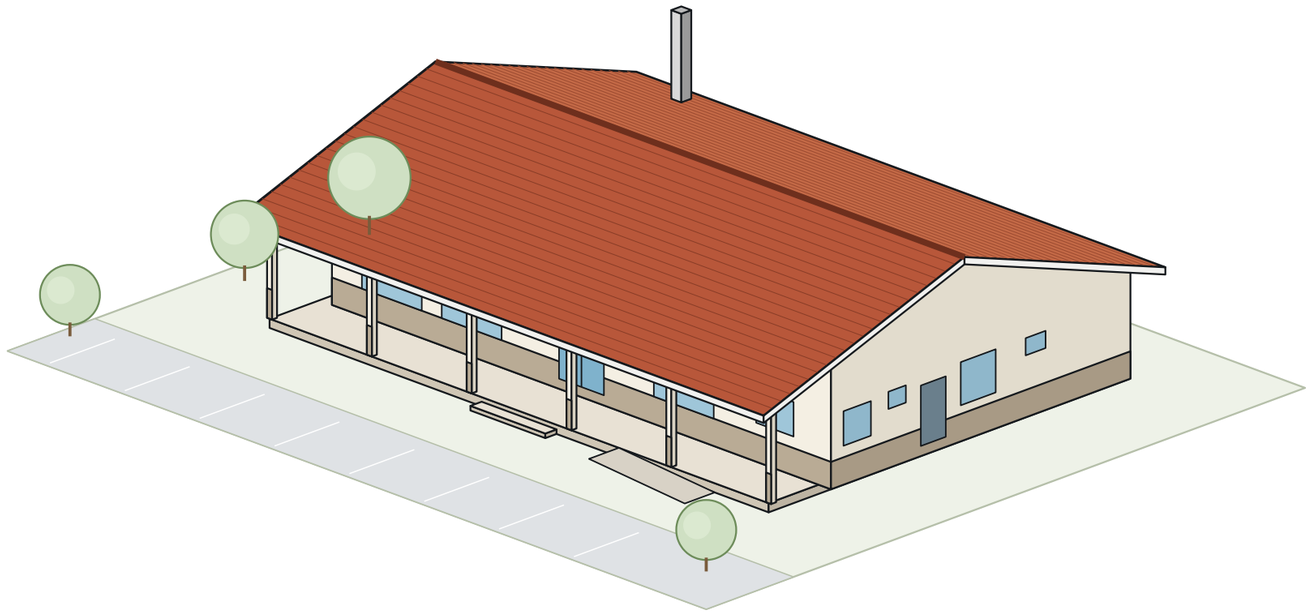

*PERSPEKTIF AKSONOMETRIK (ilustrasi, tanpa skala)*

## DAFTAR GAMBAR

| No. | Judul gambar | Skala |
|---|---|---|
| A-00 | Sampul, perspektif, daftar gambar | — |
| A-01 | Denah situasi (site plan) | 1:200 |
| A-02 | Denah lantai 1 — arsitektur | 1:100 |
| A-03 | Denah layout furnitur & peralatan | 1:100 |
| A-04 | Denah pondasi & sloof | 1:100 |
| A-05 | Tampak depan & belakang | 1:100 |
| A-06 | Tampak kiri & kanan | 1:100 |
| A-07 | Potongan I-I & II-II | 1:100 |
| A-08 | Rencana atap | 1:100 |
| A-09 | Detail konstruksi | 1:25 / 1:5 |
| A-10 | Jadwal pintu, jendela & finishing | — |

## DATA PROYEK

| Uraian | Keterangan |
|---|---|
| Fungsi | Rumah makan (restoran) keluarga + musala |
| Jumlah lantai | 1 lantai, atap pelana 20° |
| Lahan (asumsi) | 28 × 33 m = 924 m² |
| Luas bangunan | 244.8 m² + teras 48.9 m² |
| KDB / KLB | ± 31,8 % / 0,32 |
| Kapasitas | 42 kursi dalam + 24 kursi teras = 66 |
| Modul struktur | As 4,00 m × (5,00 + 7,00 m) + teras 2,40 m |
| Tinggi | Plafon +3,20 · atap +6,38 · lantai ±0,00 = +0,35 dari tanah |

## PROGRAM RUANG

Ruang makan • Teras makan luar • Dapur • Gudang • Counter saji/etalase • Kasir • WC pria/wanita/difabel • Lobi wastafel • Tempat wudhu • Musala • Area parkir mobil & motor • Ruang servis (TPS, bak lemak, septic)

## CATATAN UMUM

1. Gambar ini adalah rencana teknis awal (gambar rencana/DED tahap awal) untuk diskusi dan pengurusan perizinan.
2. Ukuran dalam cm, elevasi dalam m, kecuali tertulis lain; as ke as dinding.
3. Ukuran lahan, daya dukung tanah, dan sempadan belum terverifikasi — wajib disesuaikan.
4. Struktur & MEP dihitung/digambar terpisah oleh tenaga ahli bersertifikat.
5. Dapur harus mengikuti standar higiene sanitasi rumah makan (Permenkes) dan sertifikasi laik higiene sanitasi setempat.
6. Nama proyek, lokasi & pemilik adalah isian sementara (placeholder).

PROYEK

**RUMAH MAKAN "SELERA NUSANTARA"**

Perencanaan Bangunan Rumah Makan 1 Lantai
Kapasitas ± 66 Kursi

LOKASI

(diisi sesuai lahan terpilih)

PEMILIK

(diisi nama pemilik)

**KETERANGAN / CATATAN**

Seluruh lembar berukuran A3 (420 × 297 mm).

Skala tercetak benar pada A3.

Dibuat sebagai file SVG & PDF.

**REVISI**


| No | Tanggal | Keterangan |
|---|---|---|
| 0 | 26-10-2026 | Gambar rencana (usulan awal) |
| | | |

| | |
|---|---|
| Digambar | Drafter (Claude) |
| Diperiksa | _____ |
| Disetujui | _____ |
| Tanggal | 26 Oktober 2026 |

JUDUL GAMBAR

**SAMPUL & DAFTAR GAMBAR**

| NO. GAMBAR | SKALA | LEMBAR |
|---|---|---|
| **A-00** | — | 1/11 |

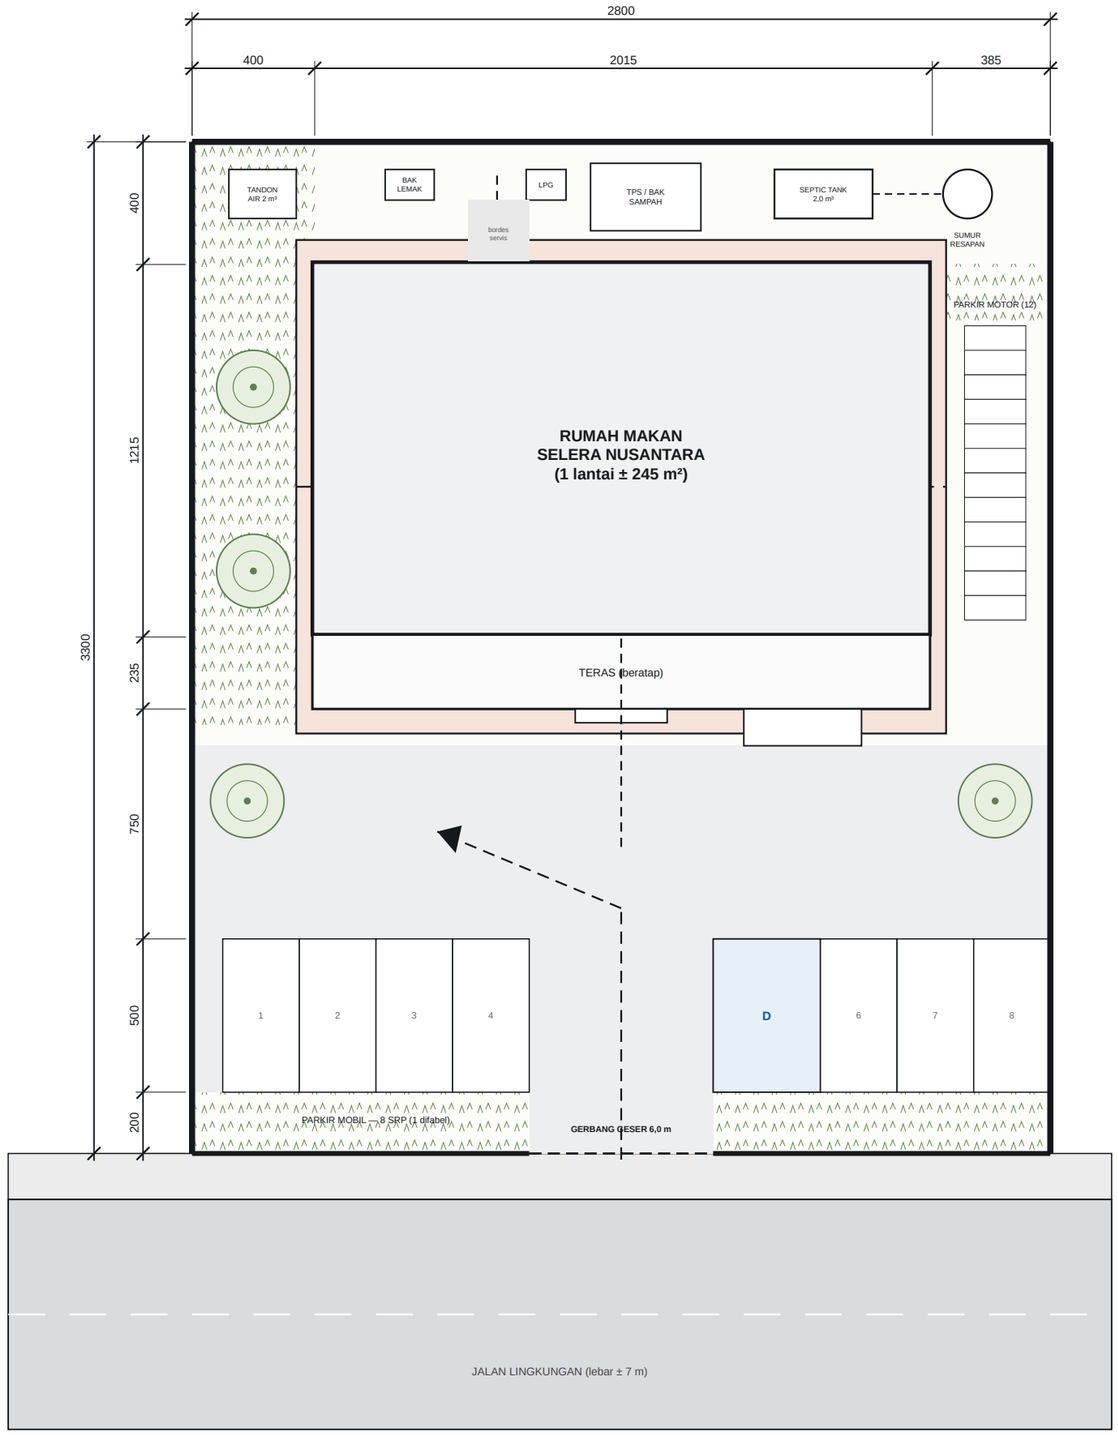


**DENAH SITUASI (SITE PLAN)** SKALA 1 : 200

U

0 2 4 6 8 10 m

**SKALA 1 : 200**

**DATA LAHAN & BANGUNAN (ASUMSI)**

| Uraian | Hitungan | Hasil |
|---|---|---|
| Luas lahan | 28,0 × 33,0 | 924 m² |
| Luas bangunan lt.1 | 20,15 × 12,15 | 244.8 m² |
| Luas teras beratap | 20,15 × 2,43 | 48.9 m² |
| Total beratap (KDB) | | 293.7 m² |
| KDB (terbangun) | 293.7 / 924 | 31.8 % |
| KLB | 1 lantai | 0.32 |
| Sempadan belakang | | ± 3,9 m |
| Sempadan samping | kiri / kanan | ± 3,9 m |
| Parkir mobil / motor | | 8 SRP / 12 |

**LEGENDA**

- Pagar bata h=2,0 (samping & belakang)
- Taman / resapan (RTH)
- Proyeksi atap + bubungan
- Perkerasan paving block / beton

**CATATAN**

Orientasi muka bangunan ke selatan (jalan).

Lahan diasumsikan datar, persegi 28×33 m; sesuaikan dengan sertifikat/IMB & GSB setempat sebelum konstruksi.

Pengolahan limbah: bak lemak → septic tank → sumur resapan (jarak ≥10 m dari sumber air bersih).

Drainase keliling lahan U-ditch 30×40.

PROYEK

# RUMAH MAKAN "SELERA NUSANTARA"

Perencanaan Bangunan Rumah Makan 1 Lantai
Kapasitas ± 66 Kursi

LOKASI

(diisi sesuai lahan terpilih)

PEMILIK

(diisi nama pemilik)

**KETERANGAN / CATATAN**

Satuan: meter (kecuali tertulis lain).

Gambar asumsi — lokasi & ukuran lahan belum ditentukan.

Lihat A-02 untuk denah lantai.

**REVISI**


| No | Tanggal | Keterangan |
|---|---|---|
| 0 | 26-10-2026 | Gambar rencana (usulan awal) |
| | | |

| | |
|---|---|
| Digambar | Drafter (Claude) |
| Diperiksa | _____ |
| Disetujui | _____ |
| Tanggal | 26 Oktober 2026 |

JUDUL GAMBAR

## DENAH SITUASI (SITE PLAN)

| NO. GAMBAR | SKALA | LEMBAR |
|---|---|---|
| A-01 | 1 : 200 | 2/11 |

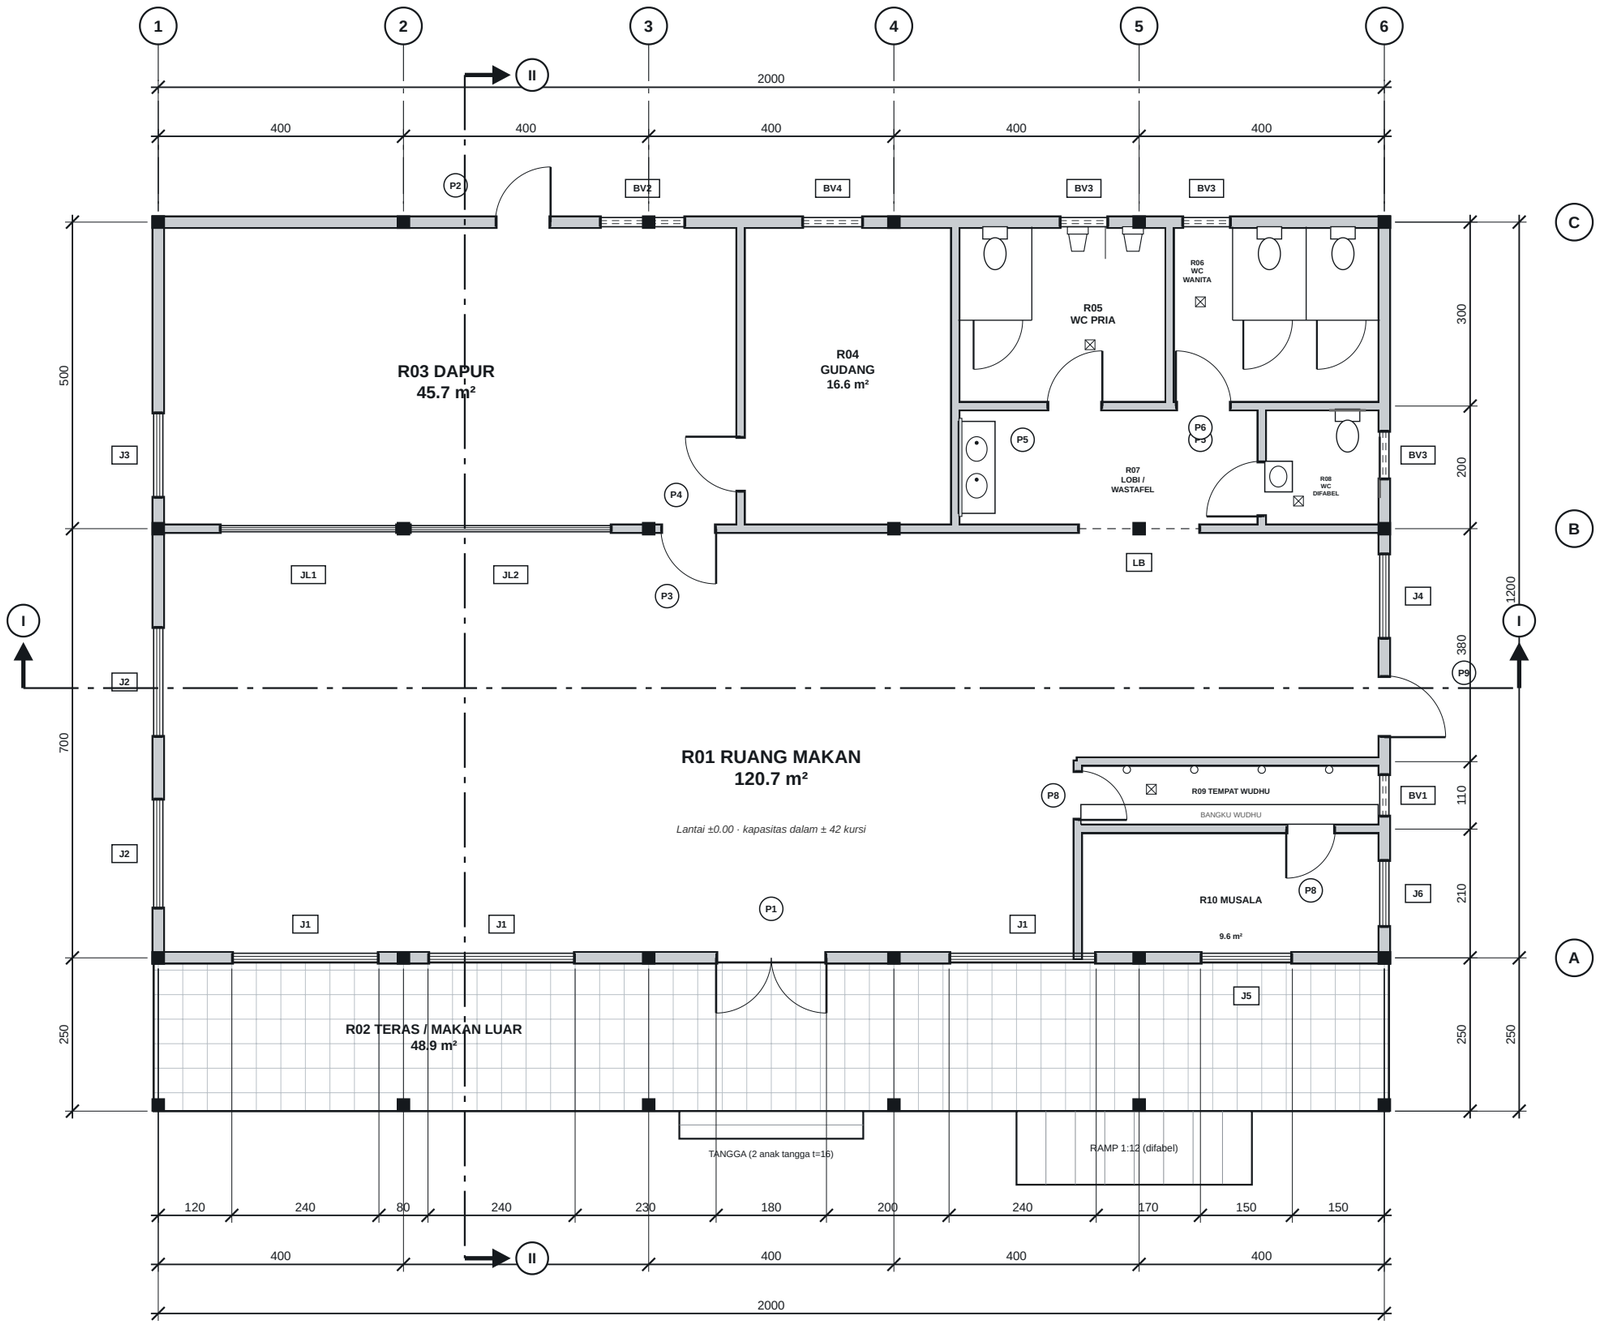


| Kode | Nama Ruang | Luas m² |
|---|---|---|
| R01 | Ruang Makan | 120.7 |
| R02 | Teras / Makan Luar | 48.9 |
| R03 | Dapur | 45.7 |
| R04 | Gudang Kering | 16.6 |
| R05 | WC Pria | 9.8 |
| R06 | WC Wanita | 9.7 |
| R07 | Lobi / Wastafel | 9.3 |
| R08 | WC Difabel | 3.6 |
| R09 | Tempat Wudhu | 4.9 |
| R10 | Musala | 9.6 |

Luas bangunan (as-as) 20,15 × 12,15 = 244.8 m²

Luas teras = 48.9 m²

**Kapasitas: 42 kursi dalam + 24 teras = 66**

**LEGENDA**

- Dinding bata ½ bata (t=15) / partisi (t=10)
- Kolom beton K1 20/20
- Pintu + arah bukaan
- Jendela / bovenlicht (garis putus = tinggi)

U

## DENAH LANTAI 1 SKALA 1 : 100

Rencana arsitektur — ukuran as ke as (cm)

PROYEK

# RUMAH MAKAN "SELERA NUSANTARA"

Perencanaan Bangunan Rumah Makan 1 Lantai
Kapasitas ± 66 Kursi

LOKASI

(diisi sesuai lahan terpilih)

PEMILIK

(diisi nama pemilik)

**KETERANGAN / CATATAN**

Satuan ukuran: cm, kecuali ditulis lain. Elevasi dalam meter. ±0.00 = lantai ruang makan.

Ukuran denah as ke as dinding, kecuali dinyatakan lain.

Gambar adalah rencana awal; ukuran lapangan wajib dicek sebelum pelaksanaan.

Kode pintu (P) & jendela (J/BV) lihat Jadwal di lembar A-10.

Garis potongan I-I & II-II lihat lembar A-07.

**REVISI**


| No | Tanggal | Keterangan |
|---|---|---|
| 0 | 26-10-2026 | Gambar rencana (usulan awal) |
| | | |

| | |
|---|---|
| Digambar | Drafter (Claude) |
| Diperiksa | _____ |
| Disetujui | _____ |
| Tanggal | 26 Oktober 2026 |

JUDUL GAMBAR

# DENAH LANTAI 1 (Arsitektur)

| NO. GAMBAR | SKALA | LEMBAR |
|---|---|---|
| A-02 | 1 : 100 | 3/11 |

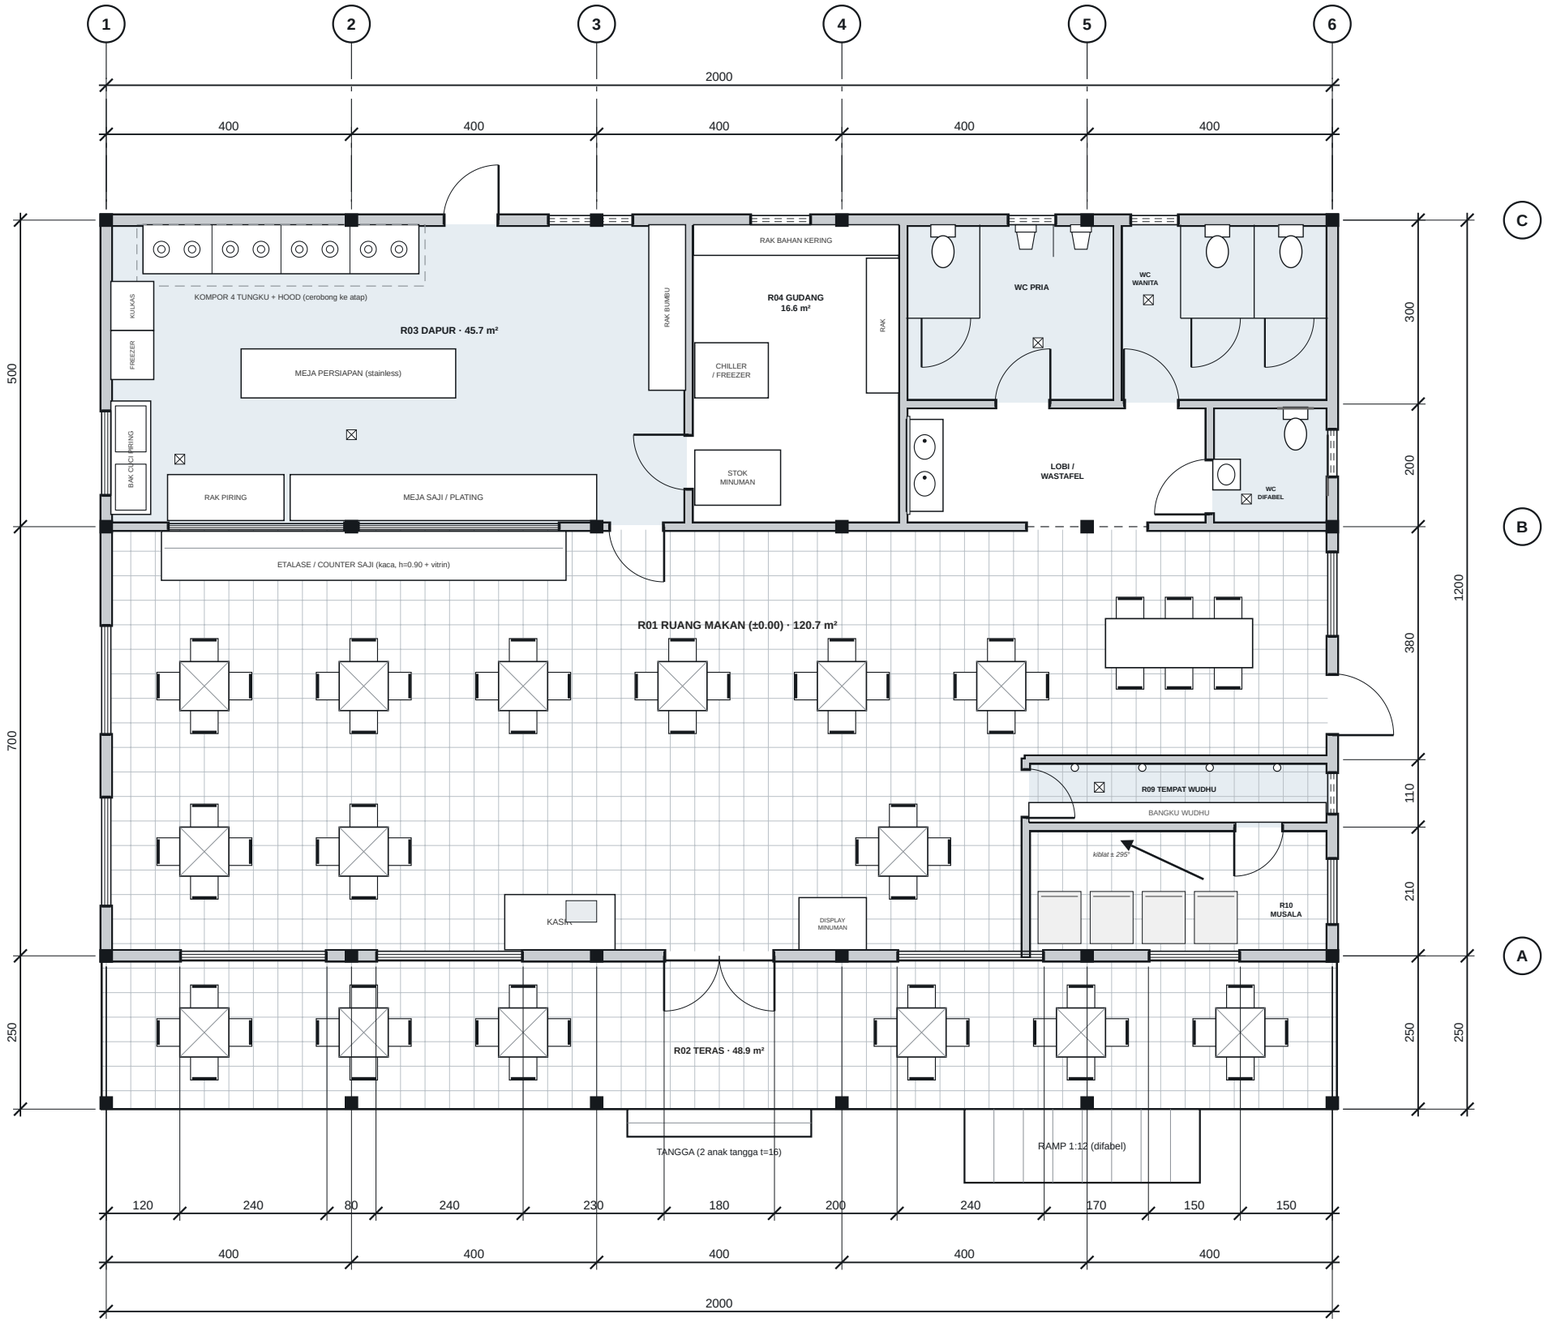


## DENAH LAYOUT FURNITUR & PERALATAN SKALA 1 : 100

Tata kursi meja, dapur, musala — kapasitas 66 kursi

### RINGKASAN KAPASITAS

| Jenis | Unit | Kursi |
|---|---|---|
| Meja 4 kursi (dalam) | 9 | 36 |
| Meja panjang 6 kursi | 1 | 6 |
| Meja 4 kursi (teras) | 6 | 24 |
| JUMLAH | | 66 |

**Standar yang dipakai:**

- Meja 80×80, kursi 45×45
- Jarak as meja 2,4–2,7 m
- Jalur sirkulasi ≥ 90 cm
- Lorong dapur ≥ 120 cm
- Etalase tinggi 90 cm
- Luas ruang makan ≈ 2.9 m²/kursi

PROYEK

# RUMAH MAKAN "SELERA NUSANTARA"

Perencanaan Bangunan Rumah Makan 1 Lantai
Kapasitas ± 66 Kursi

LOKASI

(diisi sesuai lahan terpilih)

PEMILIK

(diisi nama pemilik)

**KETERANGAN / CATATAN**

Satuan ukuran: cm, kecuali ditulis lain. Elevasi dalam meter. ±0.00 = lantai ruang makan.

Ukuran denah as ke as dinding, kecuali dinyatakan lain.

Gambar adalah rencana awal; ukuran lapangan wajib dicek sebelum pelaksanaan.

Area biru muda = area basah (dapur, WC, wudhu) lantai turun 2–5 cm.

Peralatan dapur indikatif; sesuaikan menu & vendor.

**REVISI**


| No | Tanggal | Keterangan |
|---|---|---|
| 0 | 26-10-2026 | Gambar rencana (usulan awal) |
| | | |

| | |
|---|---|
| Digambar | Drafter (Claude) |
| Diperiksa | _____ |
| Disetujui | _____ |
| Tanggal | 26 Oktober 2026 |

JUDUL GAMBAR

## DENAH LAYOUT FURNITUR & PERALATAN

| NO. GAMBAR | SKALA | LEMBAR |
|---|---|---|
| A-03 | 1 : 100 | 4/11 |

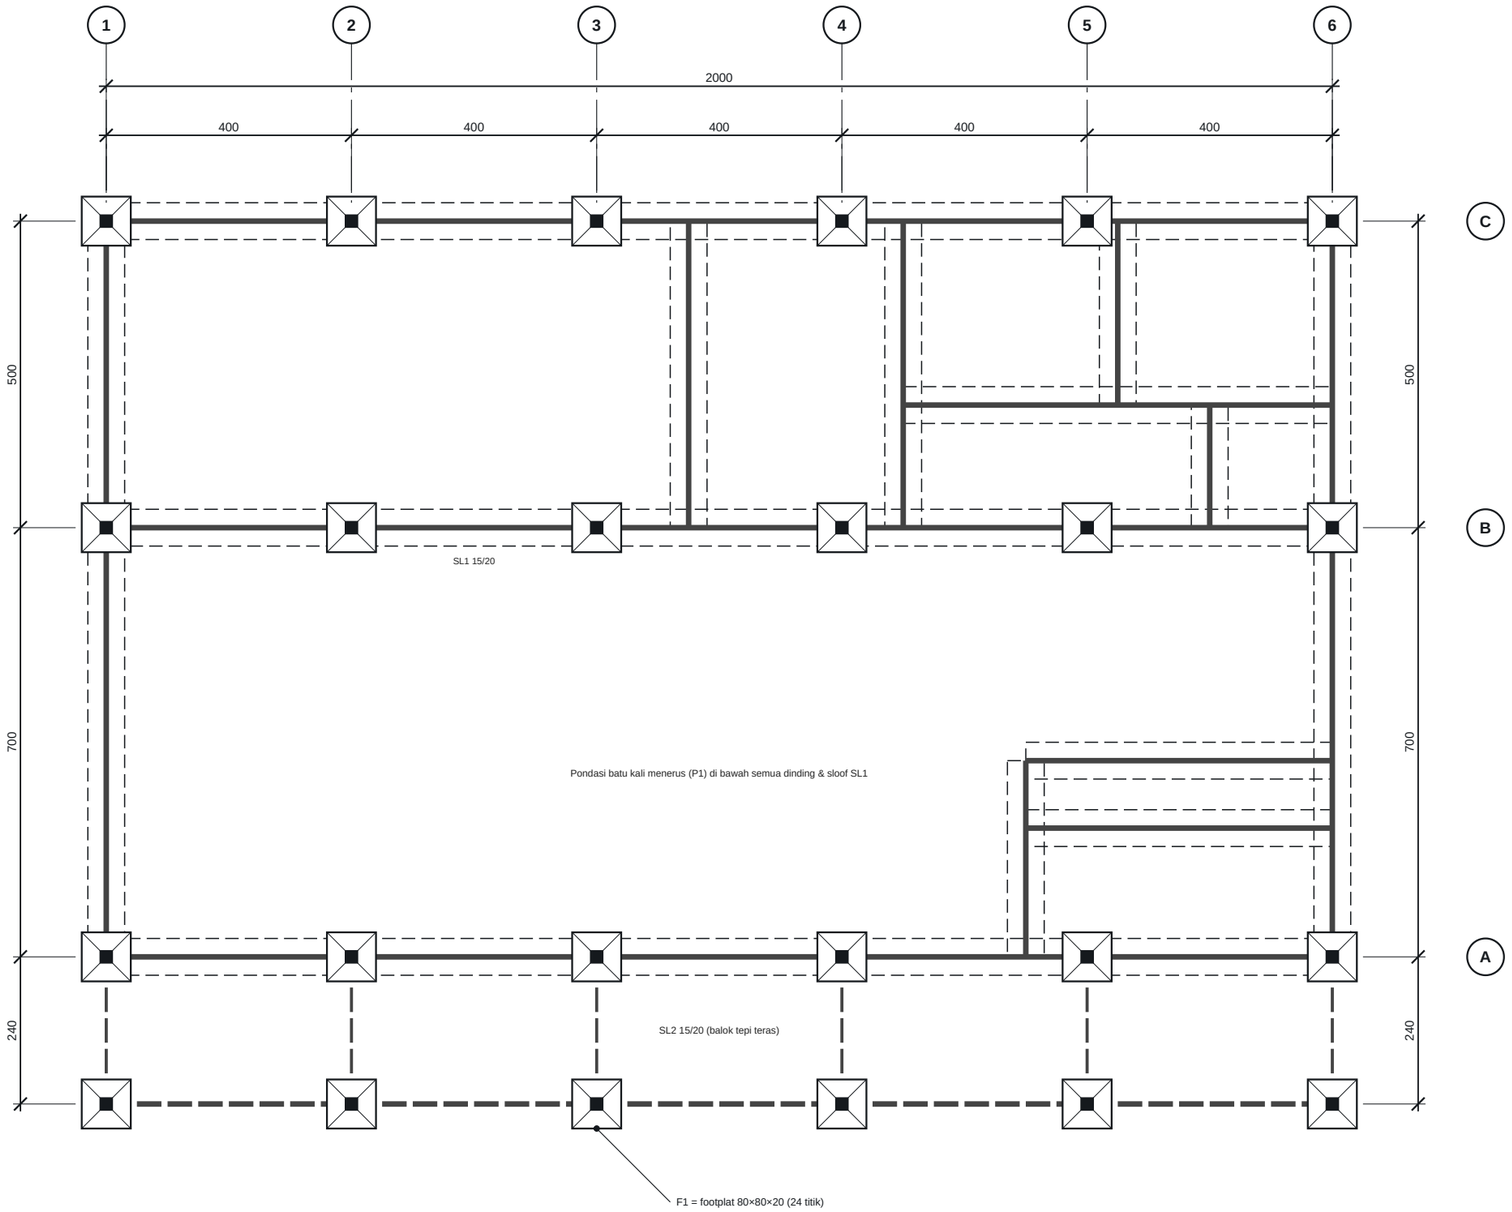


**TABEL TIPE STRUKTUR**

| | |
|---|---|
| **P1** | Pondasi batu kali menerus: atas 30, bawah 60, tinggi 80; di atas lantai kerja pasir t=10 |
| **F1** | Footplat setempat 80×80×20; tulangan Ø12-150 dua arah; di bawah kolom as |
| **K1** | Kolom beton 20/20; 4Ø12, sengkang Ø6-150; mutu K-225 |
| **SL1** | Sloof 15/20; 4Ø10, sengkang Ø6-150 |
| **SL2** | Balok tepi teras 15/20; 4Ø10, sengkang Ø6-150 |
| **RB** | Ring balk 15/20; 4Ø10, sengkang Ø6-150 (lihat A-07) |

**CATATAN STRUKTUR**

Daya dukung tanah diasumsikan ≥ 1,0 kg/cm²; wajib uji sondir/boring bila tanah lunak.

Kedalaman pondasi 80 cm dari tanah asli (−1,15 dari ±0,00); sesuaikan kondisi.

Mutu beton K-225, baja BJTP-24 (polos) / BJTD-40 (ulir).

Kolom di as 1-6 × A-C selalu bertumpu pada footplat F1 (24 titik).

Perhitungan struktur final oleh ahli teknik sipil bersertifikat.

## DENAH PONDASI & SLOOF SKALA 1 : 100

Tampak atas — garis putus = pondasi batu kali menerus; kotak X = footplat F1; as 1-6 / A-C

PROYEK

# RUMAH MAKAN "SELERA NUSANTARA"

Perencanaan Bangunan Rumah Makan 1 Lantai
Kapasitas ± 66 Kursi

LOKASI

(diisi sesuai lahan terpilih)

PEMILIK

(diisi nama pemilik)

**KETERANGAN / CATATAN**

Satuan ukuran: cm, kecuali ditulis lain. Elevasi dalam meter. ±0.00 = lantai ruang makan.

Ukuran denah as ke as dinding, kecuali dinyatakan lain.

Gambar adalah rencana awal; ukuran lapangan wajib dicek sebelum pelaksanaan.

Pondasi ditunjukkan dengan garis putus-putus (di bawah tanah).

**REVISI**


| No | Tanggal | Keterangan |
|---|---|---|
| 0 | 26-10-2026 | Gambar rencana (usulan awal) |
| | | |

| | |
|---|---|
| Digambar | Drafter (Claude) |
| Diperiksa | _____ |
| Disetujui | _____ |
| Tanggal | 26 Oktober 2026 |


JUDUL GAMBAR

**DENAH PONDASI & SLOOF**

| NO. GAMBAR | SKALA | LEMBAR |
|---|---|---|
| **A-04** | **1 : 100** | **5/11** |

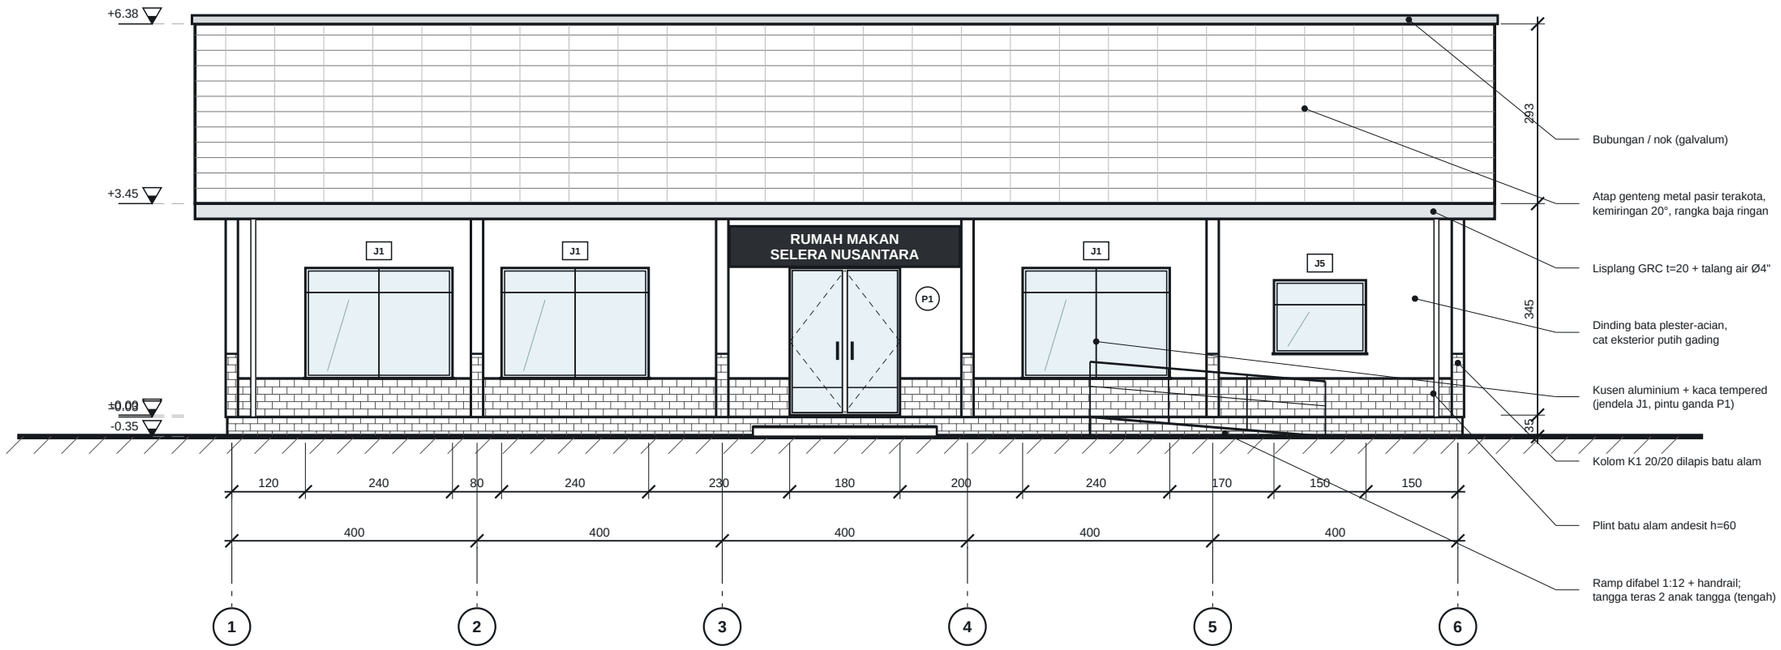


## TAMPAK DEPAN (SELATAN) SKALA 1 : 100

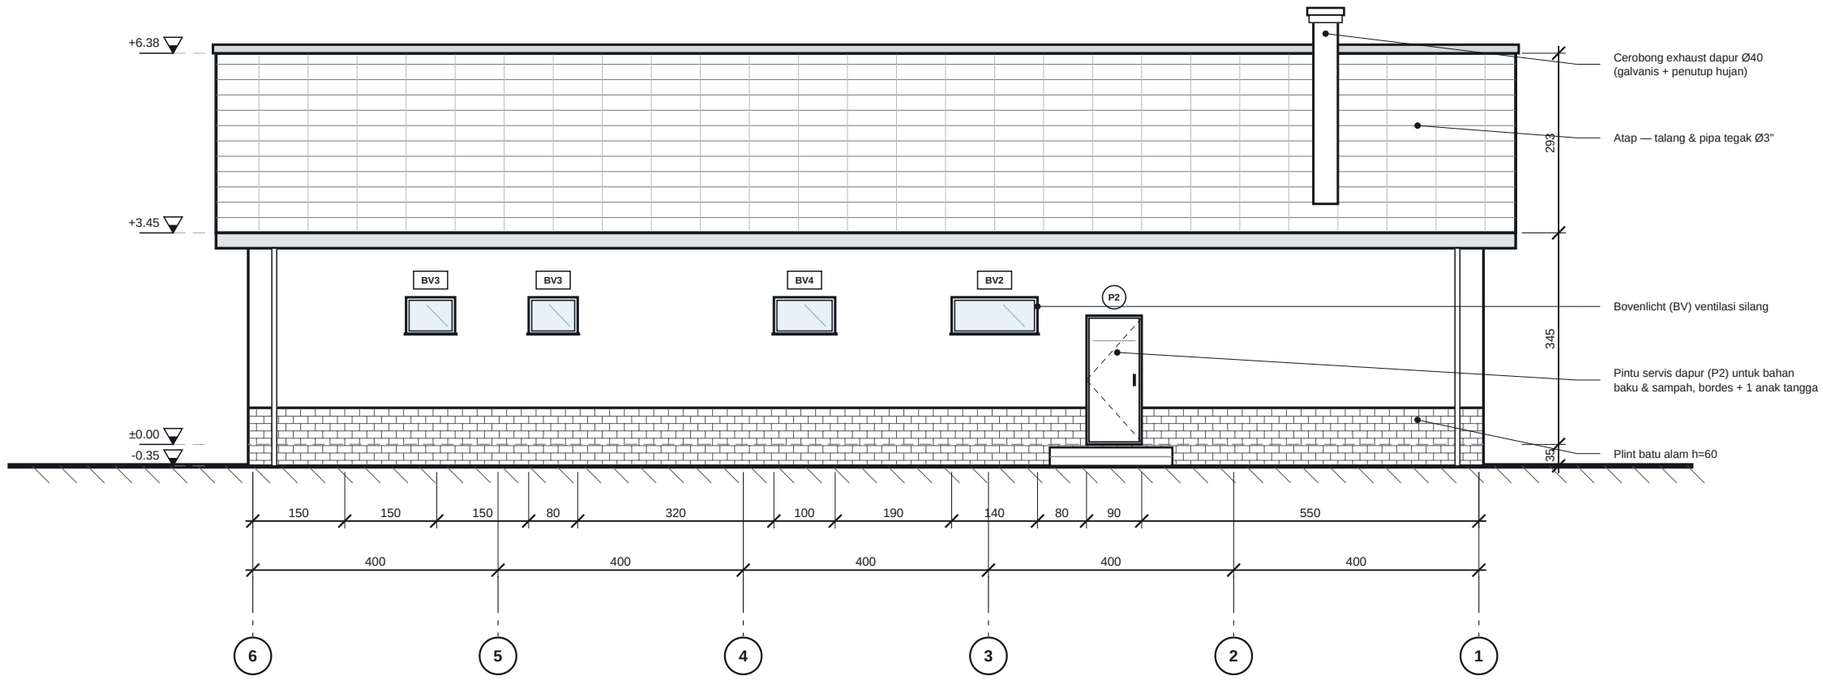


## TAMPAK BELAKANG (UTARA) SKALA 1 : 100

PROYEK

# RUMAH MAKAN "SELERA NUSANTARA"

Perencanaan Bangunan Rumah Makan 1 Lantai
Kapasitas ± 66 Kursi

LOKASI

(diisi sesuai lahan terpilih)

PEMILIK

(diisi nama pemilik)

**KETERANGAN / CATATAN**

Satuan ukuran: cm, kecuali ditulis lain. Elevasi dalam meter. ±0.00 = lantai ruang makan.

Ukuran denah as ke as dinding, kecuali dinyatakan lain.

Gambar adalah rencana awal; ukuran lapangan wajib dicek sebelum pelaksanaan.

Warna finishing: dinding putih gading, plint & kolom batu alam, kusen aluminium hitam doff.

Elevasi tanah rata-rata -0.35; sesuaikan kondisi lahan.

**REVISI**


| No | Tanggal | Keterangan |
|---|---|---|
| 0 | 26-10-2026 | Gambar rencana (usulan awal) |
| | | |

| | |
|---|---|
| Digambar | Drafter (Claude) |
| Diperiksa | _____ |
| Disetujui | _____ |
| Tanggal | 26 Oktober 2026 |


JUDUL GAMBAR

## TAMPAK DEPAN & TAMPAK BELAKANG


| NO. GAMBAR | SKALA | LEMBAR |
|---|---|---|
| A-05 | 1 : 100 | 6/11 |

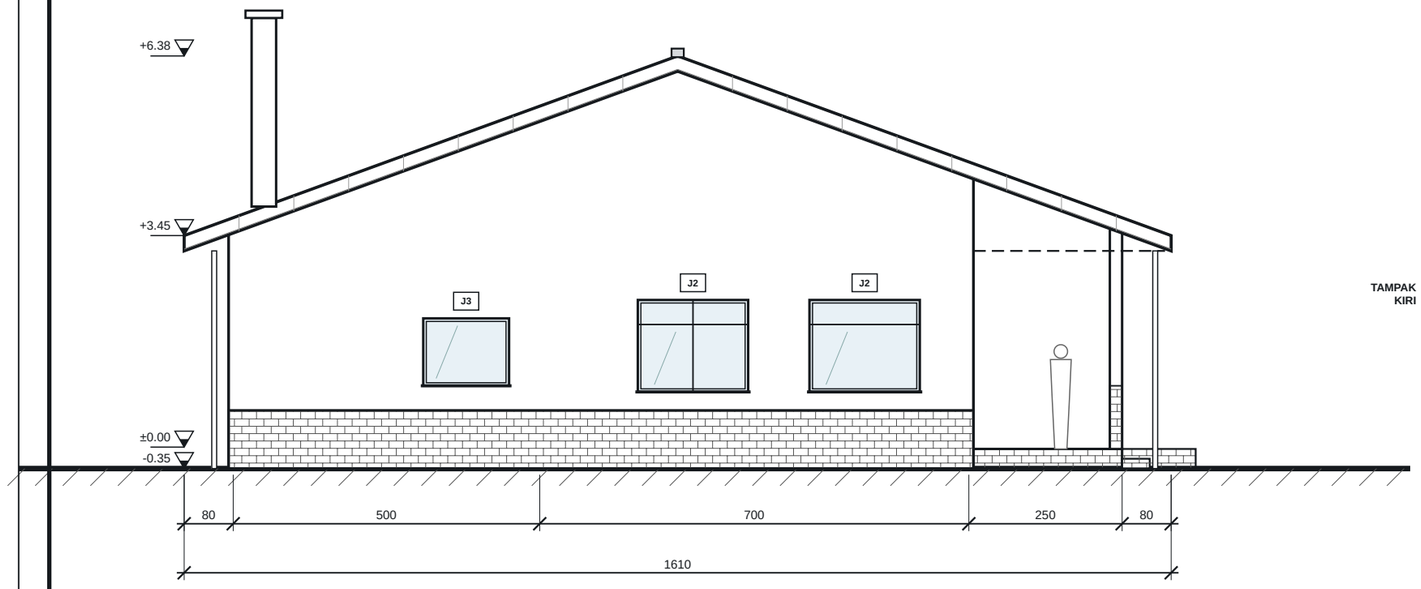


**TAMPAK KIRI (BARAT)** SKALA 1 : 100

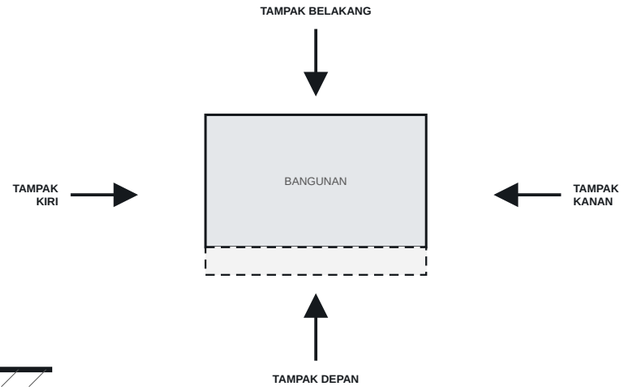


**DENAH KUNCI ARAH TAMPAK**

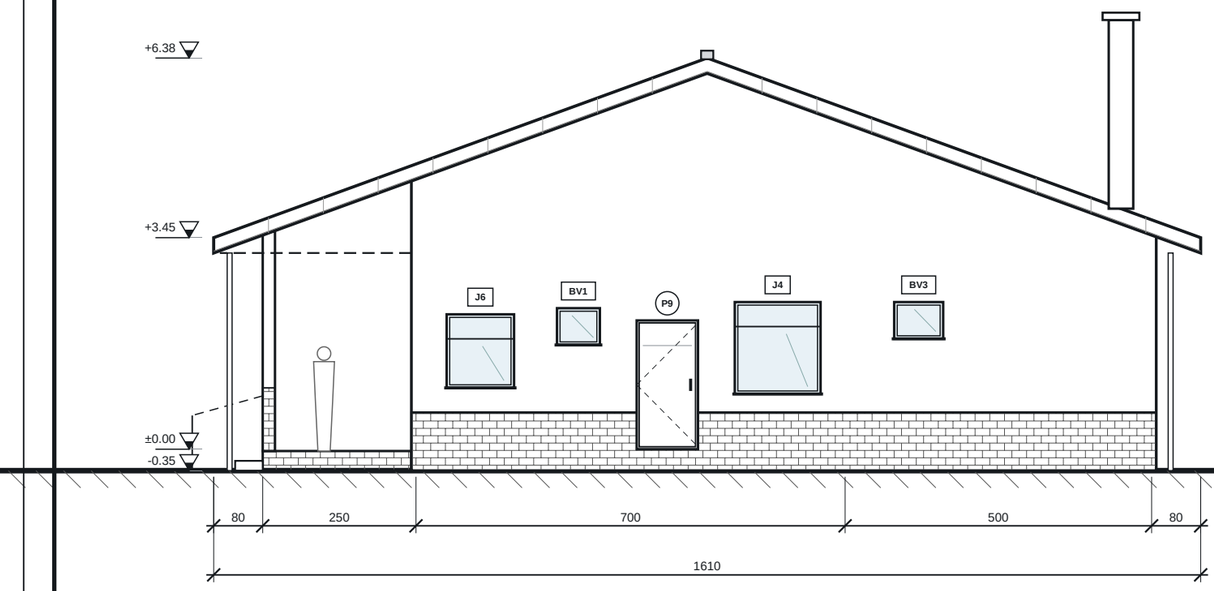


**TAMPAK KANAN (TIMUR)** SKALA 1 : 100

**KETERANGAN MATERIAL**

- Atap: genteng metal pasir 0.4 mm, warna terakota
- Rangka atap: baja ringan C75 + reng, kemiringan 20°
- Dinding: bata merah ½ bata, plester 1:4, acian
- Plint: batu alam andesit h=60 cm
- Kolom teras: K1 20/20 dilapis batu alam
- Kusen: aluminium 4" hitam doff + kaca tempered
- Lisplang: GRC 20 cm, cat putih
- Talang: PVC/galvalum Ø4", pipa tegak Ø3"
- Plafon: gypsum 9 mm (dalam), PVC (teras/WC)
- Jendela atas/ventilasi (BV): kaca nako / louvre
- Lantai teras: keramik 40×40 anti-slip
- Cerobong dapur: pipa galvanis Ø40 + topi hujan

PROYEK

# RUMAH MAKAN "SELERA NUSANTARA"

Perencanaan Bangunan Rumah Makan 1 Lantai
Kapasitas ± 66 Kursi

LOKASI

(diisi sesuai lahan terpilih)

PEMILIK

(diisi nama pemilik)

**KETERANGAN / CATATAN**

Satuan ukuran: cm, kecuali ditulis lain.
Elevasi dalam meter. ±0.00 = lantai ruang makan.

Ukuran denah as ke as dinding, kecuali dinyatakan lain.

Gambar adalah rencana awal; ukuran lapangan wajib dicek sebelum pelaksanaan.

**REVISI**


| No | Tanggal | Keterangan |
|---|---|---|
| 0 | 26-10-2026 | Gambar rencana (usulan awal) |
| | | |

| | |
|---|---|
| Digambar | Drafter (Claude) |
| Diperiksa | _____ |
| Disetujui | _____ |
| Tanggal | 26 Oktober 2026 |

JUDUL GAMBAR


## TAMPAK KIRI & TAMPAK KANAN

| NO. GAMBAR | SKALA | LEMBAR |
|---|---|---|
| A-06 | 1 : 100 | 7/11 |

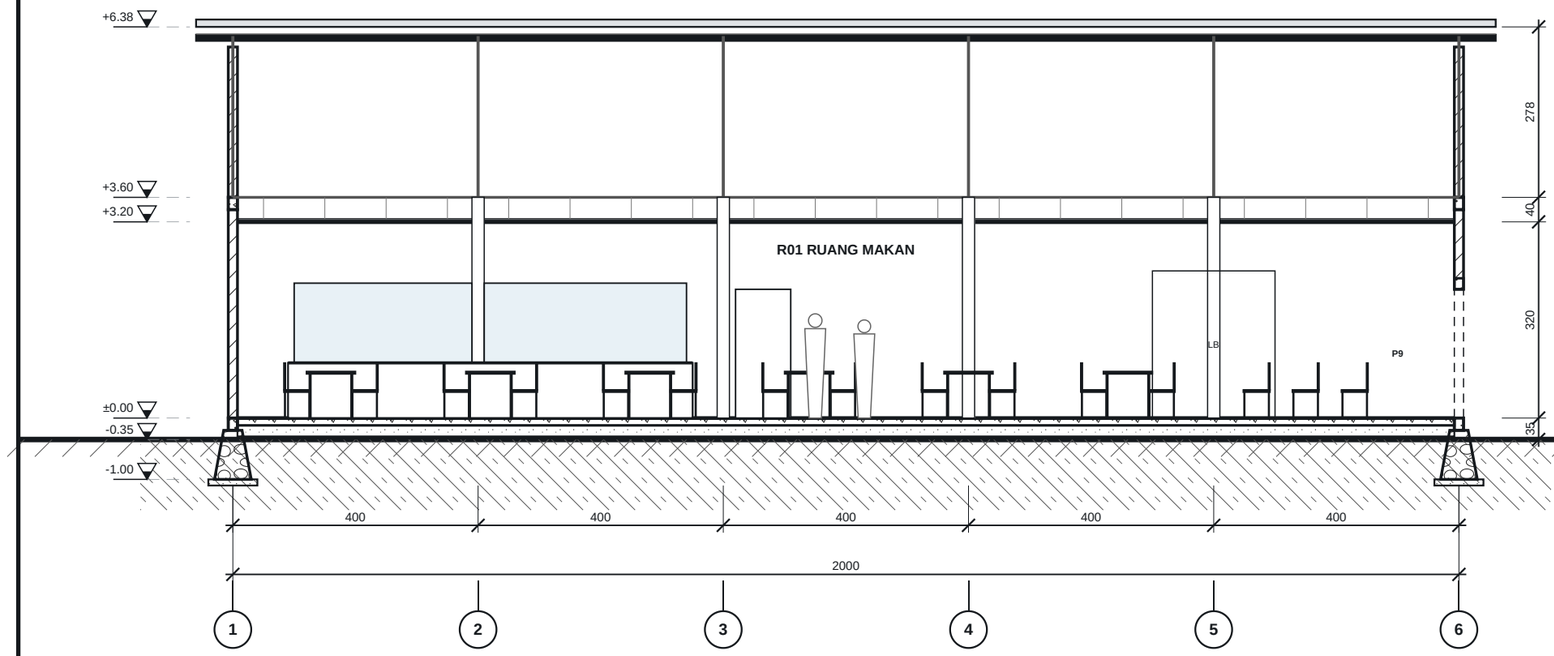


## POTONGAN I-I (MEMANJANG) SKALA 1 : 100

Dilihat ke arah utara, bidang potong pada y = +7,60 (lihat denah A-02)

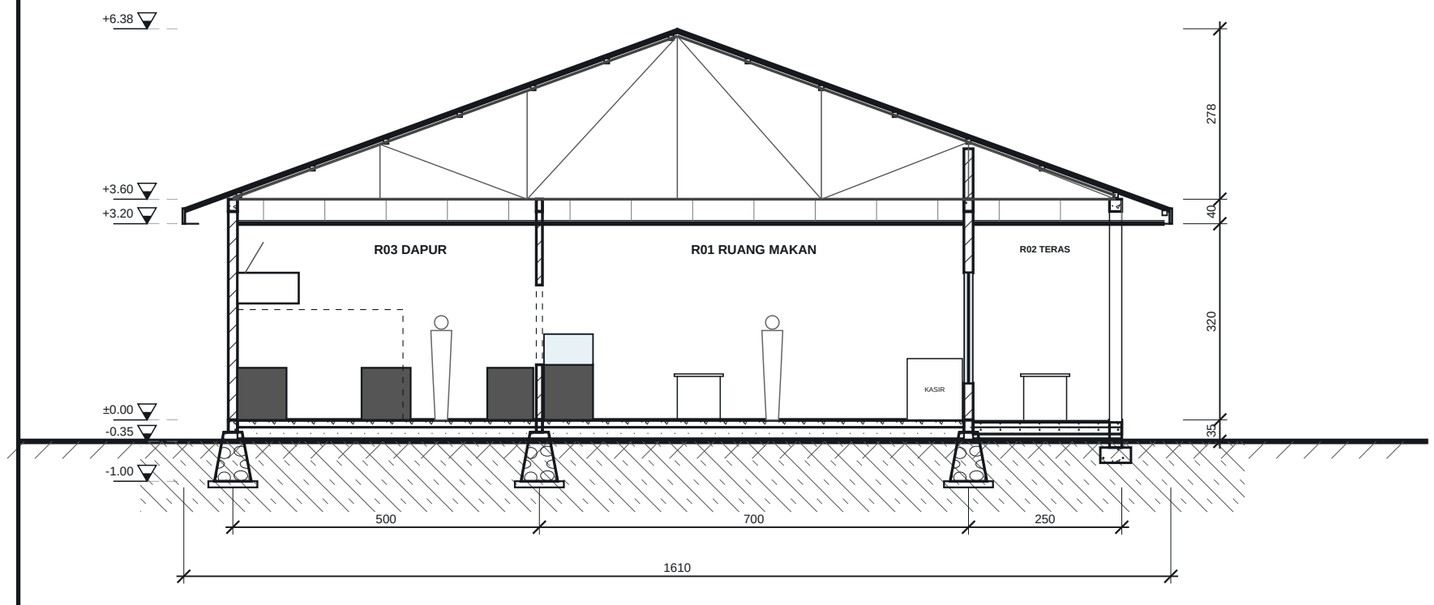


## POTONGAN II-II (MELINTANG) SKALA 1 : 100

Dilihat ke arah timur, bidang potong pada x = +5,00 melalui dapur, counter saji dan teras

**LEGENDA POTONGAN**

- Beton bertulang (kolom, sloof, ring balk, plat)
- Pasangan bata merah (dinding)
- Pondasi batu kali 1:5 (pc:ps)
- Pasir urug / lantai kerja t=5-10
- Tanah asli / urugan padat
- Kaca tempered / kusen aluminium

**KETERANGAN STRUKTUR & FINISHING**

Pondasi: batu kali menerus lebar atas 30, bawah 60, dalam 80 cm dari tanah.

Sloof SL 15/20 (4Ø10, Ø6-150).

Kolom K1 20/20 (4Ø12, Ø6-150).

Ring balk RB 15/20 (4Ø10, Ø6-150).

Lantai: urug pasir 10 + lantai kerja 5 + spesi 3 + keramik/granit tile.

Atap: kuda-kuda baja ringan, jarak 4,00, penutup genteng metal pasir.

Plafon: rangka hollow 4×4, gypsum 9 mm, tinggi +3,20 dari lantai.

Ventilasi atap: lubang angin di lisplang + nok ventilasi.

PROYEK

# RUMAH MAKAN "SELERA NUSANTARA"

Perencanaan Bangunan Rumah Makan 1 Lantai
Kapasitas ± 66 Kursi

LOKASI

(diisi sesuai lahan terpilih)

PEMILIK

(diisi nama pemilik)

**KETERANGAN / CATATAN**

Satuan ukuran: cm, kecuali ditulis lain. Elevasi dalam meter. ±0.00 = lantai ruang makan.

Ukuran denah as ke as dinding, kecuali dinyatakan lain.

Gambar adalah rencana awal; ukuran lapangan wajib dicek sebelum pelaksanaan.

Struktur indikatif — dimensi final mengikuti perhitungan insinyur sipil/struktur.

**REVISI**


| No | Tanggal | Keterangan |
|---|---|---|
| 0 | 26-10-2026 | Gambar rencana (usulan awal) |
| | | |

| | |
|---|---|
| Digambar | Drafter (Claude) |
| Diperiksa | _____ |
| Disetujui | _____ |
| Tanggal | 26 Oktober 2026 |

JUDUL GAMBAR

## POTONGAN I-I & POTONGAN II-II

| NO. GAMBAR | SKALA | LEMBAR |
|---|---|---|
| A-07 | 1 : 100 | 8/11 |

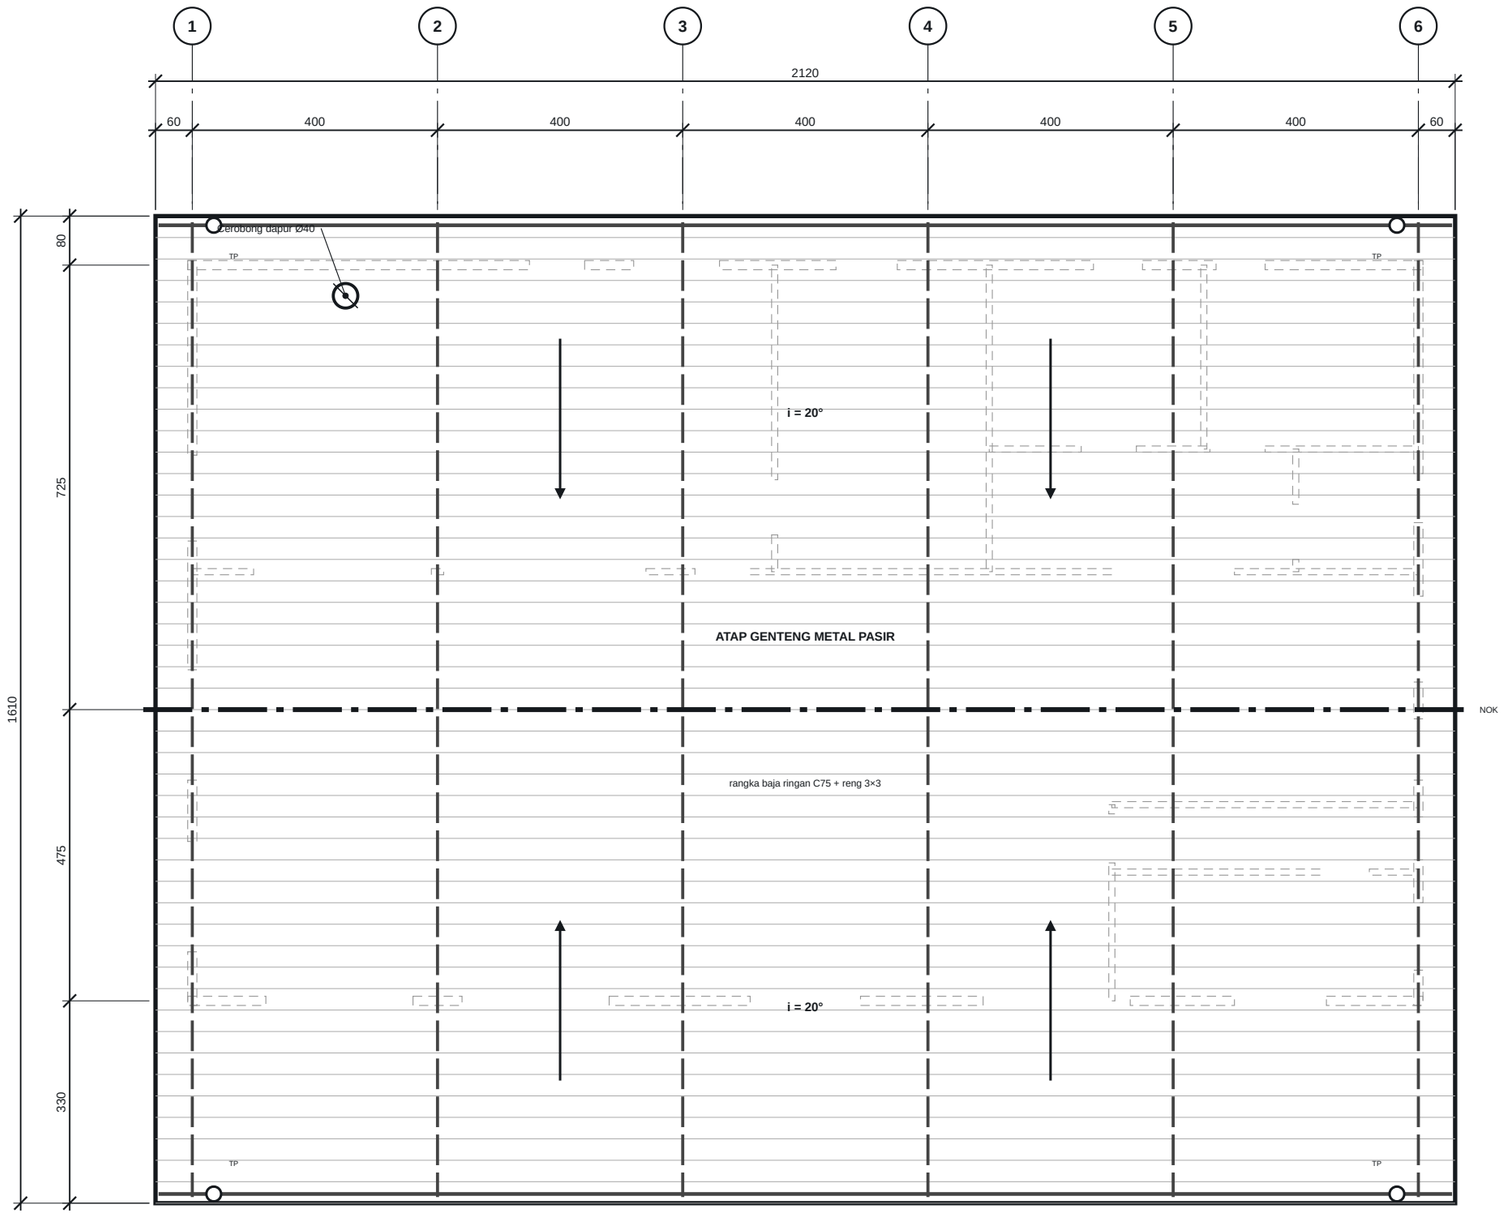


## KETERANGAN ATAP

- Penutup: genteng metal pasir t=0,4
- Rangka: baja ringan C75 / reng TS 3×3
- Jarak kuda-kuda: 4,00 m (as 1–6)
- Gording: C75 ±1,20 m searah lereng
- Kemiringan: 20° (36%)
- Tepi atap: 80 cm (belakang), 80 cm
- (depan, di luar teras), 60 cm (samping)
- Talang: PVC Ø4" kemiringan 1:200
- Pipa tegak (TP): Ø3" × 4 titik
- Lisplang: GRC 20 cm
- Nok: galvalum + ventilasi nok
- Cerobong: Ø40 galvanis, tinggi +7,00
- (≥ 1,0 m di atas nok)

## LEGENDA

- Nok / bubungan
- Kuda-kuda (rangka)
- Talang air
- Dinding di bawah atap

## RENCANA ATAP SKALA 1 : 100

Atap pelana (gable) ± 20°, bubungan memanjang timur–barat pada y = +7,25; menutup bangunan & teras

PROYEK

# RUMAH MAKAN "SELERA NUSANTARA"

Perencanaan Bangunan Rumah Makan 1 Lantai
Kapasitas ± 66 Kursi

LOKASI

(diisi sesuai lahan terpilih)

PEMILIK

(diisi nama pemilik)

**KETERANGAN / CATATAN**

Satuan ukuran: cm, kecuali ditulis lain.
Elevasi dalam meter. ±0.00 = lantai ruang makan.

Ukuran denah as ke as dinding, kecuali dinyatakan lain.

Gambar adalah rencana awal; ukuran lapangan wajib dicek sebelum pelaksanaan.

**REVISI**


| No | Tanggal | Keterangan |
|---|---|---|
| 0 | 26-10-2026 | Gambar rencana (usulan awal) |
| | | |

| | |
|---|---|
| Digambar | Drafter (Claude) |
| Diperiksa | _____ |
| Disetujui | _____ |
| Tanggal | 26 Oktober 2026 |


JUDUL GAMBAR

**RENCANA ATAP**

| NO. GAMBAR | SKALA | LEMBAR |
|---|---|---|
| A-08 | 1 : 100 | 9/11 |

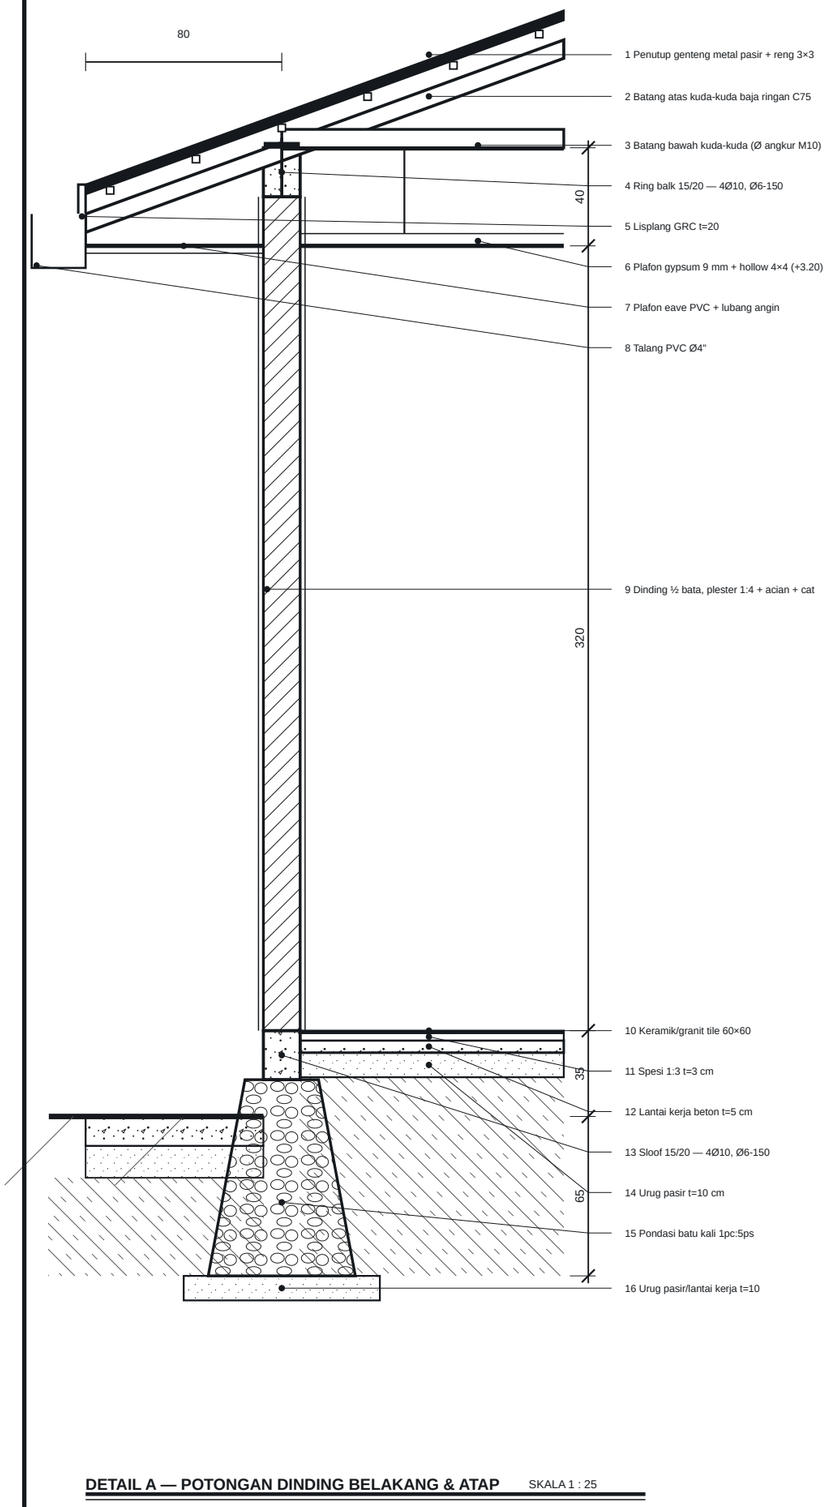



**DETAIL A — POTONGAN DINDING BELAKANG & ATAP** SKALA 1 : 25

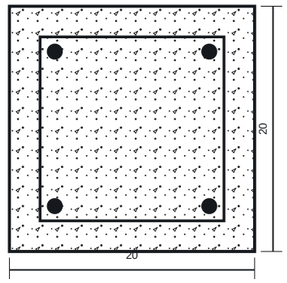



**K1 20/20**

4Ø12 · sengkang Ø6-150

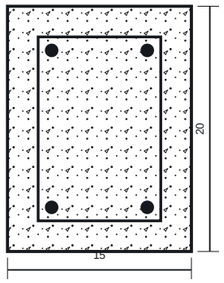


**SL / RB / SL2 15/20**

4Ø10 · Ø6-150

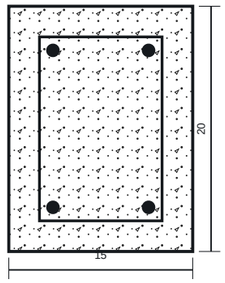


**LINTEL 15/20**

4Ø10 · Ø6-150


**DETAIL B — PENAMPANG BETON BERTULANG** SKALA 1 : 5

Selimut beton 25 mm; sambungan tulangan ≥ 40d; kait sengkang 135°.

2 anak tangga: tinggi 16 cm,


lebar injakan 45 cm, lebar 3,00 m,

keramik 40×40 anti-slip.

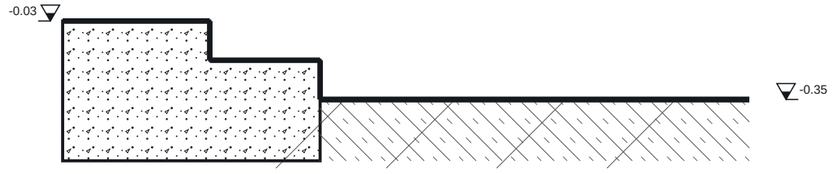


**DETAIL C — TANGGA TERAS** SKALA 1 : 25

RAMP 1:12 — lebar 1,20 m, bordes datar 1,20 m, handrail ganda 0,90 / 0,70

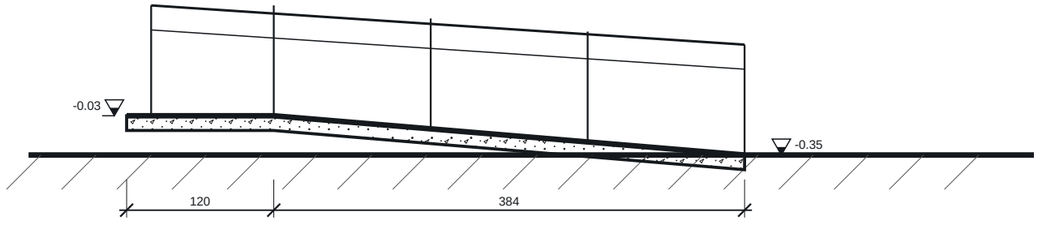


**DETAIL D — RAMP DIFABEL** SKALA 1 : 50

PROYEK

# RUMAH MAKAN "SELERA NUSANTARA"

Perencanaan Bangunan Rumah Makan 1 Lantai
Kapasitas ± 66 Kursi

LOKASI

(diisi sesuai lahan terpilih)

PEMILIK

(diisi nama pemilik)

**KETERANGAN / CATATAN**

Satuan ukuran: cm, kecuali ditulis lain. Elevasi dalam meter. ±0.00 = lantai ruang makan.

Ukuran denah as ke as dinding, kecuali dinyatakan lain.

Gambar adalah rencana awal; ukuran lapangan wajib dicek sebelum pelaksanaan.

Detail indikatif sesuai praktik umum; dimensi & tulangan final mengikuti hitungan struktur.

**REVISI**

| No | Tanggal | Keterangan |
|---|---|---|
| 0 | 26-10-2026 | Gambar rencana (usulan awal) |
| | | |

| | |
|---|---|
| Digambar | Drafter (Claude) |
| Diperiksa | _____ |
| Disetujui | _____ |
| Tanggal | 26 Oktober 2026 |

JUDUL GAMBAR

## DETAIL KONSTRUKSI

| NO. GAMBAR | SKALA | LEMBAR |
|---|---|---|
| A-09 | 1:25 / 1:5 | 10/11 |

## JADWAL PINTU & JENDELA

| Kode | Lebar×Tinggi (cm) | Ambang (cm) | Jml | Bahan / jenis | Lokasi / keterangan |
|---|---|---|---|---|---|
| P1 | 180×240 | 0 | 1 | Pintu ganda kaca tempered 10 mm, kusen aluminium | Pintu utama (swing keluar), handle stainless |
| P2 | 90×210 | 0 | 1 | Pintu plat besi / panel fiber + kusen besi | Servis dapur (swing keluar), kunci ganda |
| P3 | 90×210 | 0 | 1 | Pintu panel kayu/HPL, swing dua arah + kaca | Dapur ↔ ruang makan (jalur pelayan) |
| P4 | 90×210 | 0 | 1 | Pintu panel PVC/ aluminium | Dapur ↔ gudang |
| P5 | 90×210 | 0 | 2 | Pintu PVC/ ABS anti-air | WC pria & wanita (swing ke dalam) |
| P6 | 90×210 | 0 | 1 | Pintu aluminium anti-air, lebar bersih 80 | WC difabel (swing keluar), handle tuas |
| P8 | 80×210 | 0 | 2 | Pintu panel PVC / kayu | Wudhu & musala |
| P9 | 100×210 | 0 | 1 | Pintu baja + panic bar | Pintu darurat, swing keluar |
| J1 | 240×180 | 60 | 3 | Jendela kaca tempered 8 mm + bovenlicht, alumunium | Ruang makan (fix + engsel) |
| J2 | 180×150 | 90 | 2 | Jendela aluminium + kaca bening 5 mm | Ruang makan samping barat |
| J3 | 140×110 | 100 | 1 | Jendela aluminium + kaca bening 5 mm | Dapur — atas bak cuci piring |
| J4 | 140×150 | 90 | 1 | Jendela aluminium + kaca bening 5 mm | Ruang makan samping timur |
| J5 | 150×120 | 100 | 1 | Jendela aluminium + kaca bening 5 mm | Musala |
| J6 | 110×120 | 100 | 1 | Jendela aluminium + kaca bening 5 mm | Musala (timur) |
| BV1 | 70×60 | 170 | 1 | Bovenlicht aluminium + kaca nako | Tempat wudhu |
| BV2 | 140×60 | 180 | 1 | Bovenlicht aluminium + kaca nako | Dapur (ventilasi silang) |
| BV3 | 80×60 | 180 | 3 | Bovenlicht aluminium + kaca nako | WC pria, wanita, difabel |
| BV4 | 100×60 | 180 | 1 | Louvre aluminium | Gudang |
| JL1 | 290×130 | 90 | 1 | Jendela layan geser kaca 5 mm | Counter saji dapur ↔ etalase |
| JL2 | 330×130 | 90 | 1 | Jendela layan geser kaca 5 mm | Counter saji dapur ↔ etalase |
| LB | 200×240 | 0 | 1 | Bukaan tanpa daun (ambang beton) | Lobi WC ↔ ruang makan |

Ambang = tinggi bawah bukaan dari lantai. Kode tampak pada denah A-02 dan tampak A-05/A-06. BV = bovenlicht, JL = jendela layan.

## JADWAL FINISHING RUANG

| Kode | Ruang | Luas m² | Lantai | Dinding | Plafon | Level |
|---|---|---|---|---|---|---|
| R01 | Ruang Makan | 120.7 | Granit tile 60×60 doff | Cat emulsi + wainscot HPL h=90 | Gypsum 9mm, h=3.20 | ±0.00 |
| R02 | Teras / Makan Luar | 48.9 | Keramik 40×40 anti-slip | Cat tekstur + batu alam | Plafon PVC / kalsiboard | -0.03 |
| R03 | Dapur | 45.7 | Keramik 30×30 anti-slip | Keramik 20×25 h=2.10 | Kalsiboard 6mm, h=3.20 | ±0.00 |
| R04 | Gudang Kering | 16.6 | Plester + acian, floor hardener | Cat tembok | Kalsiboard 6mm, h=3.20 | ±0.00 |
| R05 | WC Pria | 9.8 | Keramik 30×30 anti-slip | Keramik 20×25 h=2.10 | PVC panel, h=3.00 | -0.05 |
| R06 | WC Wanita | 9.7 | Keramik 30×30 anti-slip | Keramik 20×25 h=2.10 | PVC panel, h=3.00 | -0.05 |
| R07 | Lobi / Wastafel | 9.3 | Granit tile 60×60 doff | Cat emulsi + keramik h=1.20 | Gypsum 9mm, h=3.00 | ±0.00 |
| R08 | WC Difabel | 3.6 | Keramik 30×30 anti-slip | Keramik 20×25 h=2.10 | PVC panel, h=3.00 | -0.05 |
| R09 | Tempat Wudhu | 4.9 | Keramik 30×30 anti-slip | Keramik 20×25 h=2.10 | PVC panel, h=3.00 | -0.05 |
| R10 | Musala | 9.6 | Karpet / granit 60×60 | Cat emulsi | Gypsum 9mm, h=3.00 | ±0.00 |

## DAFTAR PERALATAN DAPUR & FURNITUR (INDIKATIF)

| No | Peralatan / furnitur | Jml | Ukuran / keterangan |
|---|---|---|---|
| 1 | Kompor gas 4 tungku + hood + exhaust fan | 1 set | 4,5 × 0,8 m; cerobong Ø40 |
| 2 | Meja persiapan stainless | 1 | 3,5 × 0,8 m |
| 3 | Bak cuci piring 2 bak + grease trap | 1 | 0,65 × 1,85 m |
| 4 | Kulkas 2 pintu / freezer | 2 | 0,7 × 0,8 m |
| 5 | Meja saji / plating + rak piring | 2 | 5,0 × 0,75 m; 1,9 × 0,75 m |
| 6 | Etalase counter saji kaca | 1 | 6,6 × 0,8 m, h=0,90 |
| 7 | Meja makan 4 kursi (dalam + teras) | 15 | 0,8 × 0,8 m + 4 kursi |
| 8 | Meja panjang 6 kursi | 1 | 2,4 × 0,8 m |
| 9 | Kasir + display minuman | 1 set | 1,8 × 0,9 m; 1,1 × 0,85 m |

## REKAPITULASI

| Uraian | Nilai |
|---|---|
| Luas bangunan (as-as) | 244.8 m² |
| Luas teras | 48.9 m² |
| Luas total beratap | 293.7 m² |
| Luas ruang makan | 120.7 m² |
| Luas dapur + gudang | 62.3 m² |
| Kursi dalam / teras | 42 / 24 |
| Total kursi | 66 |
| Kloset / urinoir | 4 / 2 |
| Wastafel (lobi+difabel) | 3 |
| Kran wudhu | 4 |
| Parkir mobil / motor | 8 / 12 |

### ASUMSI & CATATAN PERENCANAAN

• Gambar rencana awal (DED belum), konsep 1 lantai.

• Lahan datar 28×33 m, muka ke selatan.

• Struktur: beton bertulang + atap baja ringan.

• Jumlah toilet & parkir mengikuti praktik umum; verifikasi dengan peraturan daerah setempat.

• Gambar MEP (listrik, plumbing, AC, hood) dibuat terpisah setelah menu & peralatan final.

• Kebutuhan dapur: 8–10 m²/100 kursi tercapai (dapur+gudang ≈ 62 m²).

• Akses difabel: ramp 1:12, WC difabel, parkir khusus.

PROYEK

**RUMAH MAKAN "SELERA NUSANTARA"**

Perencanaan Bangunan Rumah Makan 1 Lantai
Kapasitas ± 66 Kursi

LOKASI

(diisi sesuai lahan terpilih)

PEMILIK

(diisi nama pemilik)

**KETERANGAN / CATATAN**

Satuan ukuran: cm, kecuali ditulis lain. Elevasi dalam meter. ±0.00 = lantai ruang makan.

Ukuran denah as ke as dinding, kecuali dinyatakan lain.

Gambar adalah rencana awal; ukuran lapangan wajib dicek sebelum pelaksanaan.

**REVISI**

| No | Tanggal | Keterangan |
|---|---|---|
| 0 | 26-10-2026 | Gambar rencana (usulan awal) |
| | | |

| | |
|---|---|
| Digambar | Drafter (Claude) |
| Diperiksa | _____ |
| Disetujui | _____ |
| Tanggal | 26 Oktober 2026 |

JUDUL GAMBAR

**JADWAL PINTU, JENDELA & FINISHING**

| NO. GAMBAR | SKALA | LEMBAR |
|---|---|---|
| A-10 | — | 11/11 |