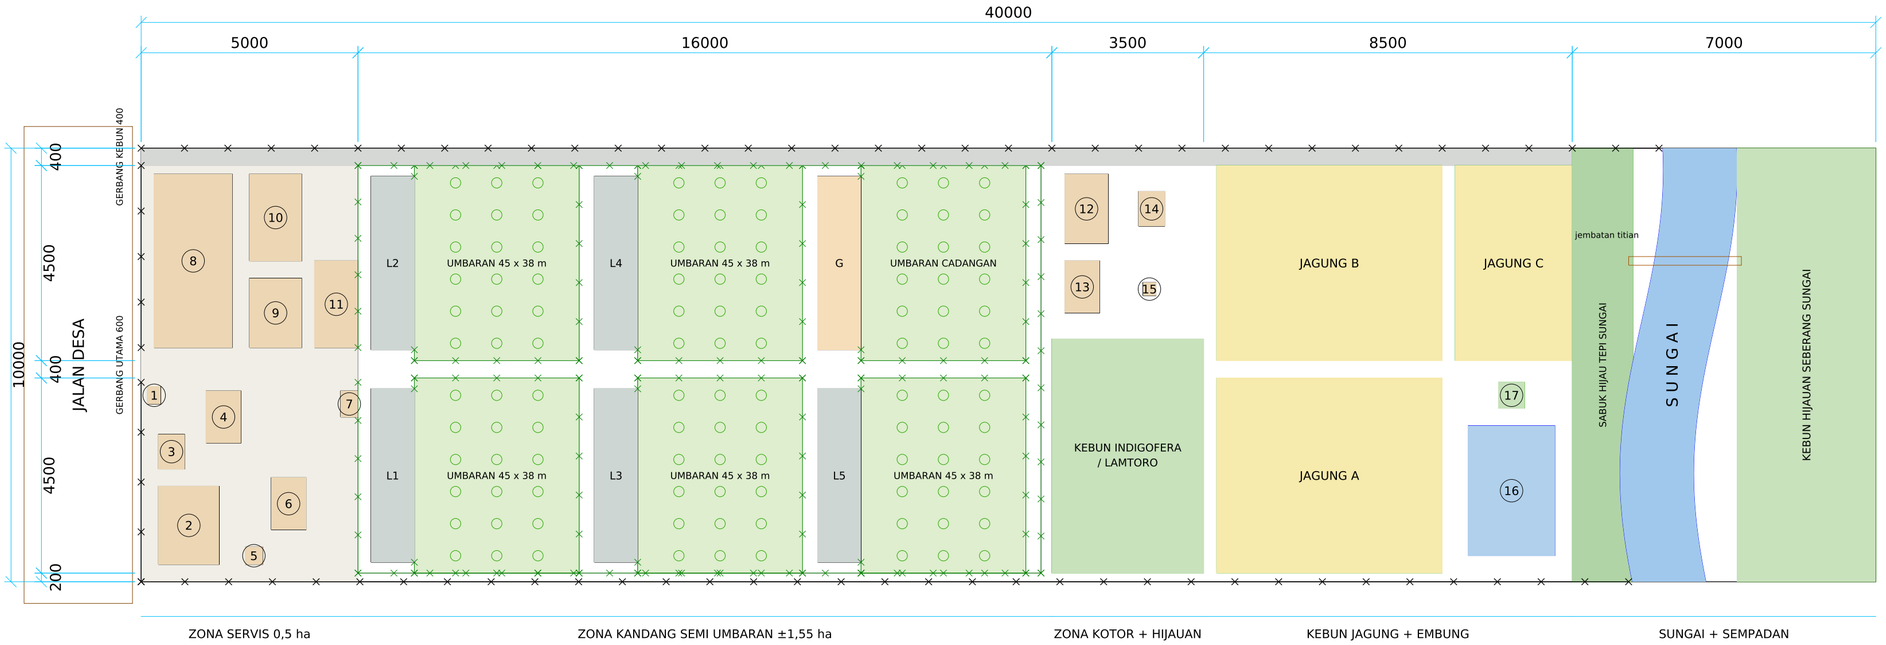


U

arah utara diasumsikan

ke jalan - mohon dicek

KETERANGAN BANGUNAN

1. Pos jaga
2. Parkir tamu & pembeli
3. Kantor
4. Rumah telur (sortir & simpan)
5. Sumur bor + menara tandon
6. Mes anak kandang
7. Ruang ganti + celup kaki
8. Lantai jemur jagung
9. Rumah pakan (olah & campur)
10. Gudang jagung
11. Gudang pakan jadi
12. Rumah kompos
13. Rumah maggot BSF
14. Kandang karantina
15. Insinerator
16. Embung 30 x 20 m
17. Rumah pompa air sungai

KONSEP TAPAK

1. Urutan dari jalan ke sungai: zona servis (bersih untuk tamu) - zona kandang (paling bersih, berpagar) - zona kotor - kebun - sungai.
2. Tamu, pembeli telur, dan truk pakan berhenti di zona servis; tidak masuk zona kandang.
3. Jalan servis 4 m di sisi timur menuju zona kotor dan kebun tanpa melewati zona kandang.
4. Kotoran dan bangkai keluar lewat gerbang belakang zona kandang ke zona kotor (kompos, maggot, insinerator).
5. Kandang dan kompos berjarak lebih dari 100 m dari sungai; air minum ayam dari sumur bor, air sungai untuk irigasi.
6. Tepi sungai dibiarkan hijau (bambu, lamtoro, rumput) untuk mencegah longsor dan pencemaran; ikuti ketentuan sempadan setempat.
7. Bentuk dan posisi sungai mengikuti sketsa pemilik; ukur ulang di lapangan sebelum pematokan.

PROYEK
PETERNAKAN AYAM KUB PETELUR SEMI UMBARAN 10.000 EKOR
ADEVA FARM - KAB. KONAWE SELATAN, SULAWESI TENGGARA

KERTAS A2

JUDUL GAMBAR
RENCANA TAPAK LAHAN 4 HA (100 X 400 M)

CATATAN
Satuan cm, elevasi terhadap lantai (±0).
Periksa ulang oleh ahli sipil.

SKALA
1 : 1000

TANGGAL
OKTOBER 2026


STATUS
GAMBAR PERENCANAAN

NO. GAMBAR
S-01



CATATAN
- Semua bangunan servis: struktur kolom beton 15/15, dinding bata, atap baja ringan + galvalum (lihat GT-03 dan GT-04).
- Pagar zona kandang kawat harmonika 2" tinggi 180 cm + 30 cm ditanam, tiang beton pracetak 10/10 @250 (lihat P-01).
- Pagar sekat umbaran sama dengan pagar zona kandang, pintu umbaran 100 cm di sisi jalan gerobak.
- Ukuran dalam meter pada gambar ini (dimensi otomatis ditampilkan dalam cm).

PROYEK PETERNAKAN AYAM KUB PETELUR SEMI UMBARAN 10.000 EKOR ADEVA FARM - KAB. KONAWE SELATAN, SULAWESI TENGGARA			KERTAS A2
JUDUL GAMBAR TATA LETAK ZONA SERVIS, ZONA KANDANG DAN ZONA KOTOR			
CATATAN Satuan cm, elevasi terhadap lantai (±0). Periksa ulang oleh ahli sipil.		SKALA 1 : 500	
TANGGAL OKTOBER 2026	STATUS GAMBAR PERENCANAAN		NO. GAMBAR S-02

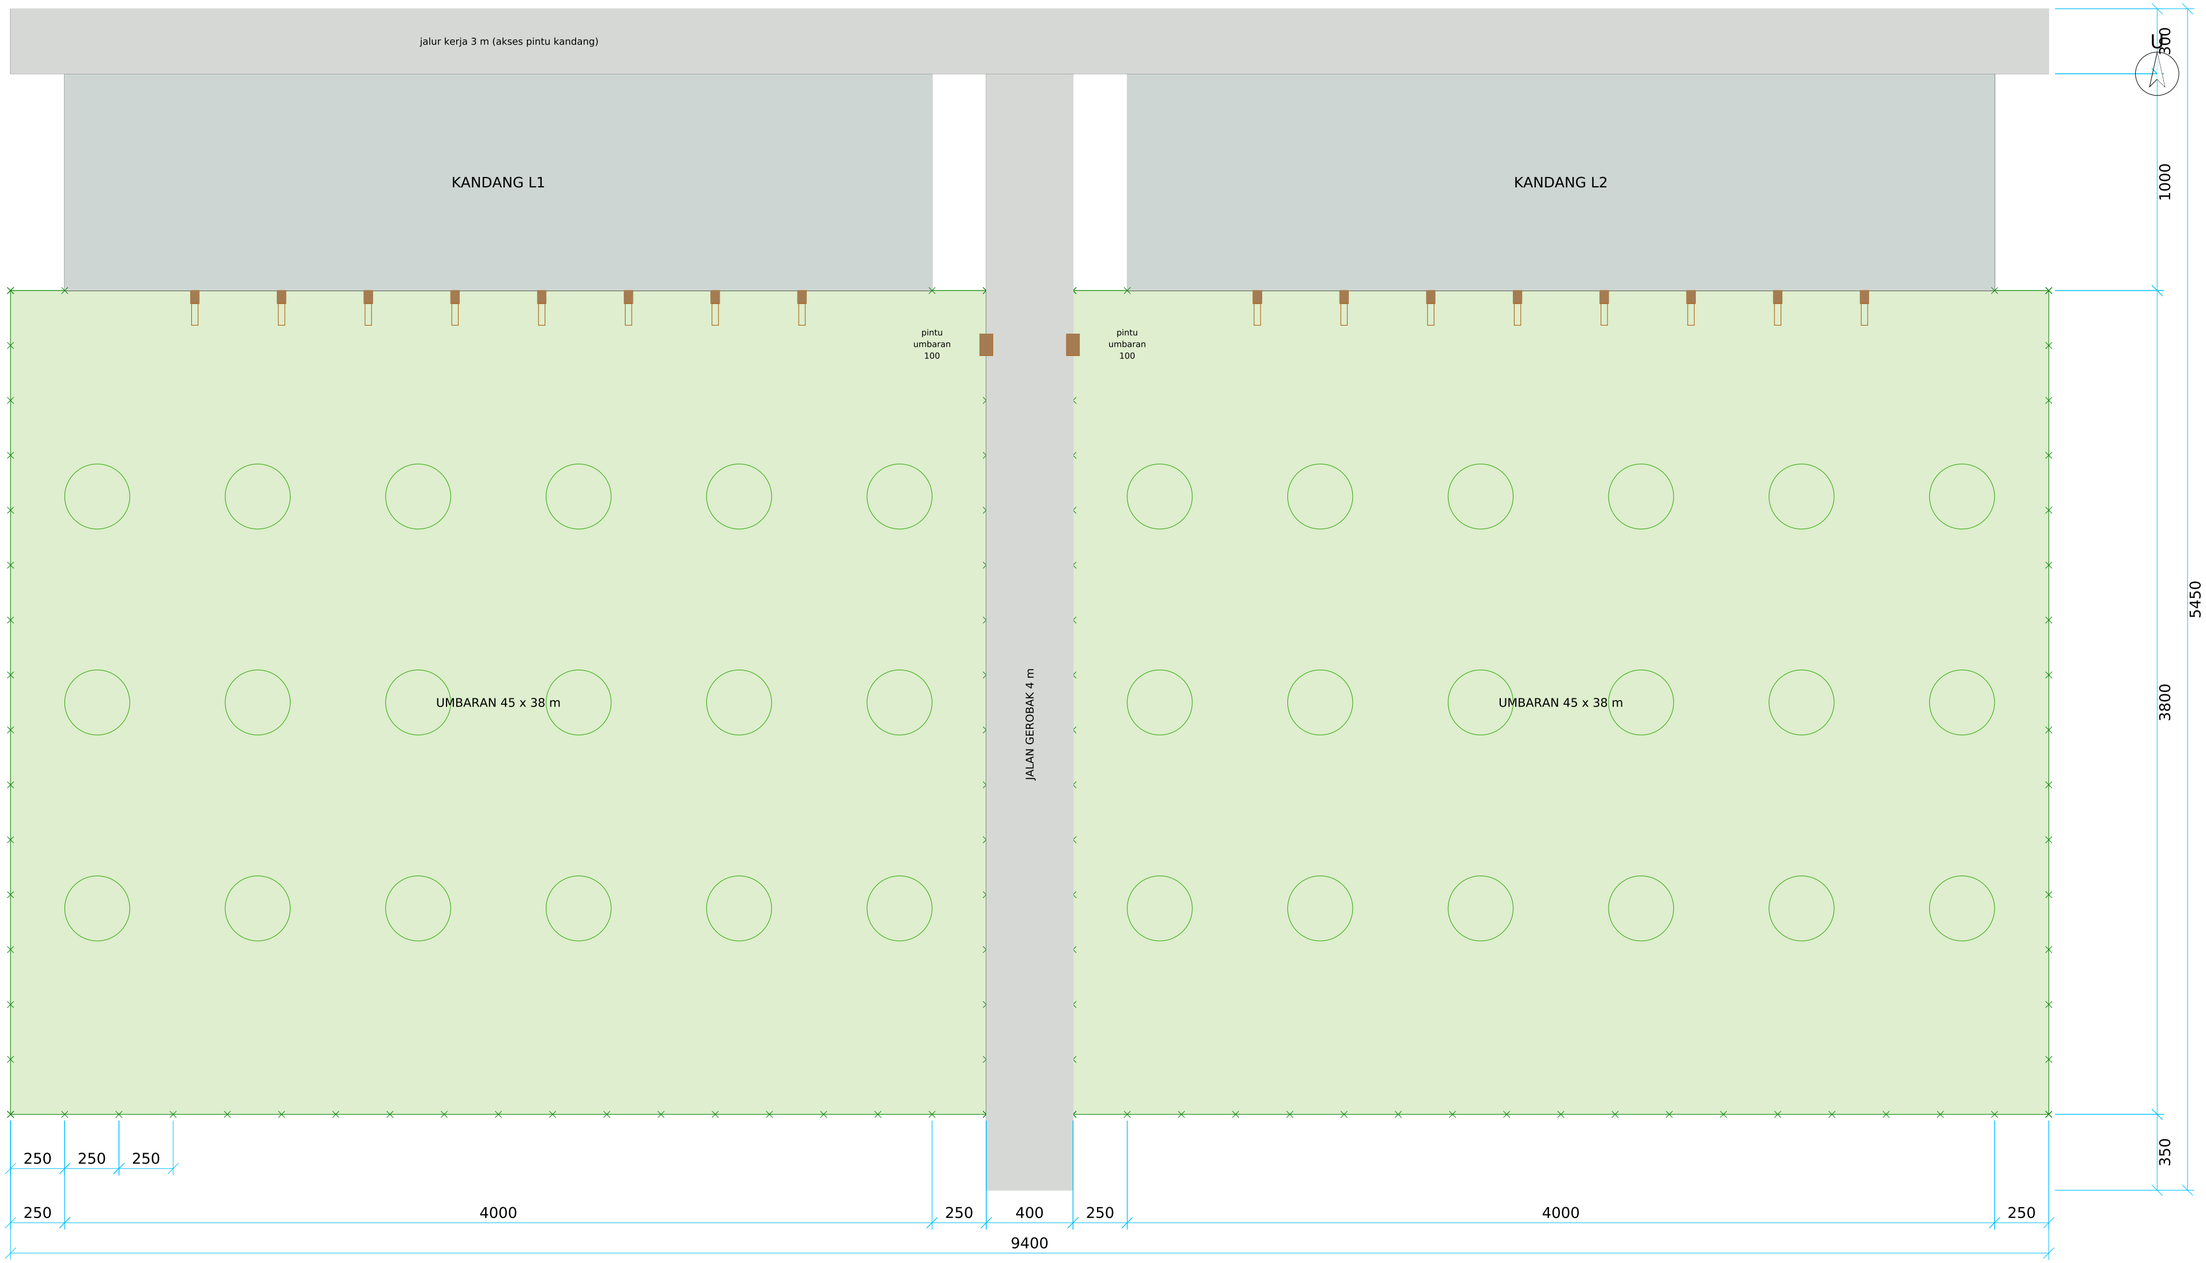


KETENTUAN UNIT

- Pagar umbaran: tiang beton pracetak 10/10 jarak 250 cm (titik pada gambar), kawat harmonika 2" BWG 12.
- Peneduh 18 pohon per petak (3 baris x 6): lamtoro, indigofera, gamal, atau mangga/nangka; lindungi bibit dengan bronjong bambu 1 tahun pertama.
- Tanam rumput lokal/legum penutup tanah; petak yang gundul diistirahatkan dan diganti ke umbaran cadangan.
- Pintu umbaran ke kandang: 8 lubang 40 x 45 cm di dinding selatan (detail K-08).

PROYEK PETERNAKAN AYAM KUB PETELUR SEMI UMBARAN 10.000 EKOR ADEVA FARM - KAB. KONAWE SELATAN, SULAWESI TENGGARA			KERTAS A2
JUDUL GAMBAR UNIT KANDANG DAN UMBARAN (TIPIKAL 1 BARIS)			
CATATAN Satuan cm, elevasi terhadap lantai (±0). Periksa ulang oleh ahli sipil.		SKALA 1 : 200	
TANGGAL OKTOBER 2026	STATUS GAMBAR PERENCANAAN		NO. GAMBAR S-03


TAMPAK PAGAR 2 BENTANG

skala 1 : 20

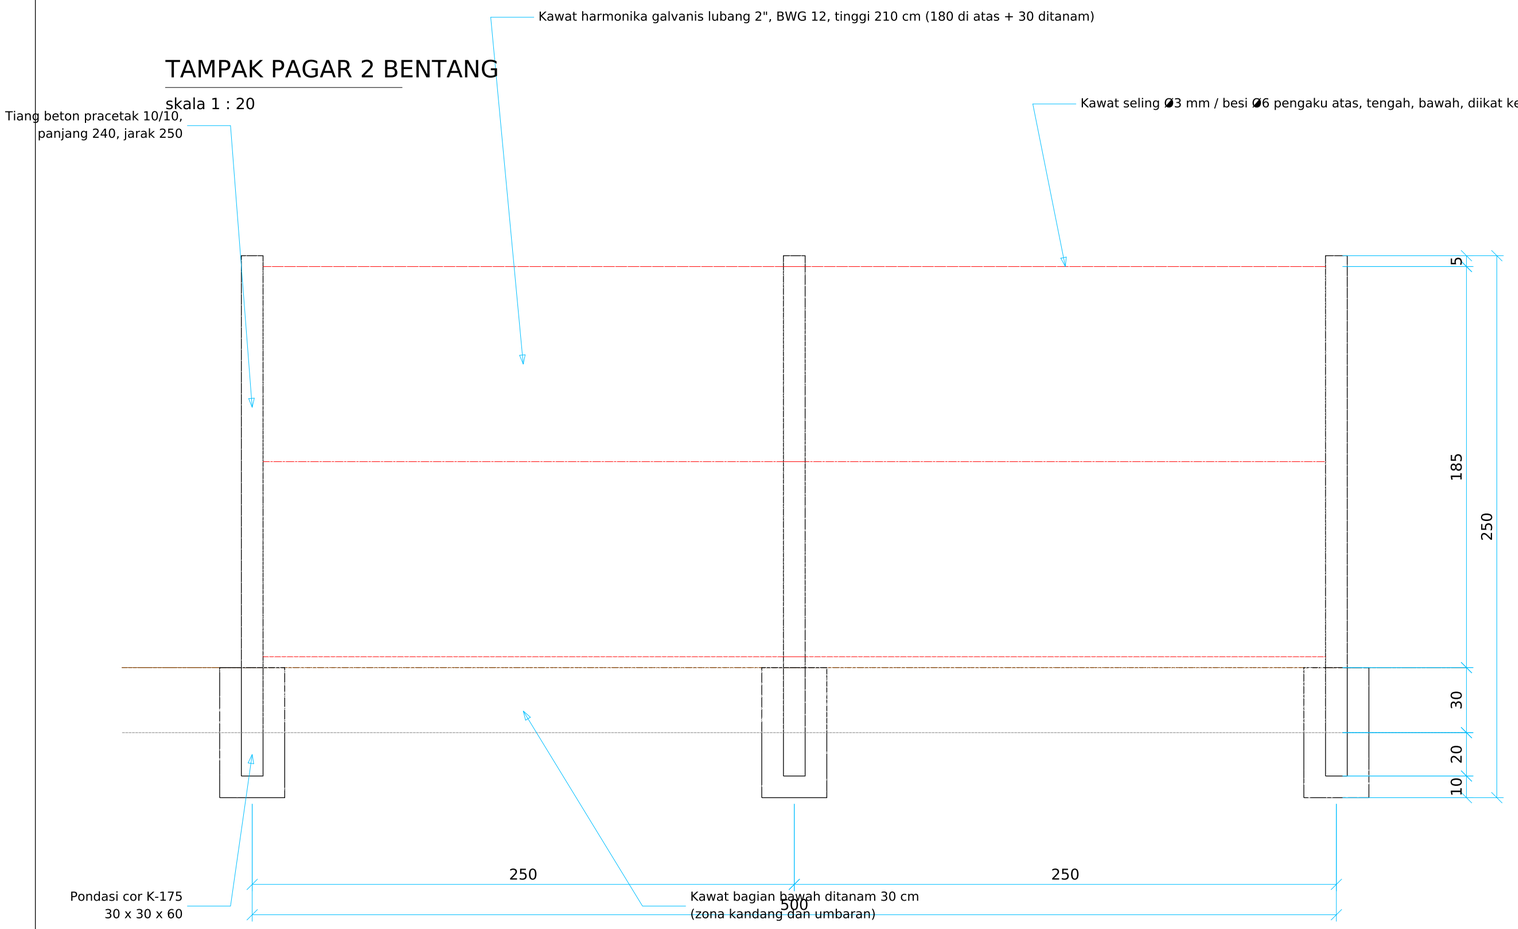

POTONGAN TIANG

skala 1 : 20

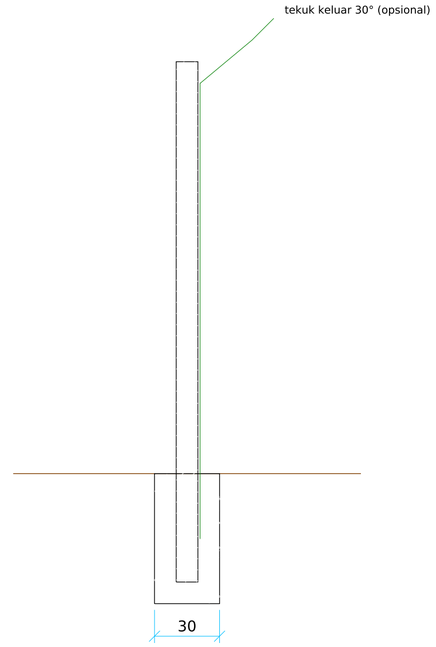

PENAMPANG TIANG



4 ⌀6, sengkang ⌀4-150, K-225


CATATAN PAGAR

- Tiang sudut dan setiap 25 m diberi skur (penopang miring) tiang beton yang sama.
- Pagar keliling lahan ±770 m, pagar zona kandang ±500 m, pagar sekat umbaran ±530 m.
- Tiang boleh dicor di lokasi dengan cetakan papan bila tidak ada pemasok pracetak.

PROYEK	KERTAS A2
PETERNAKAN AYAM KUB PETELUR SEMI UMBARAN 10.000 EKOR ADEVA FARM - KAB. KONAWE SELATAN, SULAWESI TENGGARA	
JUDUL GAMBAR	
DETAIL PAGAR KAWAT HARMONIKA DAN TIANG BETON PRACETAK	
CATATAN Satuan cm, elevasi terhadap lantai (±0). Periksa ulang oleh ahli sipil.	SKALA 1 : 20
TANGGAL OKTOBER 2026	STATUS GAMBAR PERENCANAAN
	NO. GAMBAR P-01


GERBANG UTAMA 600 cm (2 DAUN GESER/ENGSEL)

skala 1 : 50 · gerbang kebun 400 dan gerbang gerobak 300 sama, 1 atau 2 daun

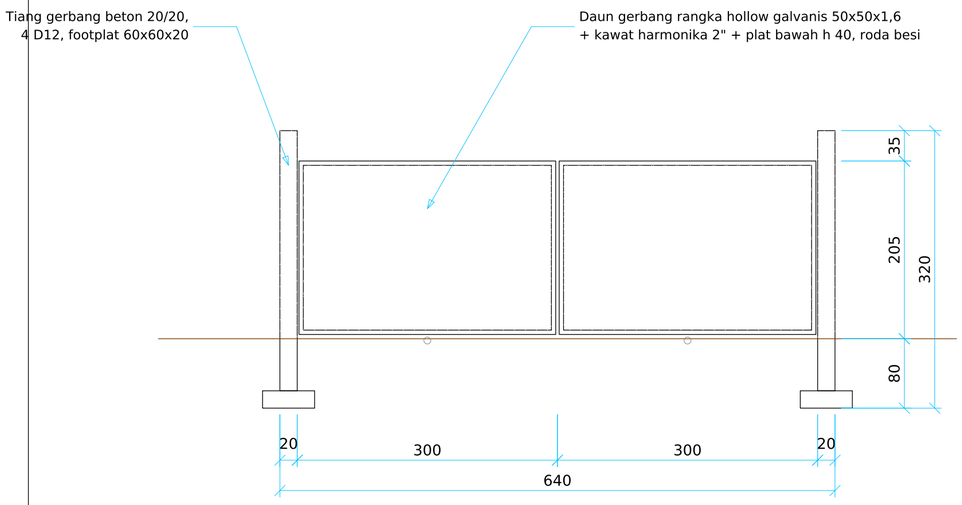

BAK CELUP KENDARAAN (DENAH + POTONGAN)

skala 1 : 50 · di gerbang utama

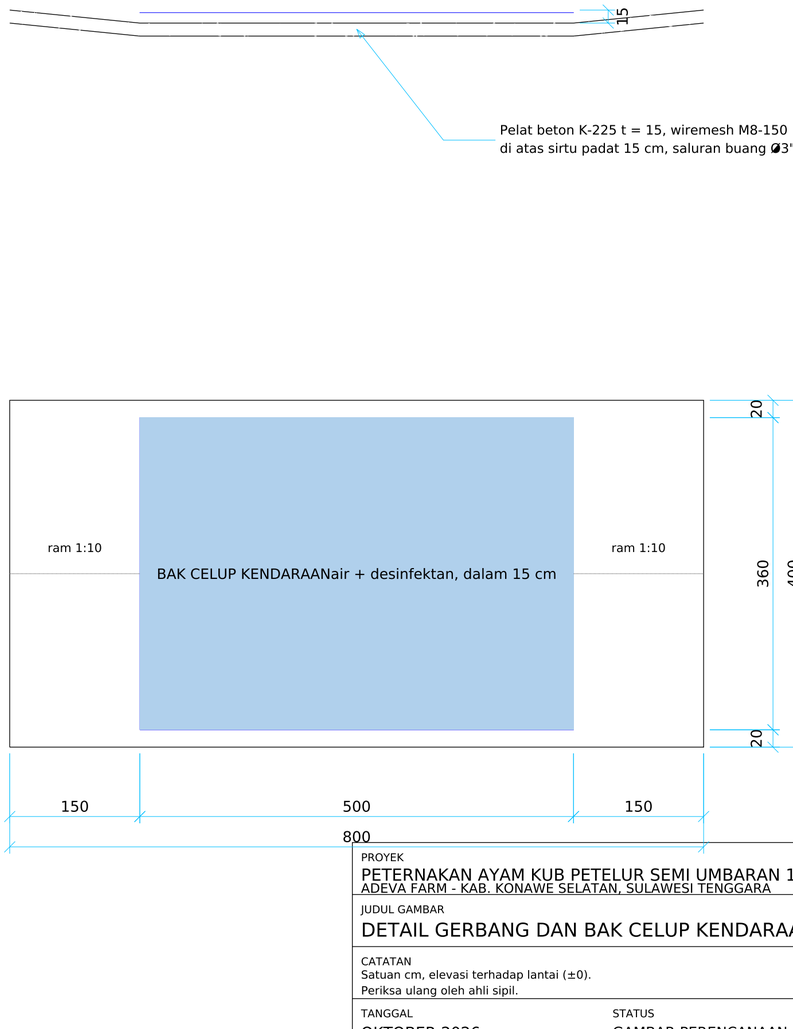

PROYEK	KERTAS A2
PETERNAKAN AYAM KUB PETELUR SEMI UMBARAN 10.000 EKOR ADEVA FARM - KAB. KONAWE SELATAN, SULAWESI TENGGARA	
JUDUL GAMBAR	
DETAIL GERBANG DAN BAK CELUP KENDARAAN	
CATATAN Satuan cm, elevasi terhadap lantai (±0). Periksa ulang oleh ahli sipil.	SKALA 1 : 50
TANGGAL OKTOBER 2026	STATUS GAMBAR PERENCANAAN
	NO. GAMBAR P-02