

DENAH GUDANG JAGUNG (TIPIKAL)

skala 1 : 100 · kapasitas ±60 ton jagung pipil

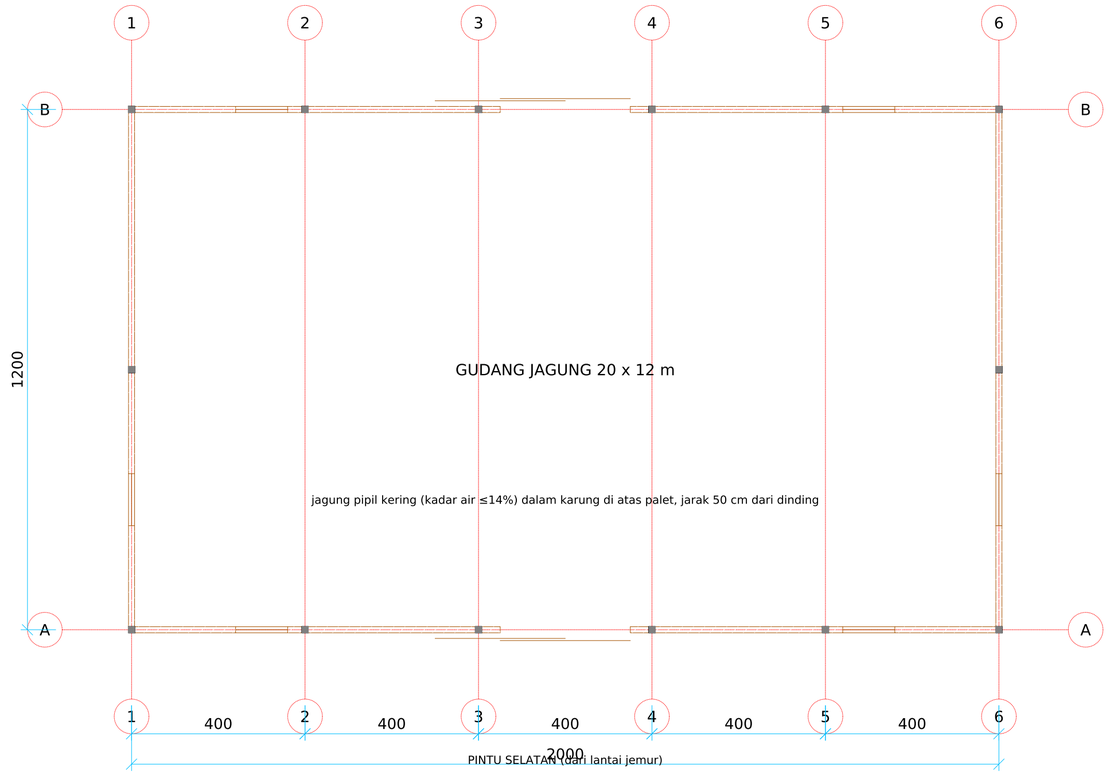

POTONGAN MELINTANG

skala 1 : 100

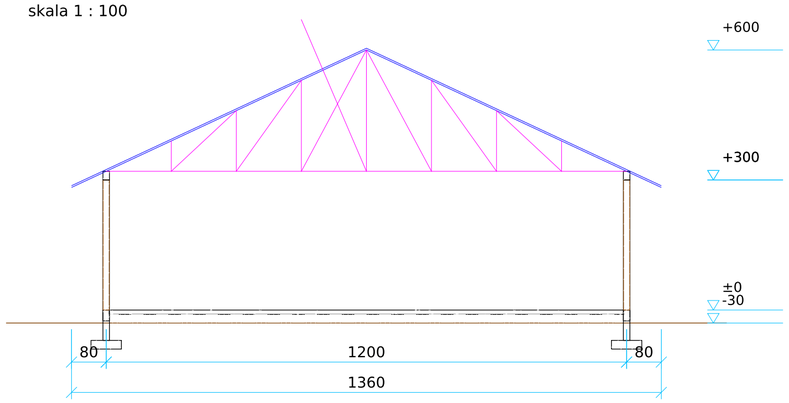

TABEL BANGUNAN FASILITAS (STRUKTUR TIPIKAL SAMA)

BANGUNAN	UKURAN (cm)	DINDING BATA	LANTAI	PINTU	KETERANGAN
Pos jaga	400 x 300	h 300 penuh	beton t=10	80 x 210 (1)	GT-04 B-01
Kantor	800 x 600	h 300 penuh	beton t=10	90 x 210 (2)	GT-04 B-02
Mes anak kandang	1200 x 800	h 300 penuh	beton t=10	90 x 210 (2)	GT-04 B-03
Rumah telur (sortir & simpan)	1200 x 800	h 300 penuh	beton t=10	120 x 210 (2)	GT-04 B-04
Rumah pakan (olah & campur)	1600 x 1200	h 150 + kawat	beton t=10	300 x 300 (3)	GT-04 B-05
Gudang pakan jadi	2000 x 1000	h 300 penuh	beton t=10	300 x 300 (2)	GT-04 B-06
Gudang jagung	2000 x 1200	h 300 penuh	beton t=10	300 x 300 (2)	F-01
Ruang ganti + celup kaki	600 x 400	h 300 penuh	beton t=10	90 x 210 (2)	F-02
Rumah kompos	1600 x 1000	h 100 + kawat	beton t=10	terbuka	GT-04 B-07
Rumah maggot BSF	1200 x 800	h 100 + kawat	beton t=10	120 x 210 (1)	GT-04 B-08
Kandang karantina	800 x 600	h 50 + kawat	beton t=7	90 x 200 (1)	F-02

SPESIFIKASI TIPIKAL FASILITAS

• Footplat 70x70x20, kolom 15/15, sloof 15/25, ring balk 15/20, beton K-225 (sama dengan kandang, K-05/K-06).
• Kolom jarak ±400 cm, tinggi kolom 300 cm dari lantai.
• Dinding bata 1/2 bata, plester + aci dua sisi, dicat.
• Lantai beton K-175 t = 10 di atas pasir 5 cm dan urugan dipadatkan; peil +30 dari tanah.• Atap baja ringan C75 jarak 120, galvalum 0,30 TCT, kemiringan 25°, overstek 80.• Pintu gudang 300 x 300 geser: rangka hollow 40x40 + plat galvalum; jendela ventilasi kawat nyamuk + teralis.
• Gudang pakan/jagung: celah bawah pintu ditutup karet, lubang angin dipasang kawat (anti tikus dan burung).

PROYEK
PETERNAKAN AYAM KUB PETELUR SEMI UMBARAN 10.000 EKOR
ADEVA FARM - KAB. KONAWE SELATAN, SULAWESI TENGGARA

KERTAS A2

JUDUL GAMBAR
GUDANG JAGUNG 20 X 12 M (GUDANG TIPIKAL)

CATATAN
Satuan cm, elevasi terhadap lantai (±0).
Periksa ulang oleh ahli sipil.

SKALA
1 : 100


TANGGAL
OKTOBER 2026

STATUS
GAMBAR PERENCANAAN

NO. GAMBAR
F-01


DENAH RUANG GANTI + CELUP KAKI 6 x 4 m

skala 1 : 50 · alur satu arah: luar - mandi - dalam

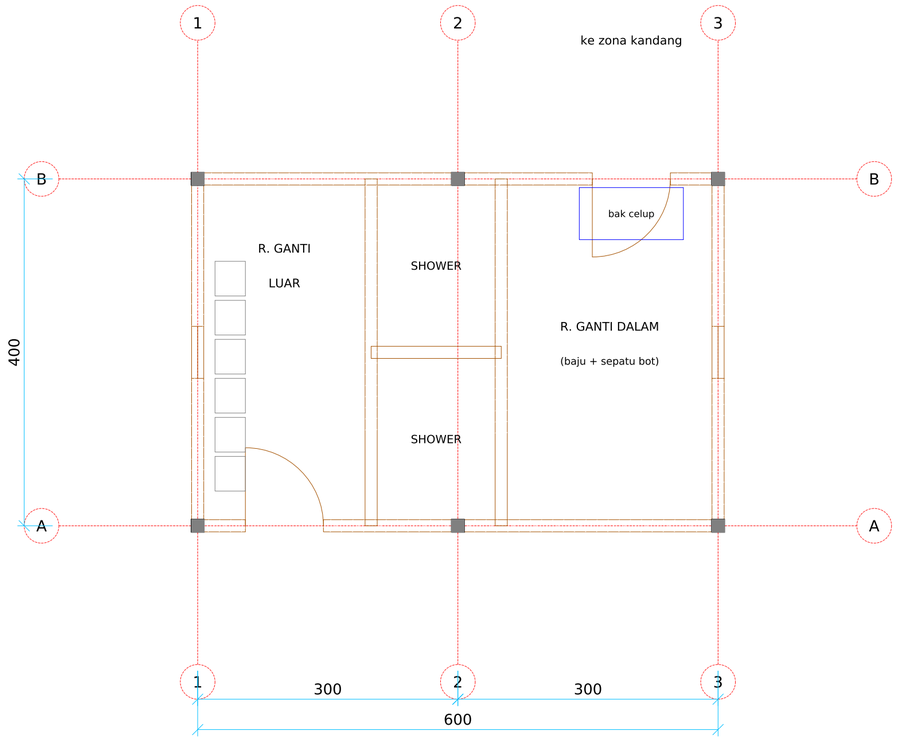

DENAH KANDANG KARANTINA 8 x 6 m

skala 1 : 50 · dinding bata 50 + kawat + tirai, detail seperti K-04/K-08

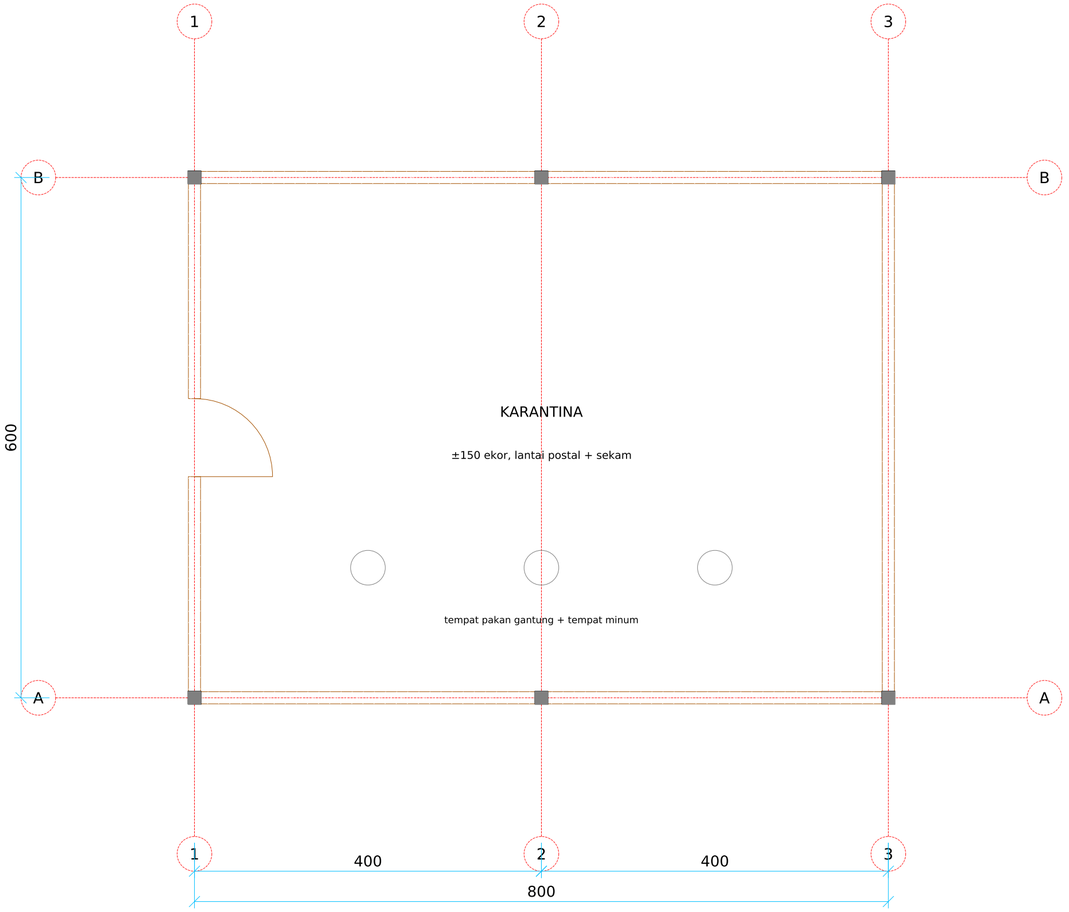


CATATAN
- Struktur dan atap sama dengan gudang tipikal F-01; lantai beton kasar + kemiringan 1% di ruang ganti.
- Ruang ganti dibangun menempel pagar zona kandang: pintu luar dari zona servis, pintu dalam langsung ke zona kandang.
- Pakaian dan sepatu kandang tidak boleh dibawa keluar zona kandang.
- Karantina untuk ayam baru/sakit di zona kotor, jauh dari kandang utama, alat kerja tersendiri.
- Kantor, pos jaga, mes, rumah telur, rumah pakan, gudang pakan, rumah kompos dan rumah maggot BSF: lihat GT-04.

PROYEK PETERNAKAN AYAM KUB PETELUR SEMI UMBARAN 10.000 EKOR ADEVA FARM - KAB. KONAWE SELATAN, SULAWESI TENGGARA		KERTAS A2
JUDUL GAMBAR RUANG GANTI + CELUP KAKI DAN KANDANG KARANTINA		
CATATAN Satuan cm, elevasi terhadap lantai (±0). Periksa ulang oleh ahli sipil.		SKALA 1 : 50
TANGGAL OKTOBER 2026	STATUS GAMBAR PERENCANAAN	NO. GAMBAR F-02

DENAH LANTAI JEMUR 40 x 18 m


skala 1 : 100 · dilatasi tiap 300 cm (isi aspal/karet)

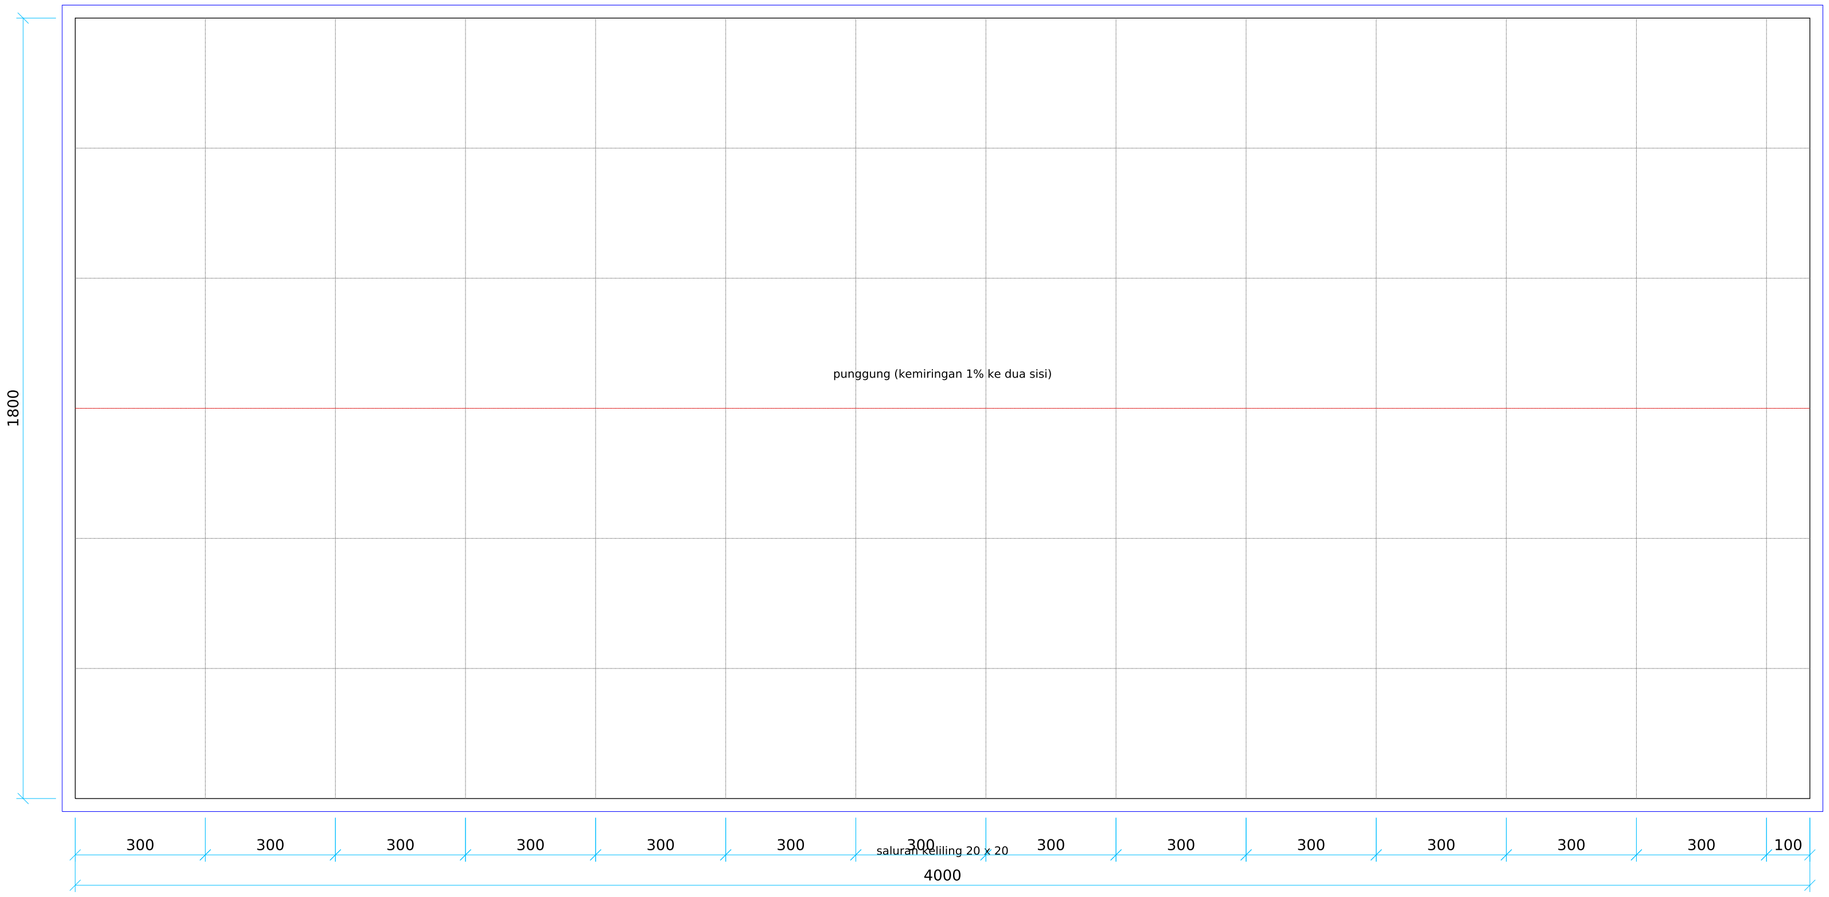


MENARA TANDON + SUMUR BOR

skala 1 : 100 · zona servis


POTONGAN LANTAI JEMUR (tebal digambar tanpa skala)

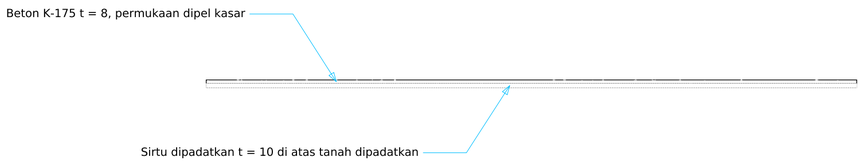

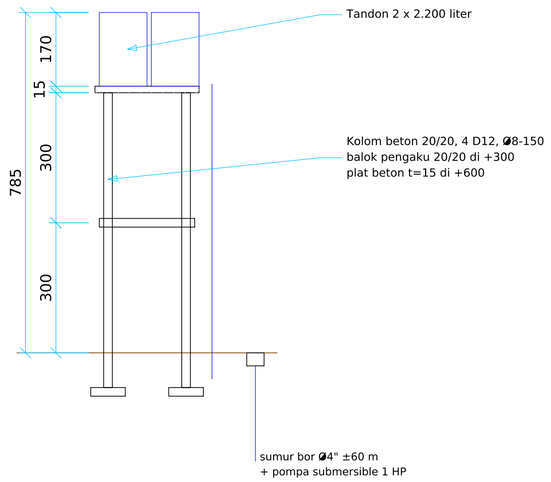

RUMAH POMPA AIR SUNGAI 3 x 3 m


pompa 3" + pipa PVC 3" ke embung & kebun

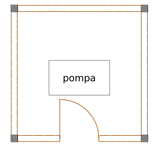

PROYEK	KERTAS A2
PETERNAKAN AYAM KUB PETELUR SEMI UMBARAN 10.000 EKOR ADEVA FARM - KAB. KONAWE SELATAN, SULAWESI TENGGARA	
JUDUL GAMBAR	
LANTAI JEMUR JAGUNG, MENARA TANDON, SUMUR BOR DAN RUMAH POMPA	
CATATAN Satuan cm, elevasi terhadap lantai (±0). Periksa ulang oleh ahli sipil.	SKALA 1 : 100
TANGGAL OKTOBER 2026	STATUS GAMBAR PERENCANAAN
	NO. GAMBAR F-03


DENAH EMBUNG

skala 1 : 200

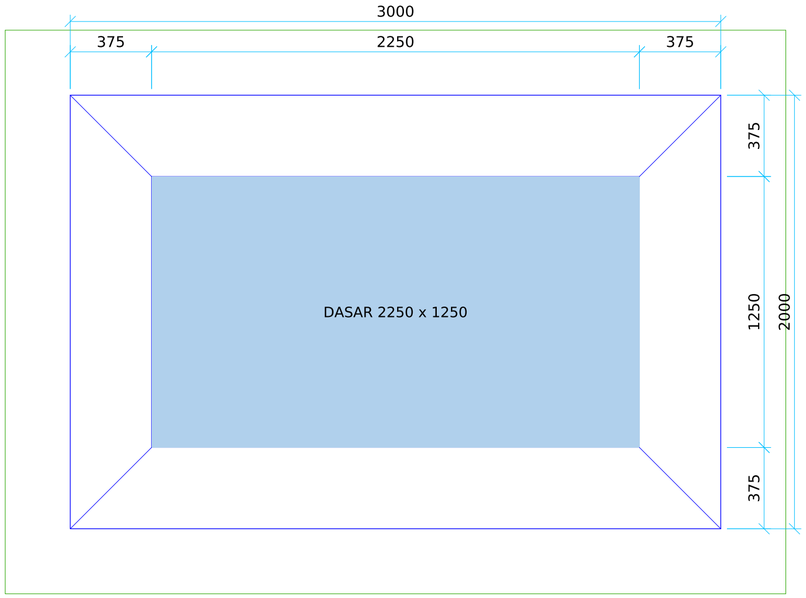

POTONGAN EMBUNG

skala 1 : 200 · volume tampung ±1.000 m³

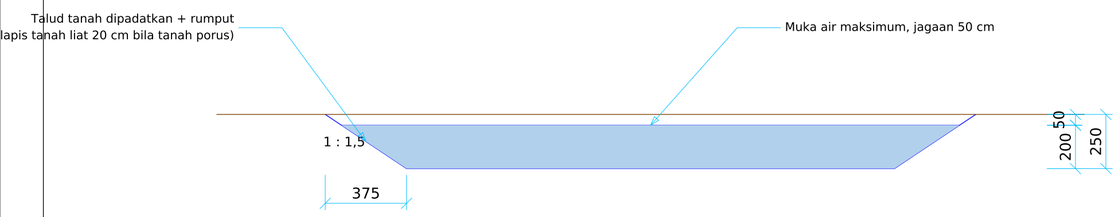

CATATAN

- Embung diisi pompa dari sungai saat musim hujan, dipakai untuk irigasi jagung musim kemarau.
- Air embung dan sungai tidak untuk minum ayam (pakai sumur bor).
- Pagar keliling embung kawat harmonika 120 cm untuk keselamatan anak dan ternak.
- Tanah galian dipakai untuk urugan peninggian lantai kandang dan bangunan.

PROYEK PETERNAKAN AYAM KUB PETELUR SEMI UMBARAN 10.000 EKOR ADEVA FARM - KAB. KONAWE SELATAN, SULAWESI TENGGARA			KERTAS A2
JUDUL GAMBAR EMBUNG PENAMPUNG AIR 30 X 20 X 2,5 M			
CATATAN Satuan cm, elevasi terhadap lantai (±0). Periksa ulang oleh ahli sipil.		SKALA 1 : 200	
TANGGAL OKTOBER 2026	STATUS GAMBAR PERENCANAAN		NO. GAMBAR F-04