

DENAH POS JAGA

skala 1 : 50 · lokasi tapak x 41 m, y 1,5 m dari pagar depan

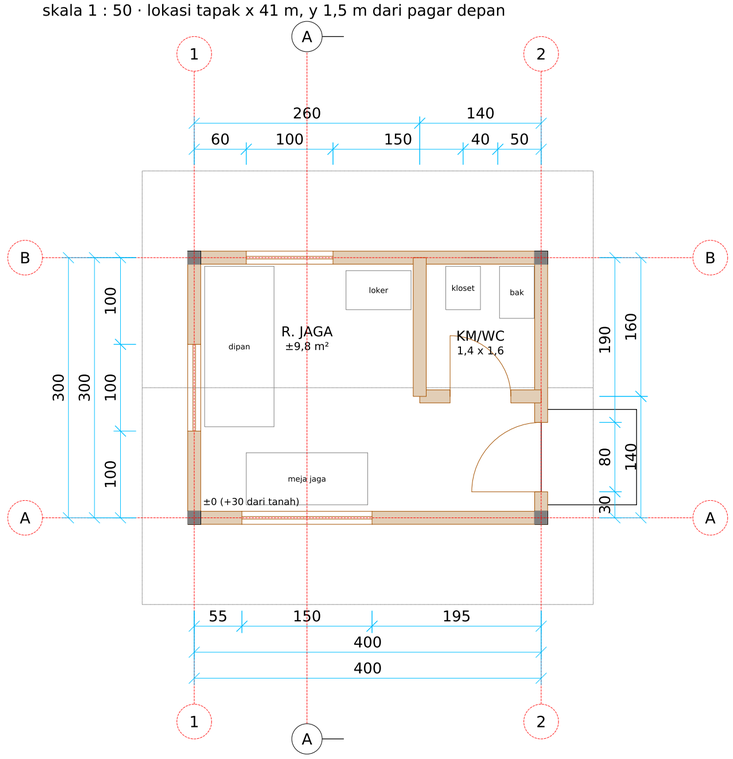

POTONGAN A-A

skala 1 : 50

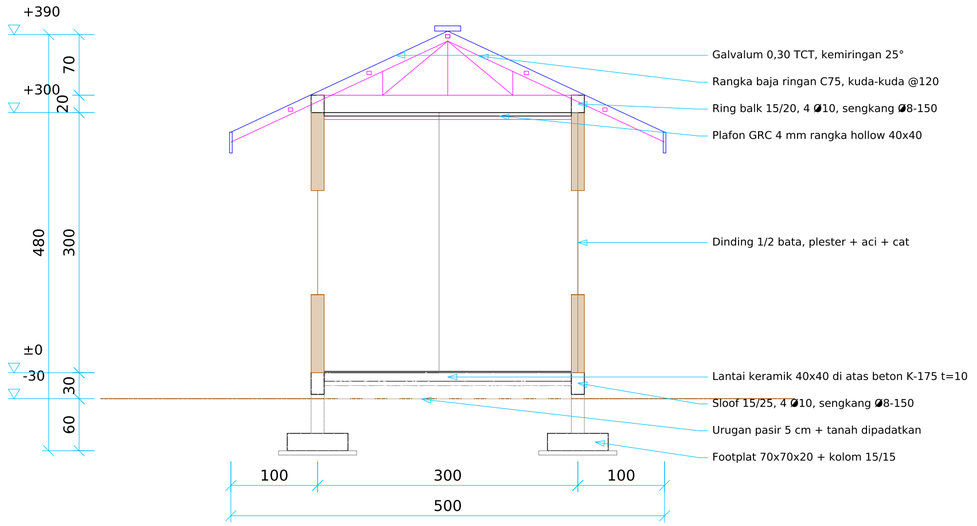


CATATAN POS JAGA

- Pos jaga di sisi kiri gerbang utama: pintu menghadap jalan masuk, jendela ke jalan desa dan ke barat.
- Tamu dicatat di buku tamu; kendaraan wajib lewat bak celup dan disemprot desinfektan.
- Kolom hanya di 4 sudut; overstek 100 cm melindungi petugas di depan pintu.
- Atap: rangka baja ringan C75 kuda-kuda @120, reng @ sesuai galvalum, galvalum 0,30 TCT, kemiringan 25°.
- Dinding 1/2 bata plester aci cat; plafon GRC +300; lantai keramik 40x40.
- KM 1,4 x 1,6 m dengan kloset jongkok, bak 40x60; buangan ke septic biofil 1 m³.
- Listrik: 2 titik lampu dalam, 1 lampu sorot 50 W ke gerbang, 1 stop kontak.


TAMPAK SELATAN (ARAH JALAN)

skala 1 : 50

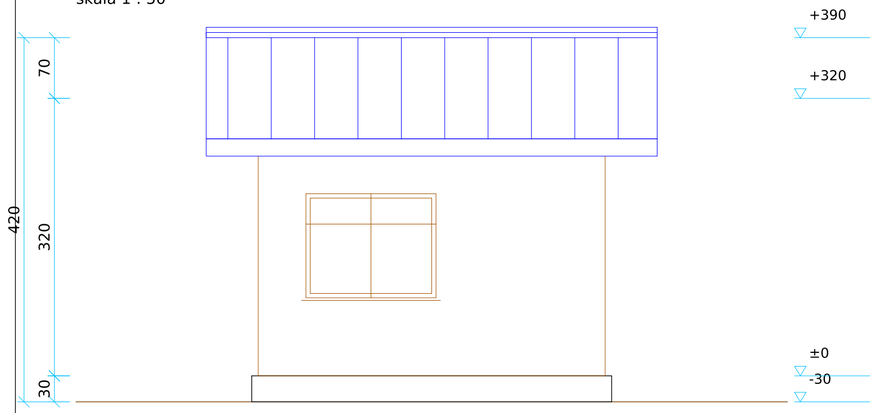


TAMPAK TIMUR (ARAH GERBANG)

skala 1 : 50

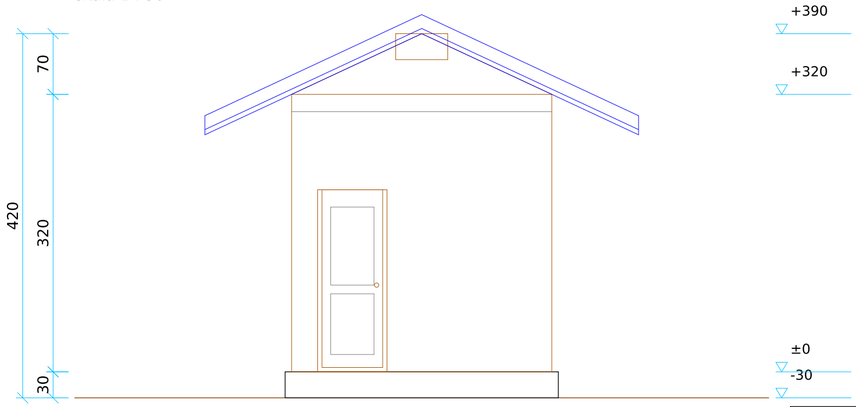

TAMPAK PORTAL PALANG GERBANG


skala 1 : 50 · dipasang di depan bak celup kendaraan

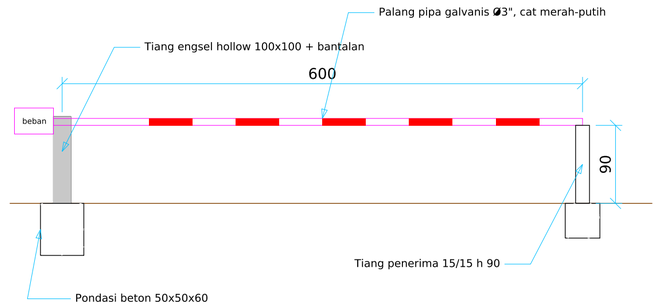

PROYEK	KERTAS A2
PETERNAKAN AYAM KUB PETELUR SEMI UMBARAN 10.000 EKOR ADEVA FARM - KAB. KONAWE SELATAN, SULAWESI TENGGARA	
JUDUL GAMBAR	
POS JAGA 4 X 3 M DAN PORTAL GERBANG	
CATATAN Satuan cm, elevasi terhadap lantai (±0). Periksa ulang oleh ahli sipil.	SKALA 1 : 50
TANGGAL OKTOBER 2026	STATUS GAMBAR PERENCANAAN
	NO. GAMBAR B-01


DENAH KANTOR

skala 1 : 50 · 8 x 6 m · lokasi tapak x 26 m, y 4 m dari pagar depan

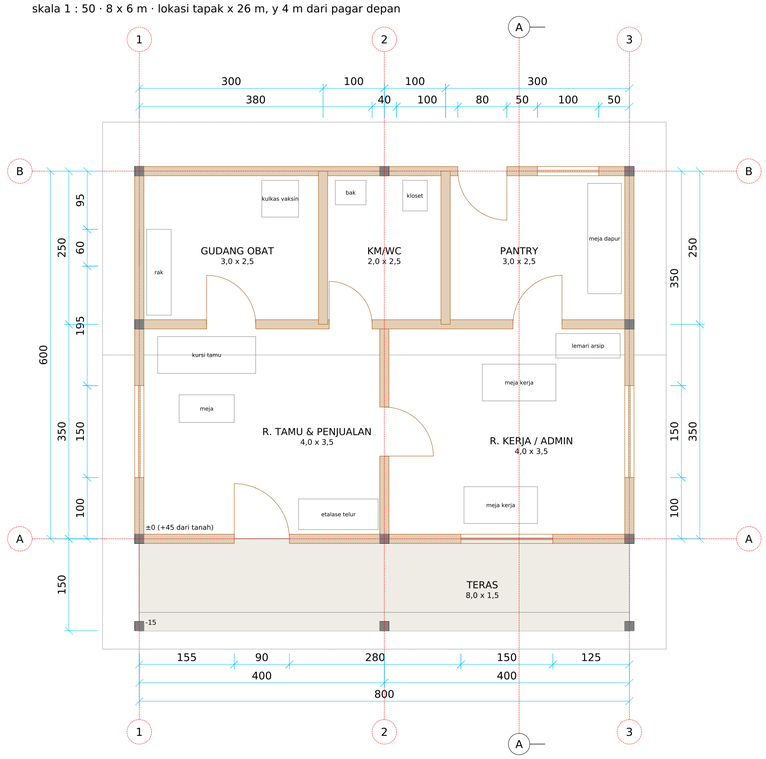

POTONGAN A-A

skala 1 : 50

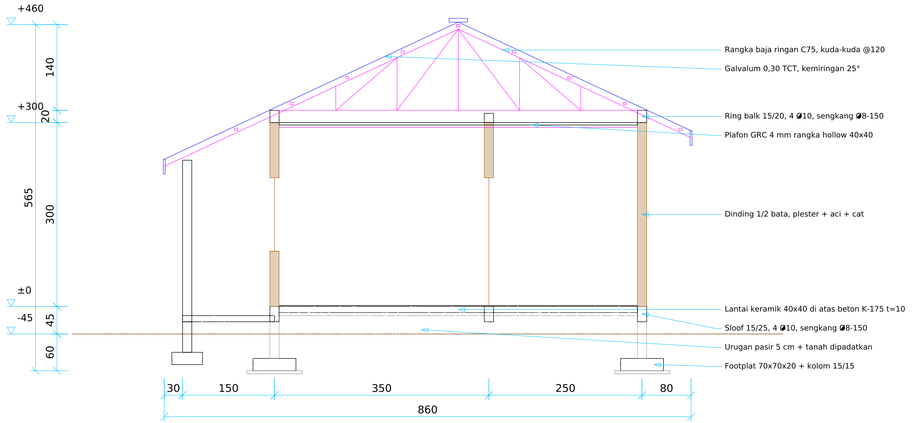


SPESIFIKASI

- Kantor di dekat parkir: tamu dan pembeli telur dilayani di sini, tidak masuk zona kandang.
- R. tamu merangkap tempat penjualan telur (etalase), R. kerja untuk administrasi dan catatan produksi.
- Gudang obat & vaksin dengan kulkas khusus vaksin (2-8 °C), dikunci.
- Teras 8 x 1,5 m, lantai -15 dari lantai dalam.

- Struktur: footplat 70×70×20, kolom 15/15 (4 ⌀10, ⌀8-150), sloof 15/25, ring balk 15/20, beton K-225 (detail sama GT-01 K-05/K-06).
- Atap: rangka baja ringan C75 kuda-kuda @120, reng @ sesuai galvalum, galvalum 0,30 TCT, kemiringan 25°.
- Lantai: urugan tanah dipadatkan per 20 cm, pasir 5 cm, beton K-175 t=10.
- Dinding 1/2 bata, plester 1:4 + aci + cat tembok; bagian KM plester 1:3 kedap air setinggi 150.
- Balok latei 15/15 di atas semua kusen pintu/jendela; kolom praktis 15/15 di setiap pertemuan dinding.
- Plafon GRC 4 mm rangka hollow 40x40 @60, tinggi +300.
- Lantai keramik 40x40 (KM: keramik kasar 20x20, miring 1% ke floor drain).
- Kusen kayu kelas II / aluminium; daftar pintu & jendela lihat B-10.
- Air buangan KM ke septic tank biofil + sumur resapan (B-10), jarak ≥10 m dari sumur bor.
- Listrik: 7 titik lampu, 6 stop kontak (1 khusus kulkas vaksin).


TAMPAK DEPAN (SELATAN)

skala 1 : 50

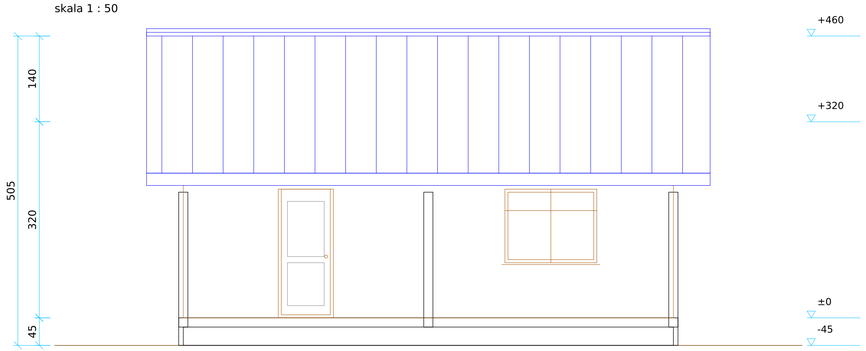

TAMPAK SAMPING (BARAT)


skala 1 : 50

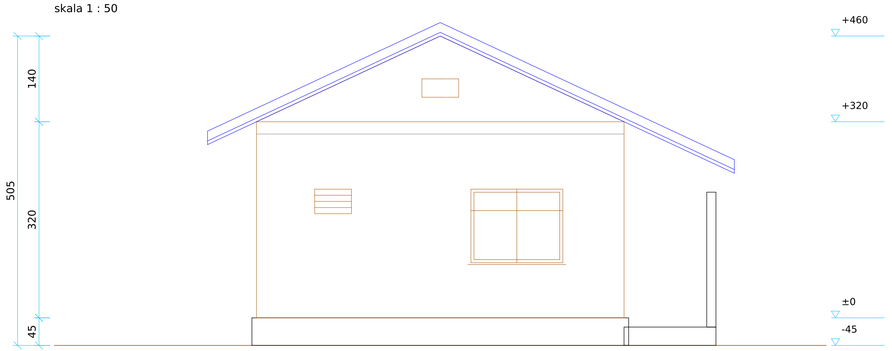

PROYEK	KERTAS A1
PETERNAKAN AYAM KUB PETELUR SEMI UMBARAN 10.000 EKOR ADEVA FARM - KAB. KONAWE SELATAN, SULAWESI TENGGARA	
JUDUL GAMBAR	
KANTOR 8 X 6 M	
CATATAN Satuan cm, elevasi terhadap lantai (±0). Periksa ulang oleh ahli sipil.	SKALA 1 : 50
TANGGAL OKTOBER 2026	STATUS GAMBAR PERENCANAAN
	NO. GAMBAR B-02


DENAH MES ANAK KANDANG

skala 1 : 50 · 12 x 8 m · lokasi tapak x 12 m, y 30 m dari pagar depan

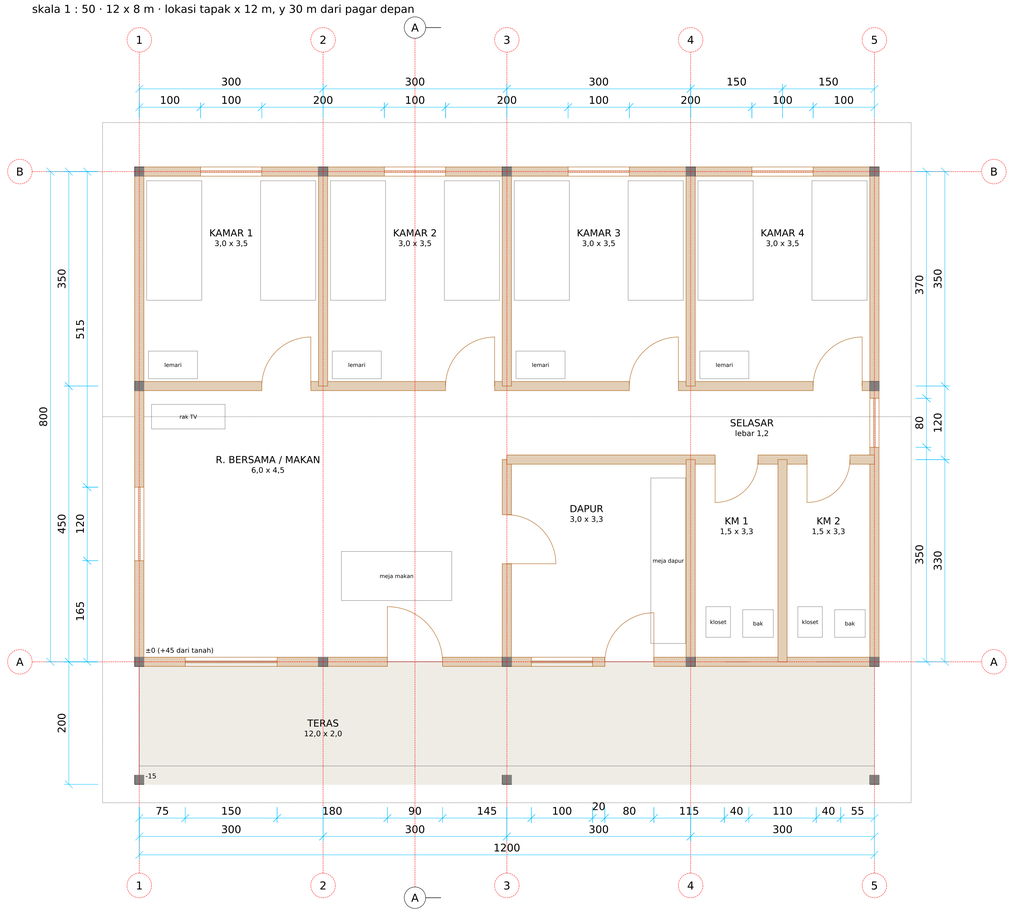

POTONGAN A-A

skala 1 : 50

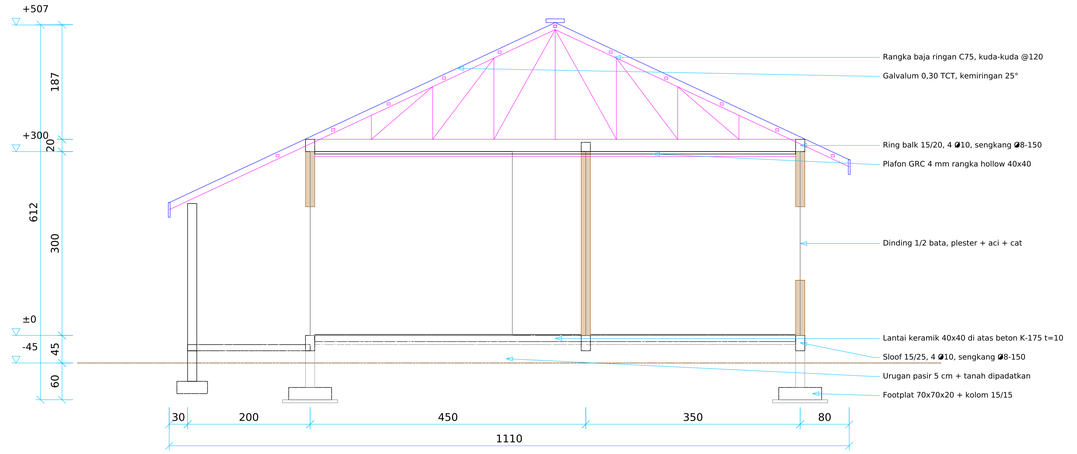


SPESIFIKASI

- Untuk 6-8 pekerja kandang: 4 kamar 3 x 3,5 m (2 orang per kamar).
- R. bersama untuk makan, istirahat, rapat pagi; dapur bersama; 2 KM/WC.
- Letak di zona servis, 12 m dari pagar zona kandang: pekerja wajib lewat ruang ganti sebelum masuk kandang.
- Teras 12 x 2 m untuk duduk dan menjemur pakaian (bukan pakaian kandang).

- Struktur: footplat 70x70x20, kolom 15/15 (4 ø10, ø8-150), sloof 15/25, ring balk 15/20, beton K-225 (detail sama GT-01 K-05/K-06).
- Atap: rangka baja ringan C75 kuda-kuda @120, reng @ sesuai galvalum, galvalum 0,30 TCT, kemiringan 25°.
- Lantai: urugan tanah dipadatkan per 20 cm, pasir 5 cm, beton K-175 t=10.
- Dinding 1/2 bata, plester 1:4 + aci + cat tembok; bagian KM plester 1:3 kedap air setinggi 150.
- Balok latei 15/15 di atas semua kusen pintu/jendela; kolom praktis 15/15 di setiap pertemuan dinding.
- Plafon GRC 4 mm rangka hollow 40x40 @60, tinggi +300.
- Lantai keramik 40x40 (KM: keramik kasar 20x20, miring 1% ke floor drain).
- Kusen kayu kelas II / aluminium; daftar pintu & jendela lihat B-10.
- Air buangan KM ke septic tank biofil + sumur resapan (B-10), jarak ≥10 m dari sumur bor.
- Septic tank biofil 2 m³ di sisi utara mes.
- Listrik: 12 titik lampu, 8 stop kontak; air dari menara tandon.


TAMPAK DEPAN (SELATAN)

skala 1 : 50

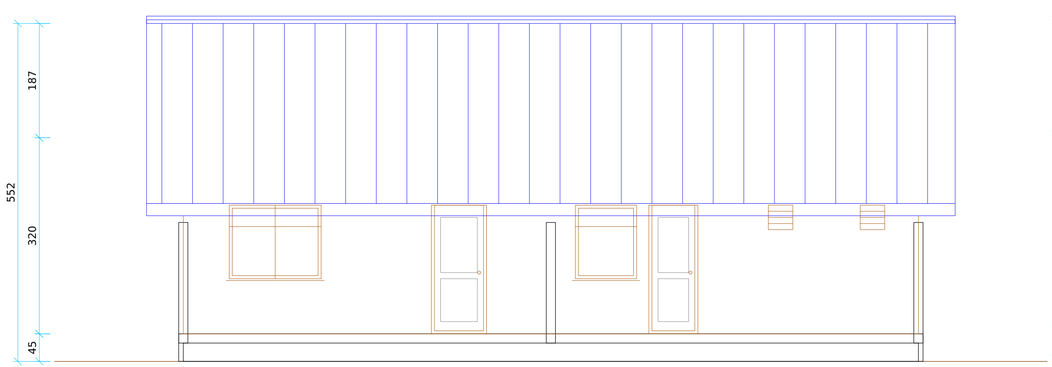

TAMPAK SAMPING (BARAT)


skala 1 : 50

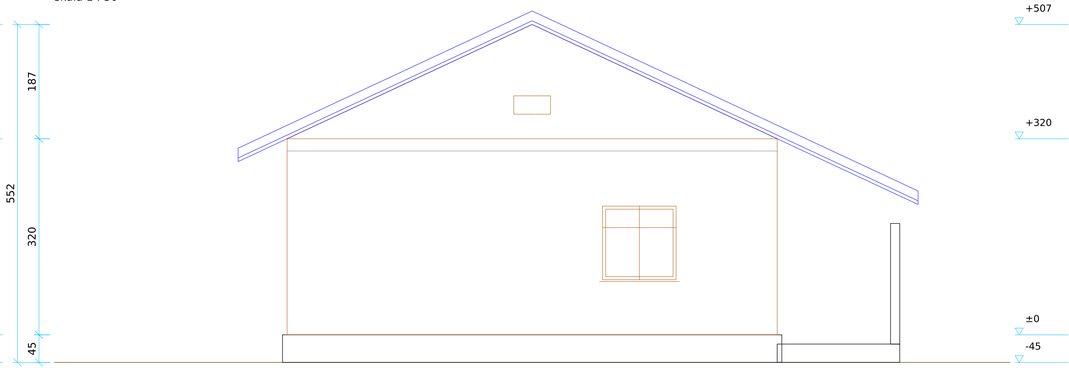

PROYEK	KERTAS A1
PETERNAKAN AYAM KUB PETELUR SEMI UMBARAN 10.000 EKOR ADEVA FARM - KAB. KONAWE SELATAN, SULAWESI TENGGARA	
JUDUL GAMBAR	
MES ANAK KANDANG 12 X 8 M	
CATATAN Satuan cm, elevasi terhadap lantai (±0). Periksa ulang oleh ahli sipil.	SKALA 1 : 50
TANGGAL OKTOBER 2026	STATUS GAMBAR PERENCANAAN
	NO. GAMBAR B-03


DENAH RUMAH TELUR (SORTIR & SIMPAN)

skala 1 : 50 · 12 x 8 m · lokasi tapak x 32 m, y 15 m dari pagar depan

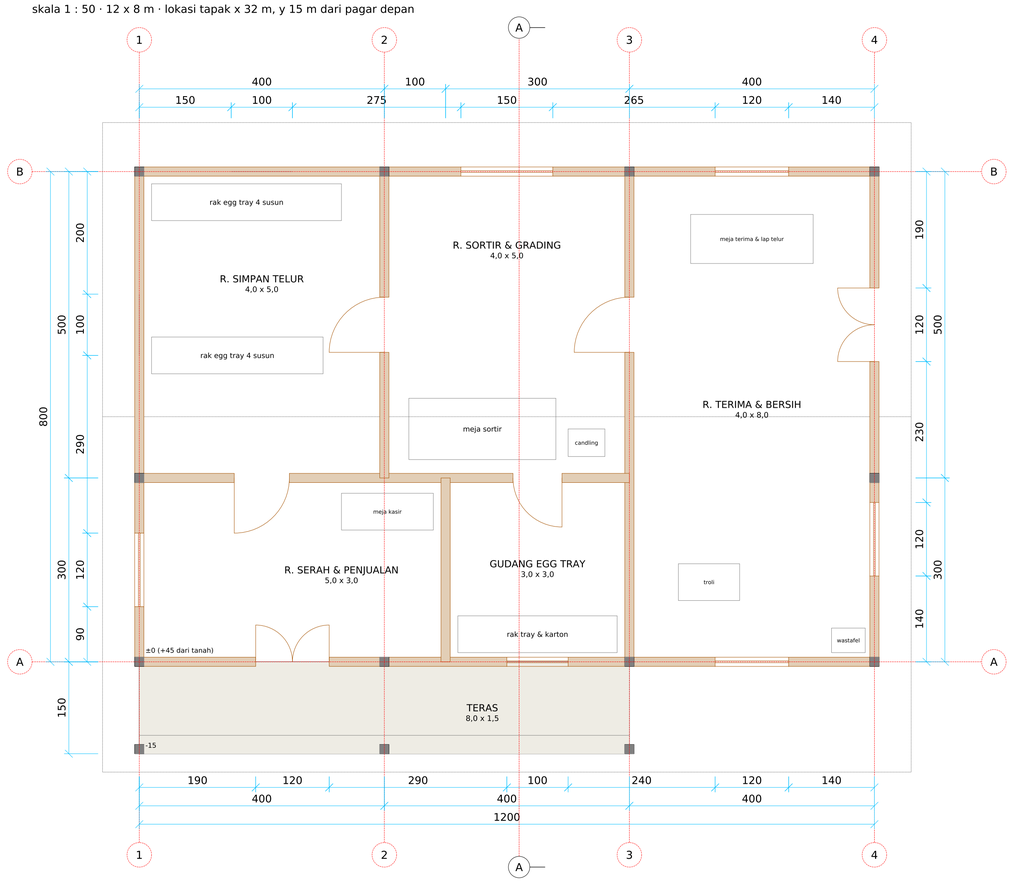

POTONGAN A-A

skala 1 : 50

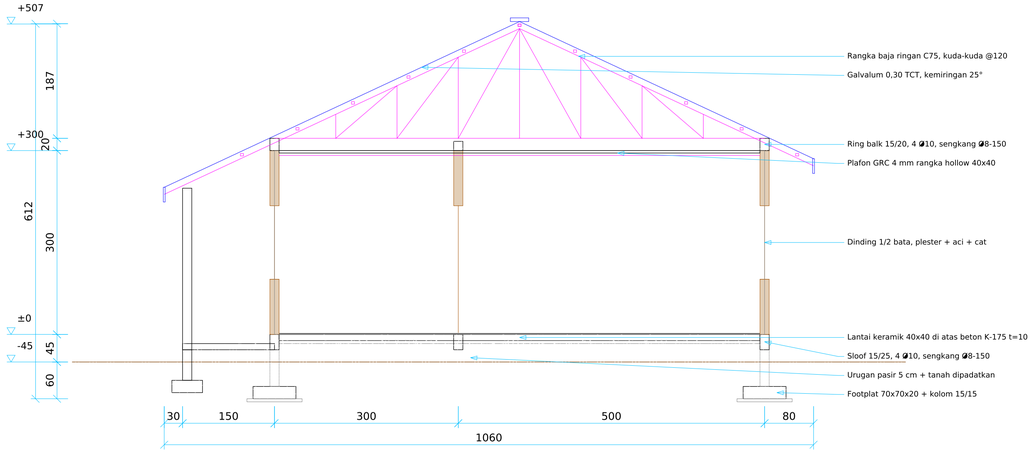

SPESIFIKASI


ALUR TELUR: troli dari zona kandang masuk pintu timur -> R. terima (lap kering, buang retak) ->
R. sortir (candling + timbang per kelas) -> R. simpan (rak) ->
R. serah -> pembeli di teras/parkir.

- Produksi ±5.000 butir/hari = ±170 tray; R. simpan muat ±480 tray (3 hari produksi).
- R. simpan sejuk dan gelap: dinding dua sisi diaci, plafon, ventilasi kawat kasa di atas, kipas exhaust 12".
- Telur tidak dicuci basah; kotoran kering dilap/amplas halus.
- Meja sortir & rak egg tray: detail B-10.

- Struktur: footplat 70x70x20, kolom 15/15 (4 ø10, ø8-150), sloof 15/25, ring balk 15/20, beton K-225 (detail sama GT-01 K-05/K-06).
- Atap: rangka baja ringan C75 kuda-kuda @120, reng @ sesuai galvalum, galvalum 0,30 TCT, kemiringan 25°.
- Lantai: urugan tanah dipadatkan per 20 cm, pasir 5 cm, beton K-175 t=10.
- Dinding 1/2 bata, plester 1:4 + aci + cat tembok; bagian KM plester 1:3 kedap air setinggi 150.
- Balok latei 15/15 di atas semua kusen pintu/jendela; kolom praktis 15/15 di setiap pertemuan dinding.
- Plafon GRC 4 mm rangka hollow 40x40 @60, tinggi +300.
- Lantai keramik 40x40 (KM: keramik kasar 20x20, miring 1% ke floor drain).
- Kusen kayu kelas II / aluminium; daftar pintu & jendela lihat B-10.
- Listrik: 8 titik lampu, 4 stop kontak, 1 kipas exhaust, lampu candling.

TAMPAK DEPAN (SELATAN)

skala 1 : 50

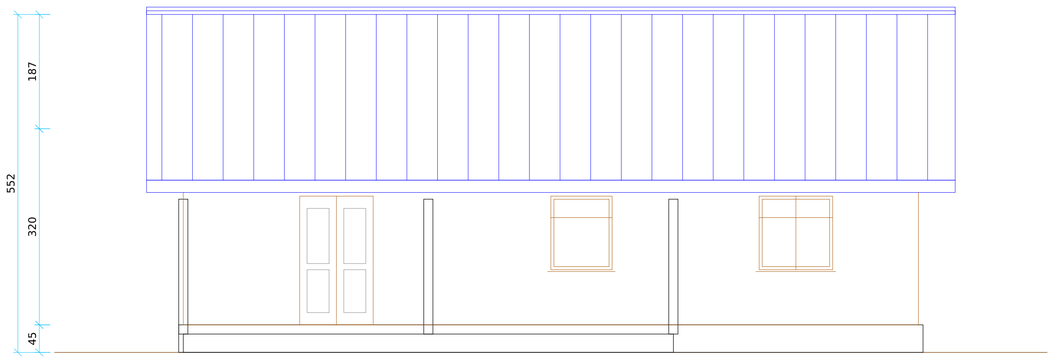

TAMPAK SAMPING (TIMUR)


skala 1 : 50



PROYEK: PETERNAKAN AYAM KUB PETELUR SEMI UMBARAN 10.000 EKOR ADEVA FARM - KAB. KONAWE SELATAN, SULAWESI TENGGARA			KERTAS A1
JUDUL GAMBAR: RUMAH TELUR (SORTIR & SIMPAN) 12 X 8 M			
CATATAN: Satuan cm, elevasi terhadap lantai (±0). Periksa ulang oleh ahli sipil.		SKALA: 1 : 50	
TANGGAL: OKTOBER 2026	STATUS: GAMBAR PERENCANAAN		NO. GAMBAR: B-04


DENAH RUMAH PAKAN (OLAH & CAMPUR)

skala 1 : 100 · 16 x 12 m · lokasi tapak x 54 m, y 25 m dari pagar depan

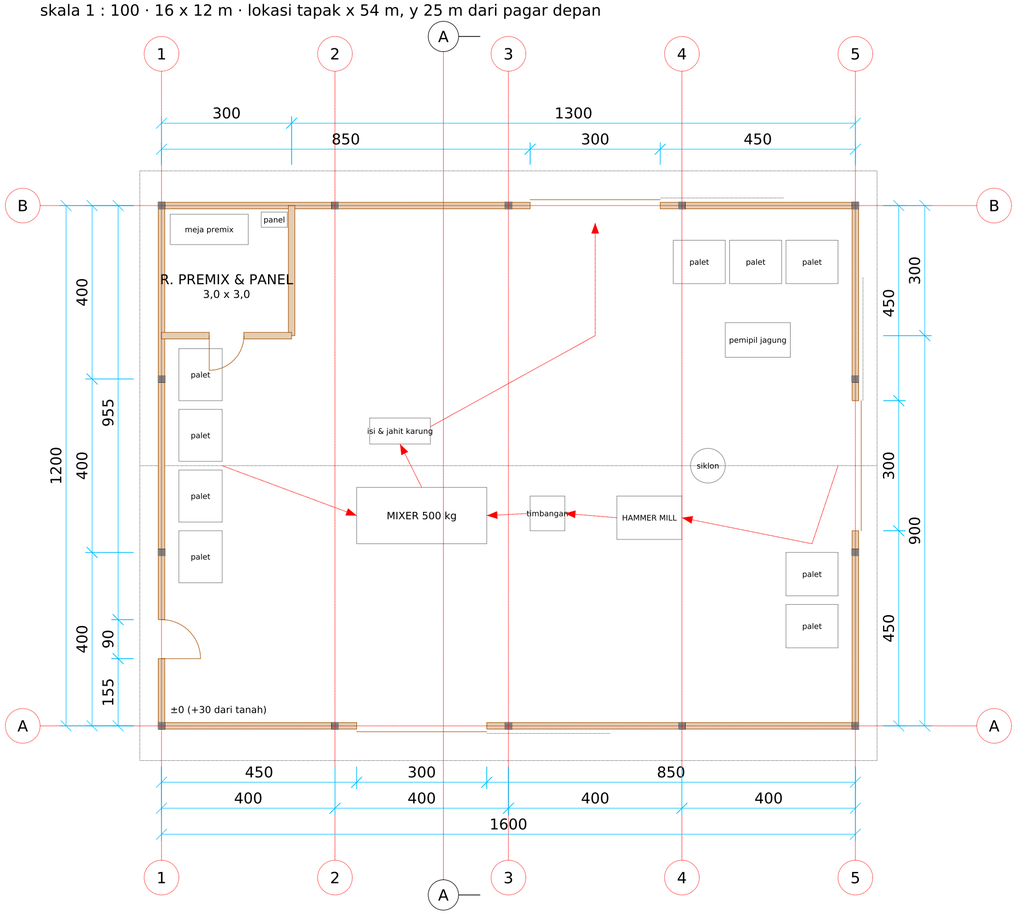

POTONGAN A-A

skala 1 : 100

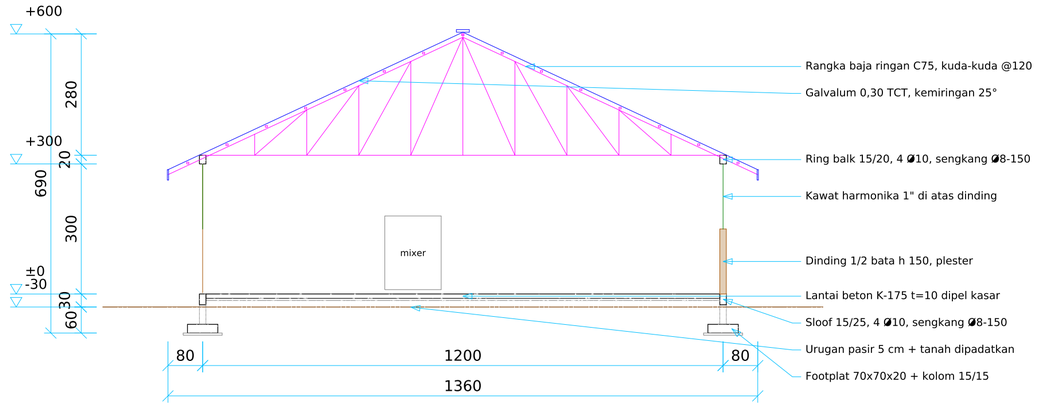

SPESIFIKASIDAN CATATAN

ALUR KERJA (garis merah putus-putus pada denah):
1. Jagung pipil kering dari gudang jagung masuk lewat pintu timur.
2. Digiling hammer mill + siklon (saringan 3-4 mm).
3. Ditimbang per resep (timbangan duduk 300 kg).
4. Dicampur di mixer horizontal 500 kg bersama dedak, bungkil, konsentrat, premix (±10 menit per batch).
5. Diisi karung 50 kg, dijahit, ditumpuk di palet, dibawa ke gudang pakan jadi lewat pintu utara.


Kebutuhan ±950 kg/hari = 2 batch mixer, ±2 jam kerja per hari.

• Struktur: footplat 70x70x20, kolom 15/15 (4 ◪10, ◪8-150), sloof 15/25, ring balk 15/20, beton K-225 (detail sama GT-01 K-05/K-06).

• Atap: rangka baja ringan C75 kuda-kuda @120, reng @ sesuai galvalum, galvalum 0,30 TCT, kemiringan 25°.
• Lantai: urugan tanah dipadatkan per 20 cm, pasir 5 cm, beton K-175 t=10.
• Dinding bata h 150 + kawat harmonika 1" sampai ring balk (ventilasi debu); R. premix & panel dinding penuh + pintu kunci.
• Pondasi mesin terpisah dari lantai (dilatasi 2 cm), detail B-09.
• Pintu geser 300 x 300 rangka hollow 40x40 + plat galvalum, rel atas + roda, celah bawah karet anti tikus.
• Listrik: PLN 3.500 VA cukup untuk mixer 2,2 kW + lampu; hammer mill memakai mesin diesel 16-24 PK.
Bila hammer mill memakai motor listrik 5,5 kW, daya PLN perlu dinaikkan ke ±7.700 VA.
• Lantai beton dipel kasar, peil +30, kemiringan 0,5% ke pintu agar mudah dibersihkan.


TAMPAK DEPAN (SELATAN)

skala 1 : 100

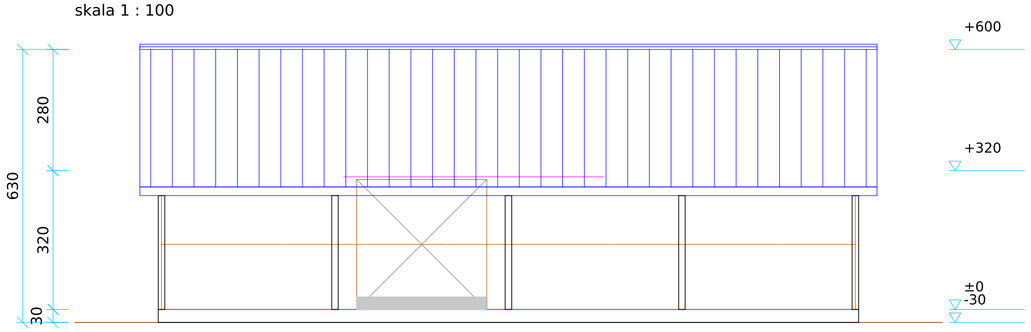

TAMPAK SAMPING (BARAT)


skala 1 : 100

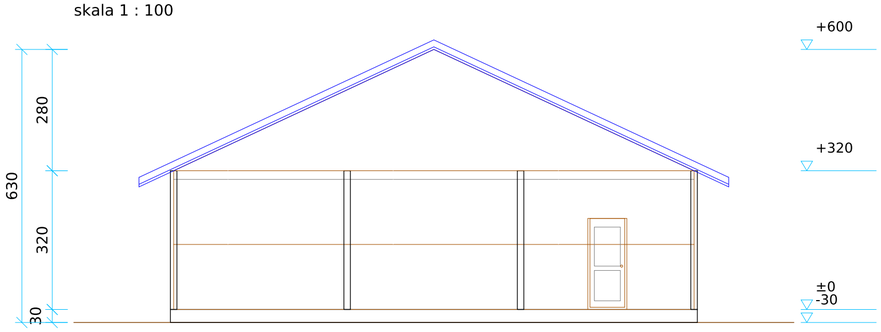

PROYEK	KERTAS A2
PETERNAKAN AYAM KUB PETELUR SEMI UMBARAN 10.000 EKOR ADEVA FARM - KAB. KONAWE SELATAN, SULAWESI TENGGARA	
JUDUL GAMBAR	
RUMAH PAKAN (OLAH & CAMPUR) 16 X 12 M	
CATATAN Satuan cm, elevasi terhadap lantai (±0). Periksa ulang oleh ahli sipil.	SKALA 1 : 100
TANGGAL OKTOBER 2026	STATUS GAMBAR PERENCANAAN
	NO. GAMBAR B-05


DENAH GUDANG PAKAN JADI

skala 1 : 100 · 20 x 10 m · lokasi tapak x 54 m, y 40 m dari pagar depan

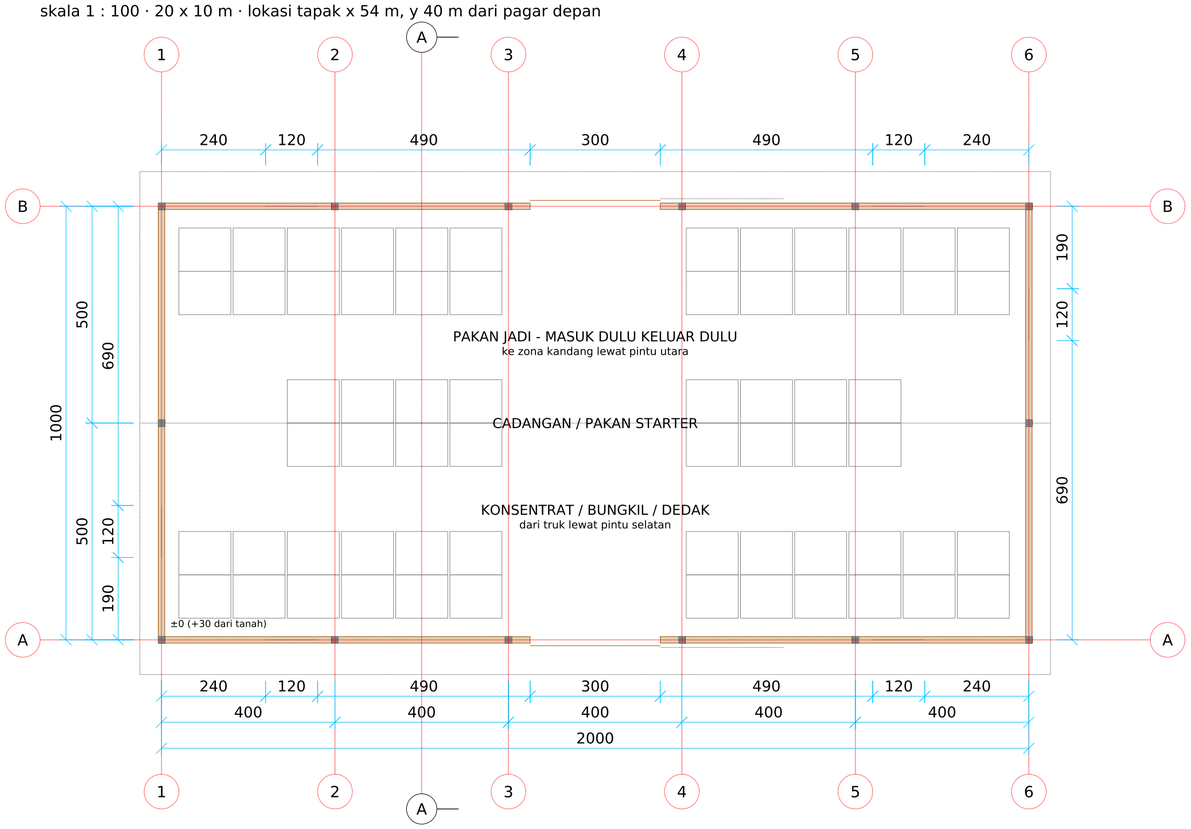

POTONGAN A-A

skala 1 : 100

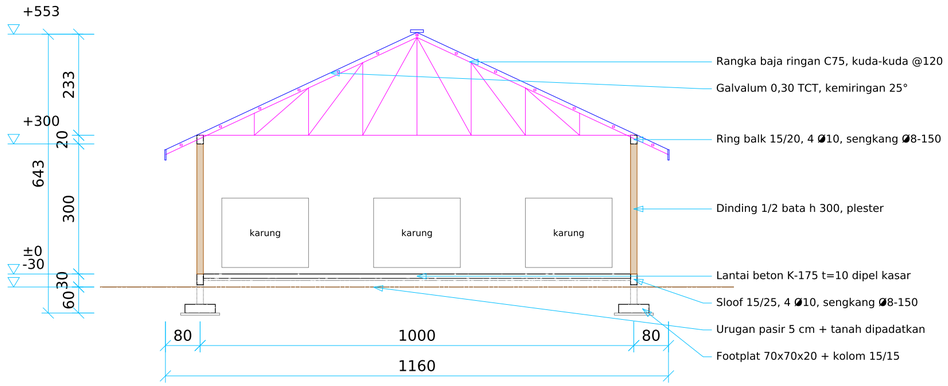

SPESIFIKASIDAN CATATAN

PENYIMPANAN:

- Palet kayu 120 x 100 x 15, jarak 50 cm dari dinding, maks. 10 karung (50 kg) per tumpukan.
- Kapasitas ±68 palet = ±34 ton = ±5 minggu kebutuhan pakan 950 kg/hari.
- Pakan jadi di baris utara (dekat pintu ke zona kandang), bahan baku di baris selatan.
- Masuk dulu keluar dulu: tulis tanggal produksi di setiap tumpukan.


BIOSEKURITI:

- Dinding utara gudang menjadi bagian pagar zona kandang (lihat MP-02).
- Pintu selatan diisi dari zona servis; pintu utara hanya dibuka dari dalam zona kandang.

- Struktur: footplat 70x70x20, kolom 15/15 (4 Ø10, Ø8-150), sloof 15/25, ring balk 15/20, beton K-225 (detail sama GT-01 K-05/K-06).
- Atap: rangka baja ringan C75 kuda-kuda @120, reng @ sesuai galvalum, galvalum 0,30 TCT, kemiringan 25°.
- Lantai: urugan tanah dipadatkan per 20 cm, pasir 5 cm, beton K-175 t=10.
- Dinding 1/2 bata penuh h 300, plester + aci sisi luar, plester sisi dalam.
- Ventilasi atas 120 x 60 (kawat ram + kasa) di +220 pada keempat sisi, anti burung dan tikus.
- Pintu geser 300 x 300 dengan karet bawah; plat seng 30 cm di kaki pintu (sekat tikus, B-10).
- Lantai peil +30, beton K-175 t=10, permukaan dipel halus agar mudah disapu.


TAMPAK DEPAN (SELATAN)

skala 1 : 100

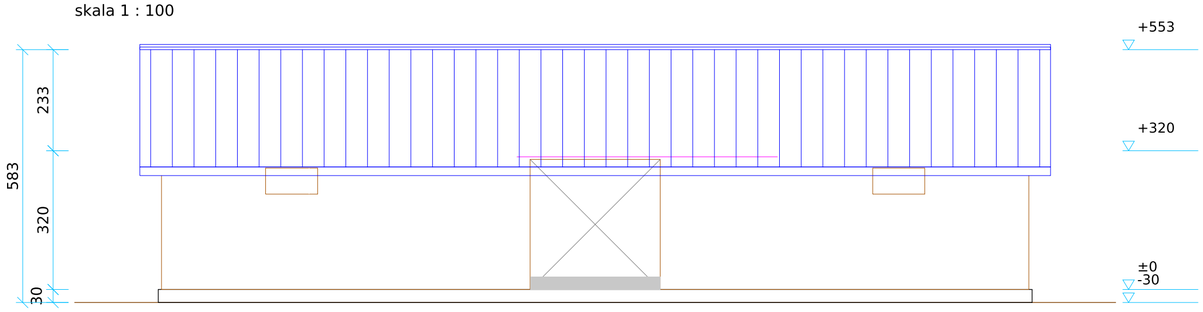

TAMPAK SAMPING (BARAT)


skala 1 : 100

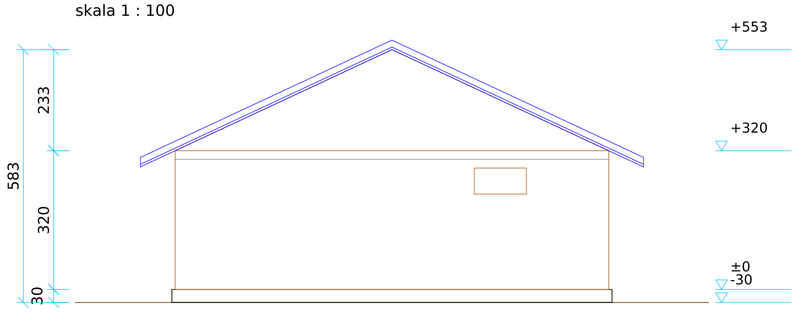

PROYEK PETERNAKAN AYAM KUB PETELUR SEMI UMBARAN 10.000 EKOR ADEVA FARM - KAB. KONAWE SELATAN, SULAWESI TENGGARA		KERTAS A2
JUDUL GAMBAR GUDANG PAKAN JADI 20 X 10 M		
CATATAN Satuan cm, elevasi terhadap lantai (±0). Periksa ulang oleh ahli sipil.		SKALA 1 : 100
TANGGAL OKTOBER 2026	STATUS GAMBAR PERENCANAAN	NO. GAMBAR B-06


DENAH RUMAH KOMPOS

skala 1 : 100 · 16 x 10 m · lokasi tapak x 78 m, y 213 m dari pagar depan

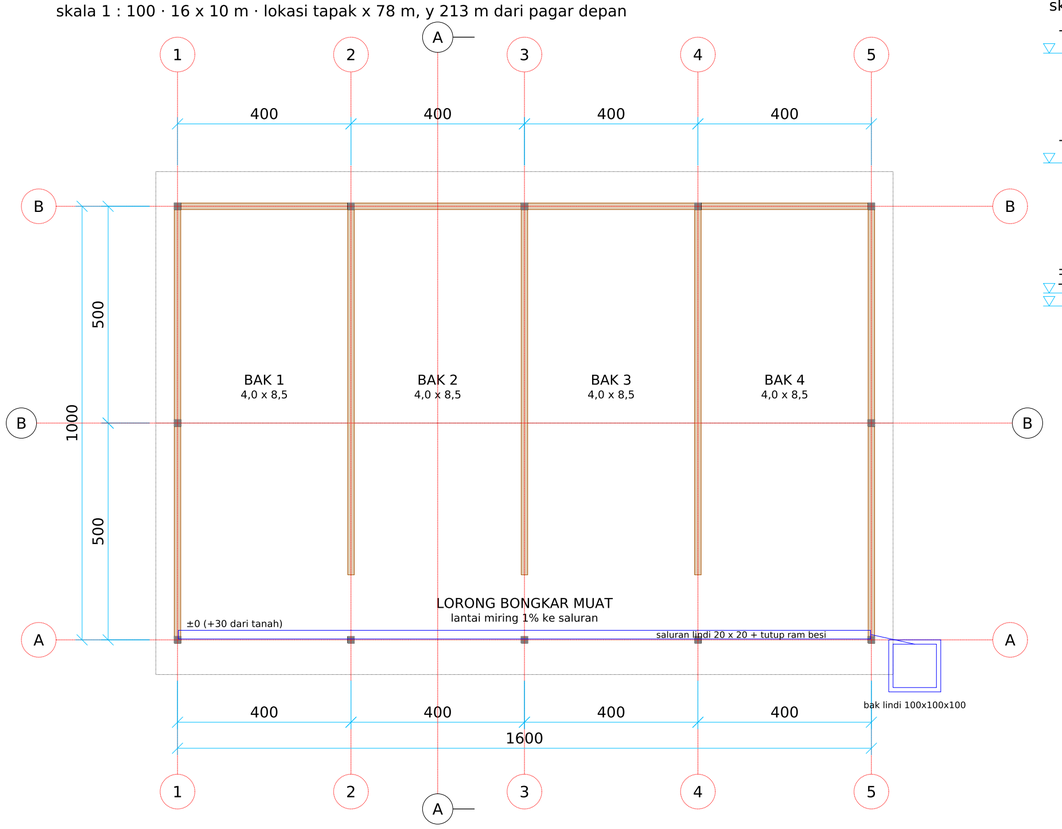

POTONGAN A-A

skala 1 : 100

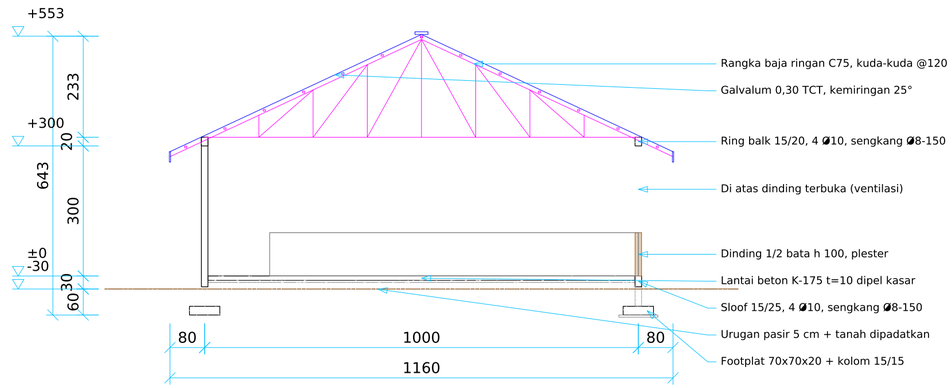

SPESIFIKASIDAN CATATAN

CARA KERJA:


• Kotoran + sekam dari kandang (±1,2-1,5 m³/hari) masuk bak 1 selama 1 minggu, tinggi maks. 1 m.
• Disiram dekomposer (EM4/trichoderma), kelembapan 50-60%, ditutup terpal.
• Tiap minggu tumpukan dipindah ke bak berikutnya (pembalikan); dari bak 4 kompos matang (±4 minggu).
• Kompos untuk kebun jagung dan indigofera; sebagian kotoran segar untuk pakan maggot BSF.

• Struktur: footplat 70x70x20, kolom 15/15 (4 Ø10, Ø8-150), sloof 15/25, ring balk 15/20, beton K-225 (detail sama GT-01 K-05/K-06).

• Atap: rangka baja ringan C75 kuda-kuda @120, reng @ sesuai galvalum, galvalum 0,30 TCT, kemiringan 25°.
• Sisi selatan terbuka penuh untuk gerobak; lorong depan 150 cm.
• Dinding keliling dan sekat bata h 100, plester kedap 1:3, di atasnya terbuka (ventilasi).
• Lantai beton K-175 t=10 miring 1% ke saluran lindi 20 x 20 bertutup ram besi di sisi depan.
• Saluran lindi ke bak lindi 100 x 100 x 100 di sudut tenggara (B-09); lindi disiram kembali ke tumpukan.
• Atap menutup penuh agar kompos tidak kehujanan; overstek 80.
• Jarak rumah kompos ke kandang terdekat ±10 m, ke sungai >100 m.


POTONGAN B-B (MEMANJANG MELALUI BAK)

skala 1 : 100 · tumpukan kompos dibalik tiap minggu ke bak berikutnya

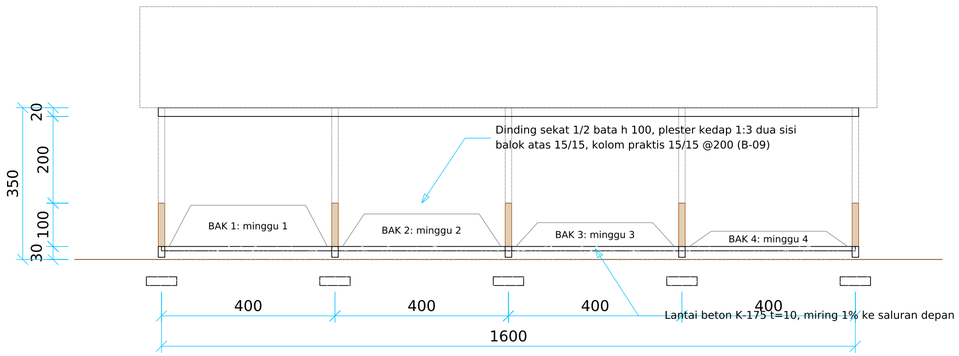

TAMPAK SAMPING (TIMUR)


skala 1 : 100

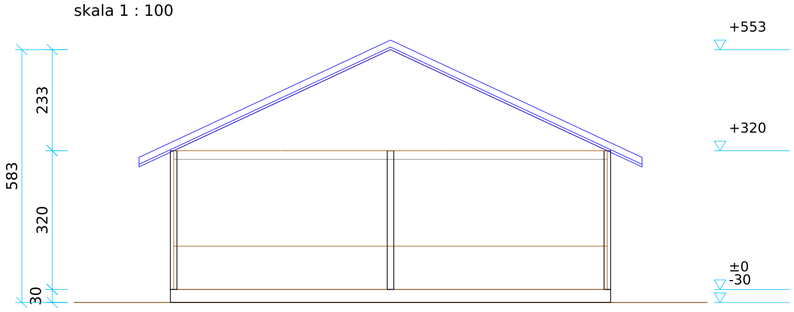

PROYEK	KERTAS A2
PETERNAKAN AYAM KUB PETELUR SEMI UMBARAN 10.000 EKOR ADEVA FARM - KAB. KONAWE SELATAN, SULAWESI TENGGARA	
JUDUL GAMBAR	
RUMAH KOMPOS 16 X 10 M (4 BAK BERGILIR)	
CATATAN Satuan cm, elevasi terhadap lantai (±0). Periksa ulang oleh ahli sipil.	SKALA 1 : 100
TANGGAL OKTOBER 2026	STATUS GAMBAR PERENCANAAN
	NO. GAMBAR B-07


DENAH RUMAH MAGGOT BSF

skala 1 : 50 · 12 x 8 m · lokasi tapak x 62 m, y 213 m dari pagar depan

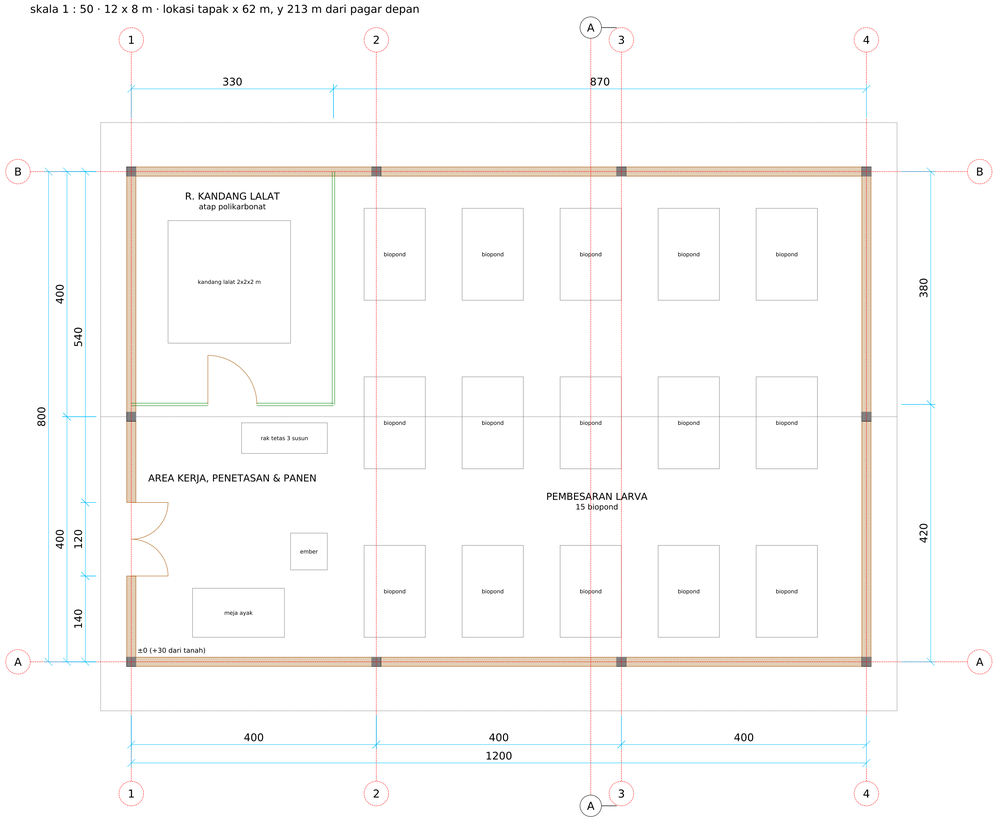


POTONGAN A-A

skala 1 : 50

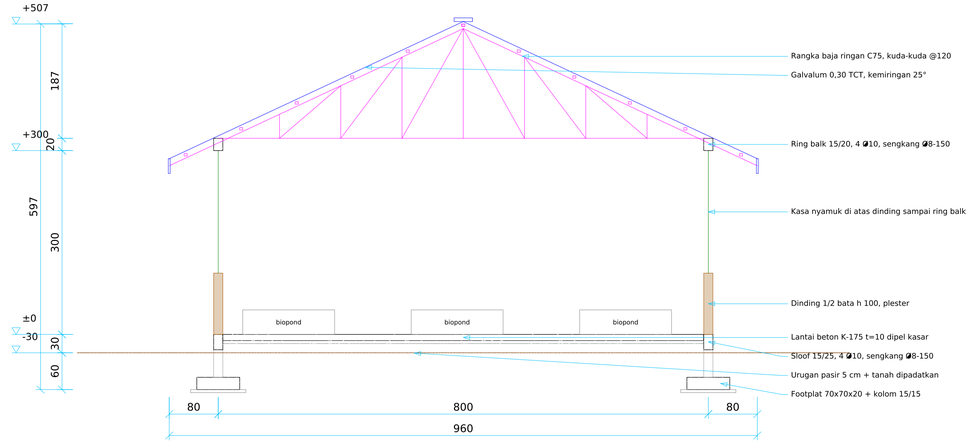

KANDANG LALAT BSF

1 : 50 · rangka kayu 5/5, kasa nyamuk

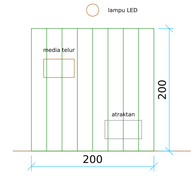


CARA KERJADAN SPESIFIKASI

SIKLUS: lalat kawin di kandang lalat -> telur di media kayu -> rak tetas (3-4 hari) -> larva kecil
ke biopond -> diberi kotoran ayam segar + limbah sayur/dedak 14-18 hari -> prepupa merayap naik
bidang miring ke talang -> sebagian dipanen untuk ayam, sebagian disisakan jadi lalat lagi.

- 15 biopond 100 x 150 (3 baris x 5), lorong 125; detail biopond B-09.
- Perkiraan panen maggot segar ±25-40 kg/hari setelah stabil (tambahan protein ayam).
- Dinding bata h 100 + kasa nyamuk sampai ring balk; pintu dua daun dengan tirai plastik.
- R. kandang lalat bersekat kasa, di atasnya 2 lembar atap polikarbonat (lalat BSF butuh cahaya).
- Struktur: footplat 70x70x20, kolom 15/15 (4 Ø10, Ø8-150), sloof 15/25, ring balk 15/20, beton K-225 (detail sama GT-01 K-05/K-06).
- Atap: rangka baja ringan C75 kuda-kuda @120, reng @ sesuai galvalum, galvalum 0,30 TCT, kemiringan 25°.
- Lantai beton K-175 t=10 dipel kasar, peil +30.
- Listrik: 4 titik lampu, 1 lampu LED khusus kandang lalat.


TAMPAK DEPAN (SELATAN)

skala 1 : 50

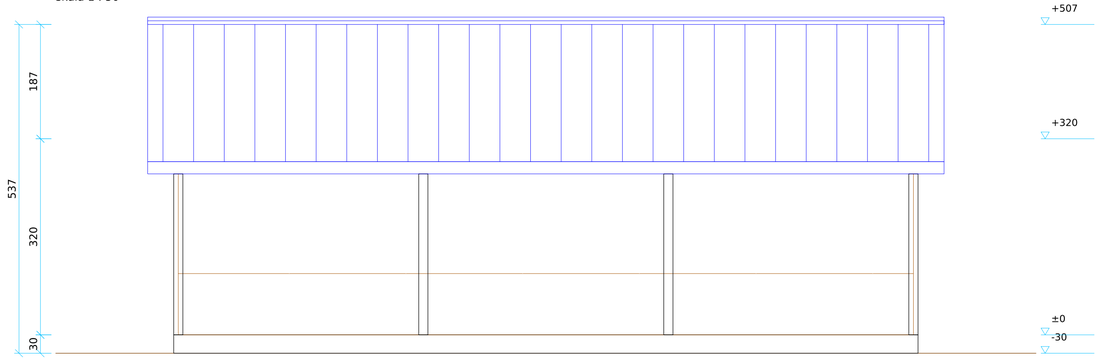

TAMPAK SAMPING (BARAT)


skala 1 : 50

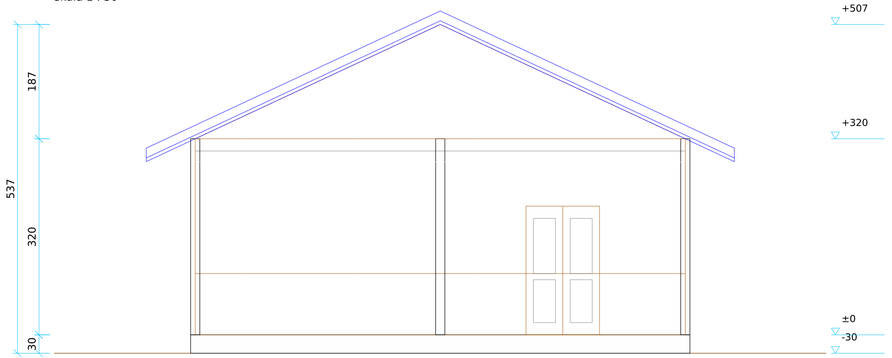

PROYEK: PETERNAKAN AYAM KUB PETELUR SEMI UMBARAN 10.000 EKOR ADEVA FARM - KAB. KONAWE SELATAN, SULAWESI TENGGARA			KERTAS A1
JUDUL GAMBAR: RUMAH MAGGOT BSF 12 X 8 M			
CATATAN: Satuan cm, elevasi terhadap lantai (±0). Periksa ulang oleh ahli sipil.		SKALA: 1 : 50	
TANGGAL: OKTOBER 2026	STATUS: GAMBAR PERENCANAAN		NO. GAMBAR: B-08


A. DETAIL PONDASI MESIN

skala 1 : 20 · rumah pakan B-05

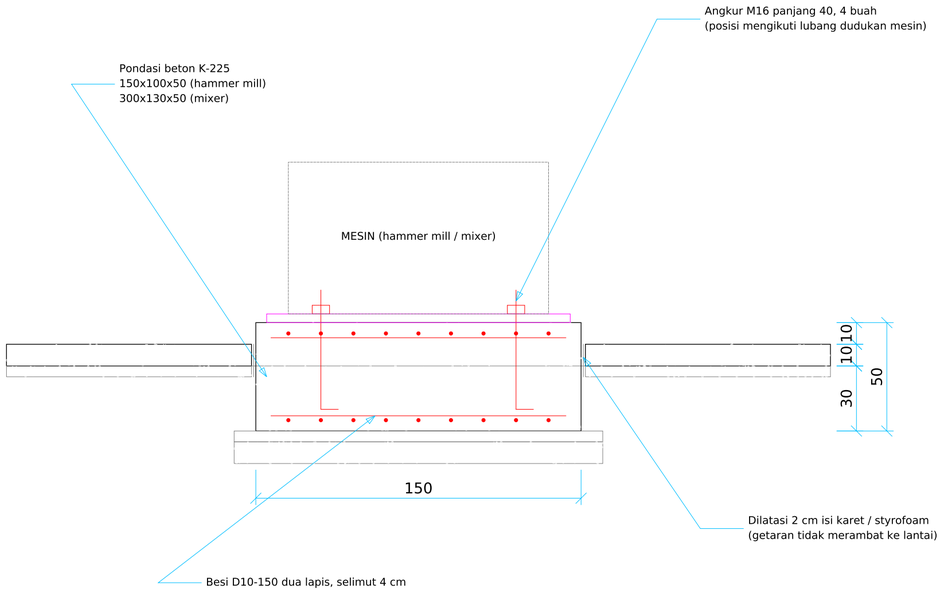


B. DETAIL SALURAN DAN BAK LINDI

skala 1 : 20 · rumah kompos B-07

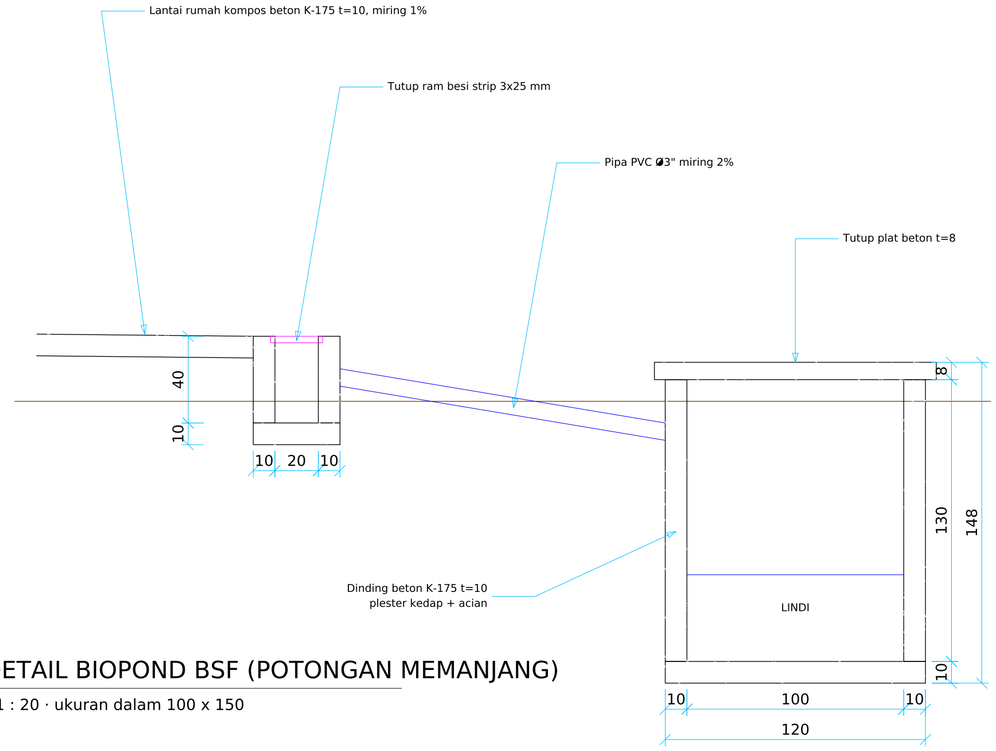


C. DETAIL DINDING SEKAT BAK KOMPOS

skala 1 : 20

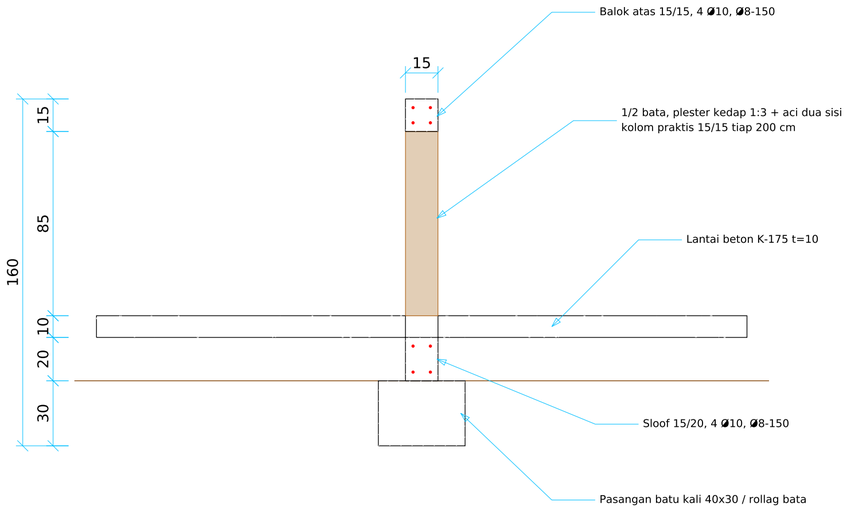


D. DETAIL BIOPOND BSF (POTONGAN MEMANJANG)

skala 1 : 20 · ukuran dalam 100 x 150

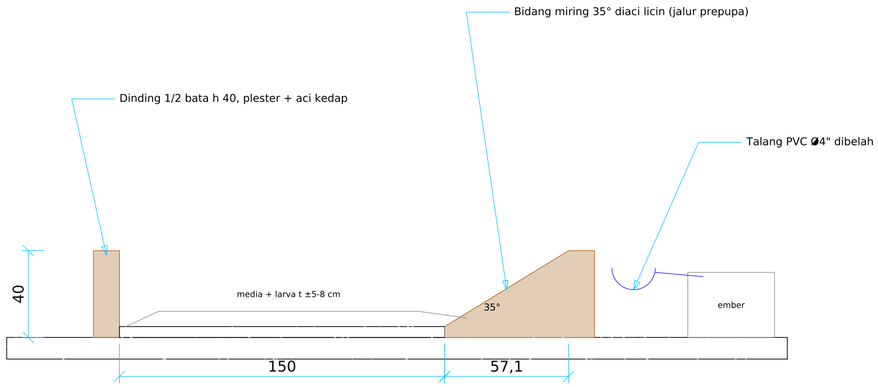


PROYEK	KERTAS A2
PETERNAKAN AYAM KUB PETELUR SEMI UMBARAN 10.000 EKOR ADEVA FARM - KAB. KONAWE SELATAN, SULAWESI TENGGARA	
JUDUL GAMBAR	
DETAIL RUMAH PAKAN, RUMAH KOMPOS DAN BIOPOND BSF	
CATATAN Satuan cm, elevasi terhadap lantai (±0). Periksa ulang oleh ahli sipil.	SKALA 1 : 20
TANGGAL OKTOBER 2026	STATUS GAMBAR PERENCANAAN
	NO. GAMBAR B-09

P1

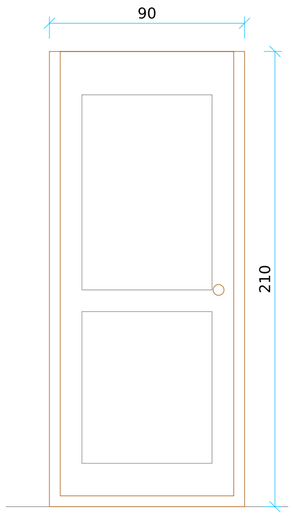


Pintu panel kayu 90x210
kusen 6/12 kayu kelas II
engsel 3 bh, kunci tanam

P2

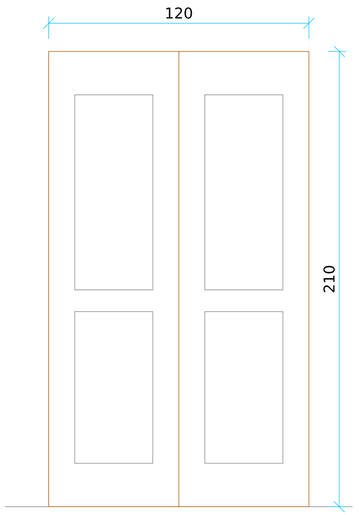


Pintu dua daun 120x210
(rumah telur, BSF)

J1

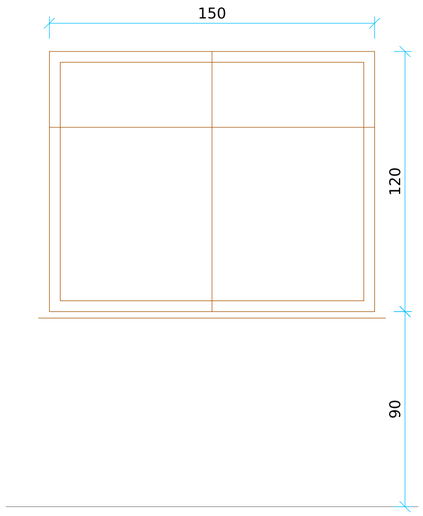


Jendela aluminium kaca 5 mm
150x120, boven kaca mati
(lebar 100/120 = J2/J3)

BV

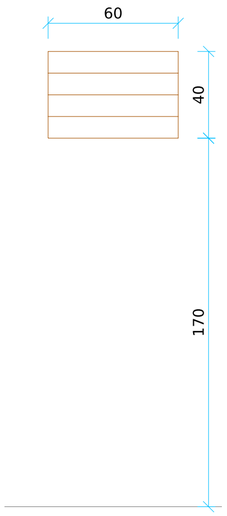


Boven/ventilasi KM 40-60x40
kaca nako / jalusi

PALET KAYU 120 x 100 x 15

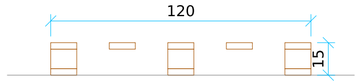

Papan 12/2,5 kayu kelas III diawetkan,
balok 9/12; tumpukan maks. 10 karung


SEKAT TIKUS: plat seng/galvalum
30 cm di kaki dinding & kusen
pintu gudang, celah bawah
pintu karet ≤ 1 cm

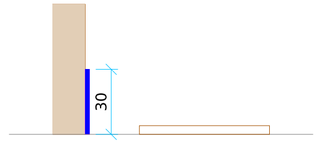

SEPTIC TANK BIOFIL + RESAPAN


tanpa skala (skematik)

Septic tank biofil pabrikan 1 m³ (mes 2 m³)
Resapan 100x100x120: ijuk, kerikil, pasir;
jarak ≥10 m dari sumur bor

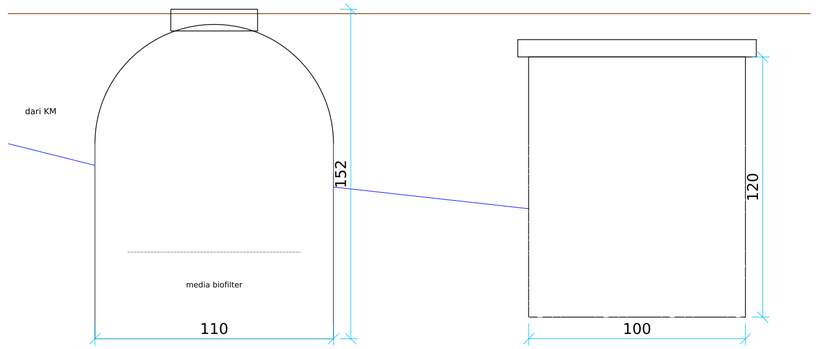


MEJA SORTIR TELUR 240 x 100 x 80

skala 1 : 20 · R. sortir B-04

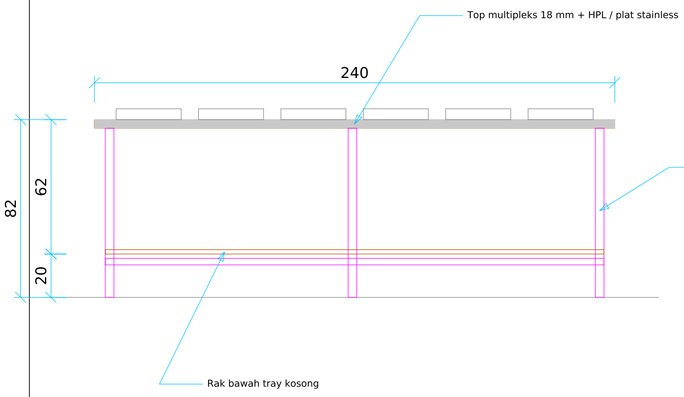

RAK EGG TRAY 300 x 50 x 180

skala 1 : 20 · R. simpan B-04

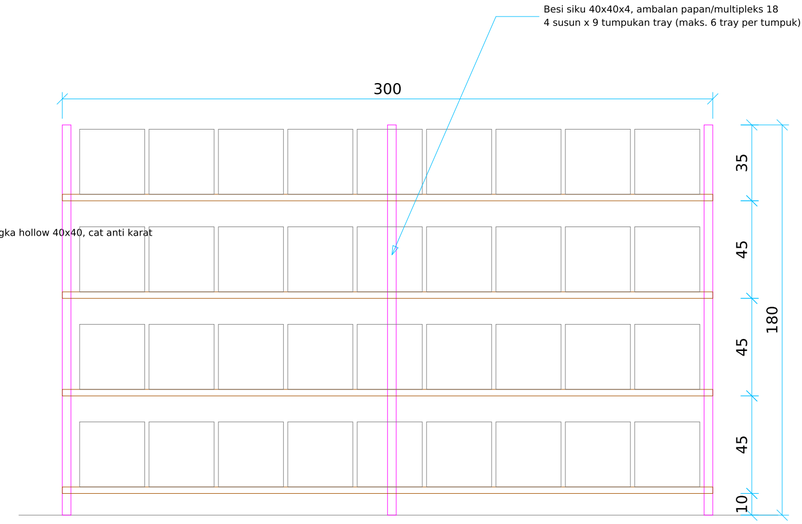

PROYEK	KERTAS A2
PETERNAKAN AYAM KUB PETELUR SEMI UMBARAN 10.000 EKOR ADEVA FARM - KAB. KONAWE SELATAN, SULAWESI TENGGARA	
JUDUL GAMBAR	
DAFTAR KUSEN, MEJA SORTIR & RAK TELUR, PALET, SEPTIC TANK BIOFIL	
CATATAN Satuan cm, elevasi terhadap lantai (±0). Periksa ulang oleh ahli sipil.	SKALA 1 : 20
TANGGAL OKTOBER 2026	STATUS GAMBAR PERENCANAAN
	NO. GAMBAR B-10