
Masterplan Pemanfaatan Lahan 4 Ha (Semi Umbaran)


Zona kandang semi umbaran 1,6 ha untuk 10.000 ekor, kebun pakan dan unit pengolahan pakan 2,4 ha. Pagar kawat harmonika keliling lahan, zona kandang, dan tiap petak umbaran.

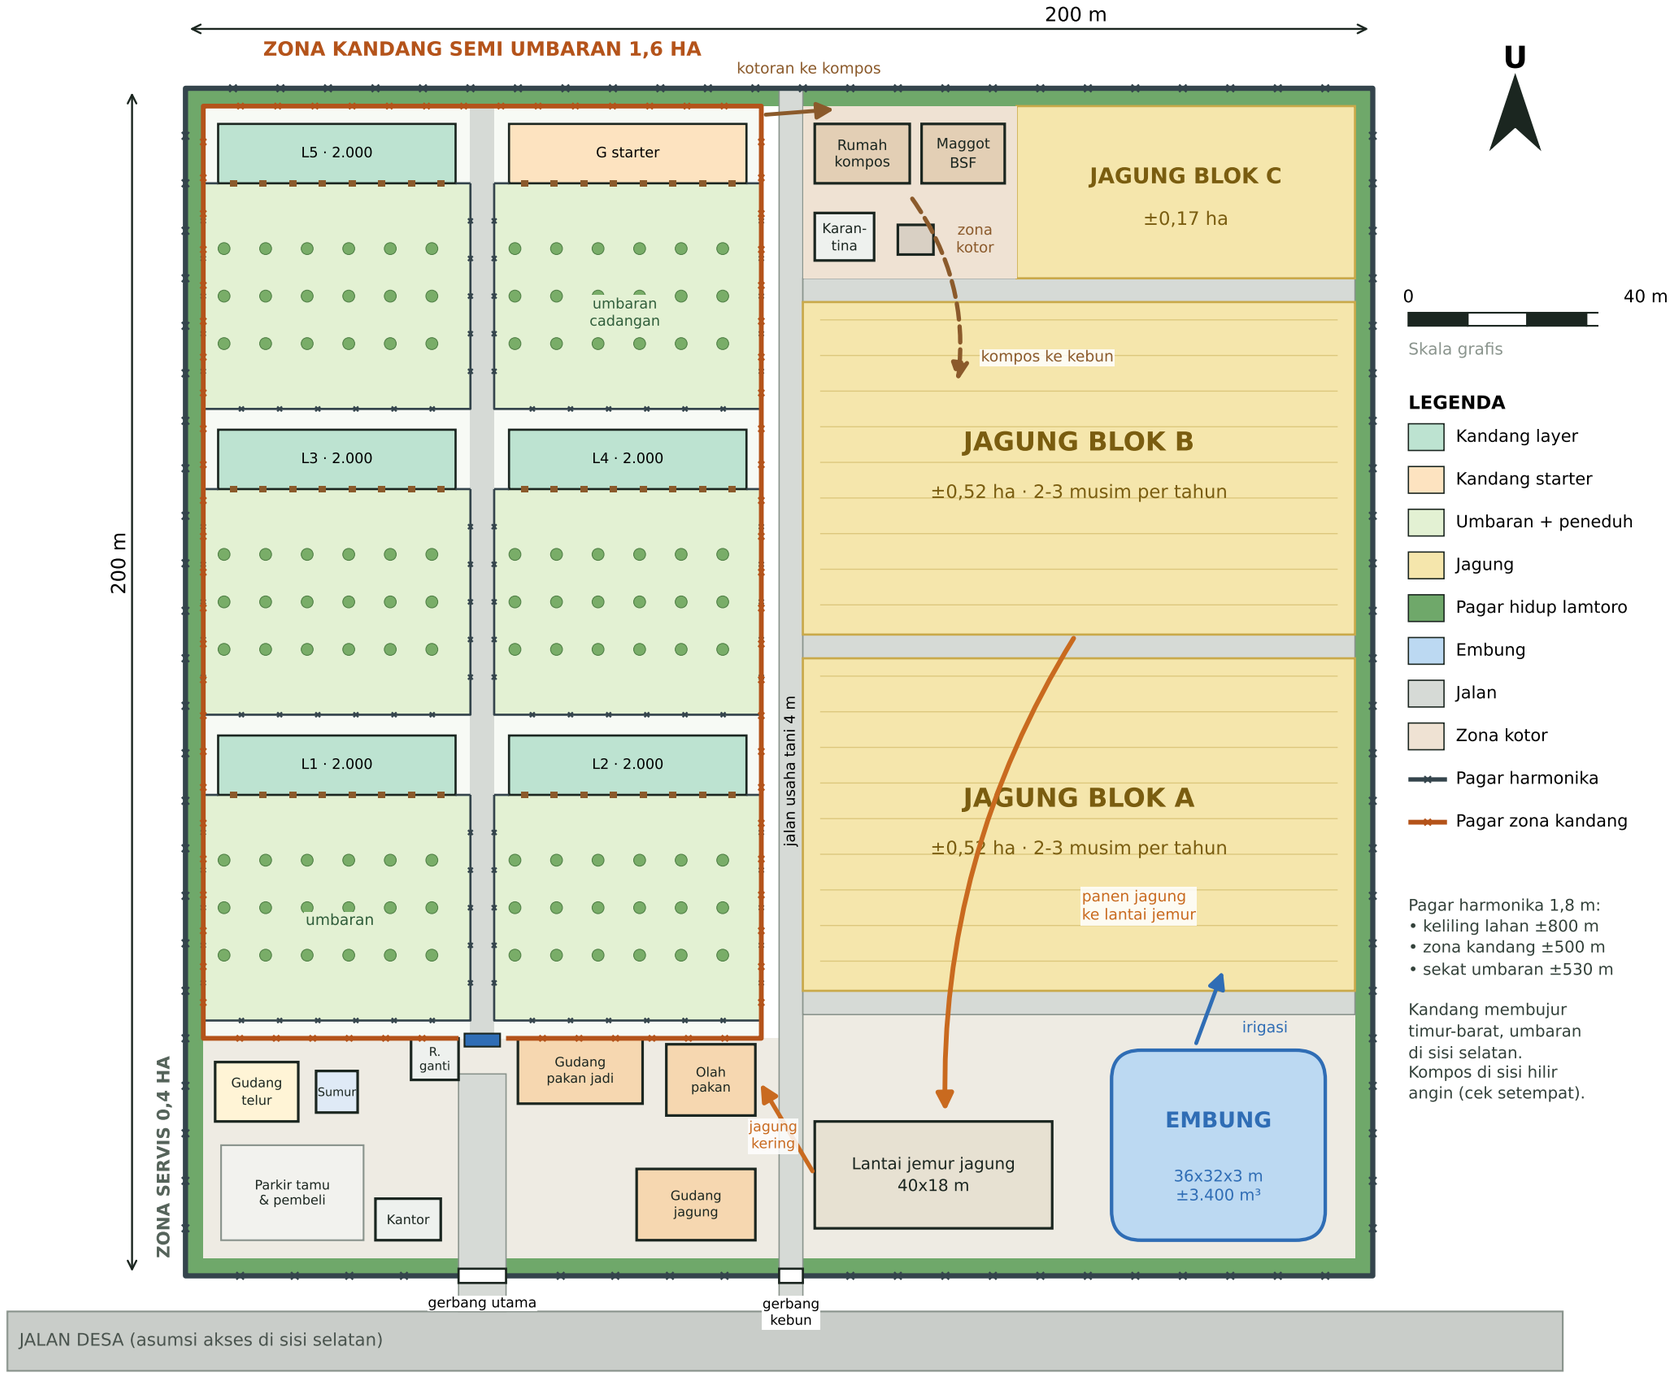

PROYEK	NO. GAMBAR	STATUS
Masterplan Lahan 4 Ha Adeva Farm - Ayam KUB Petelur 10.000 ekor - Kab. Konawe Selatan	**MP-01**	Rencana awal. Bentuk lahan diasumsikan persegi 200 x 200 m, sesuaikan dengan lahan asli.

Zona Kandang Semi Umbaran 1,6 Ha + Zona Servis

Tiap kandang postal 10 x 40 m (2.000 ekor) punya petak umbaran 45 x 38 m berpagar harmonika dan berpohon peneduh. Umbaran kandang starter dipakai sebagai petak cadangan untuk digilir.

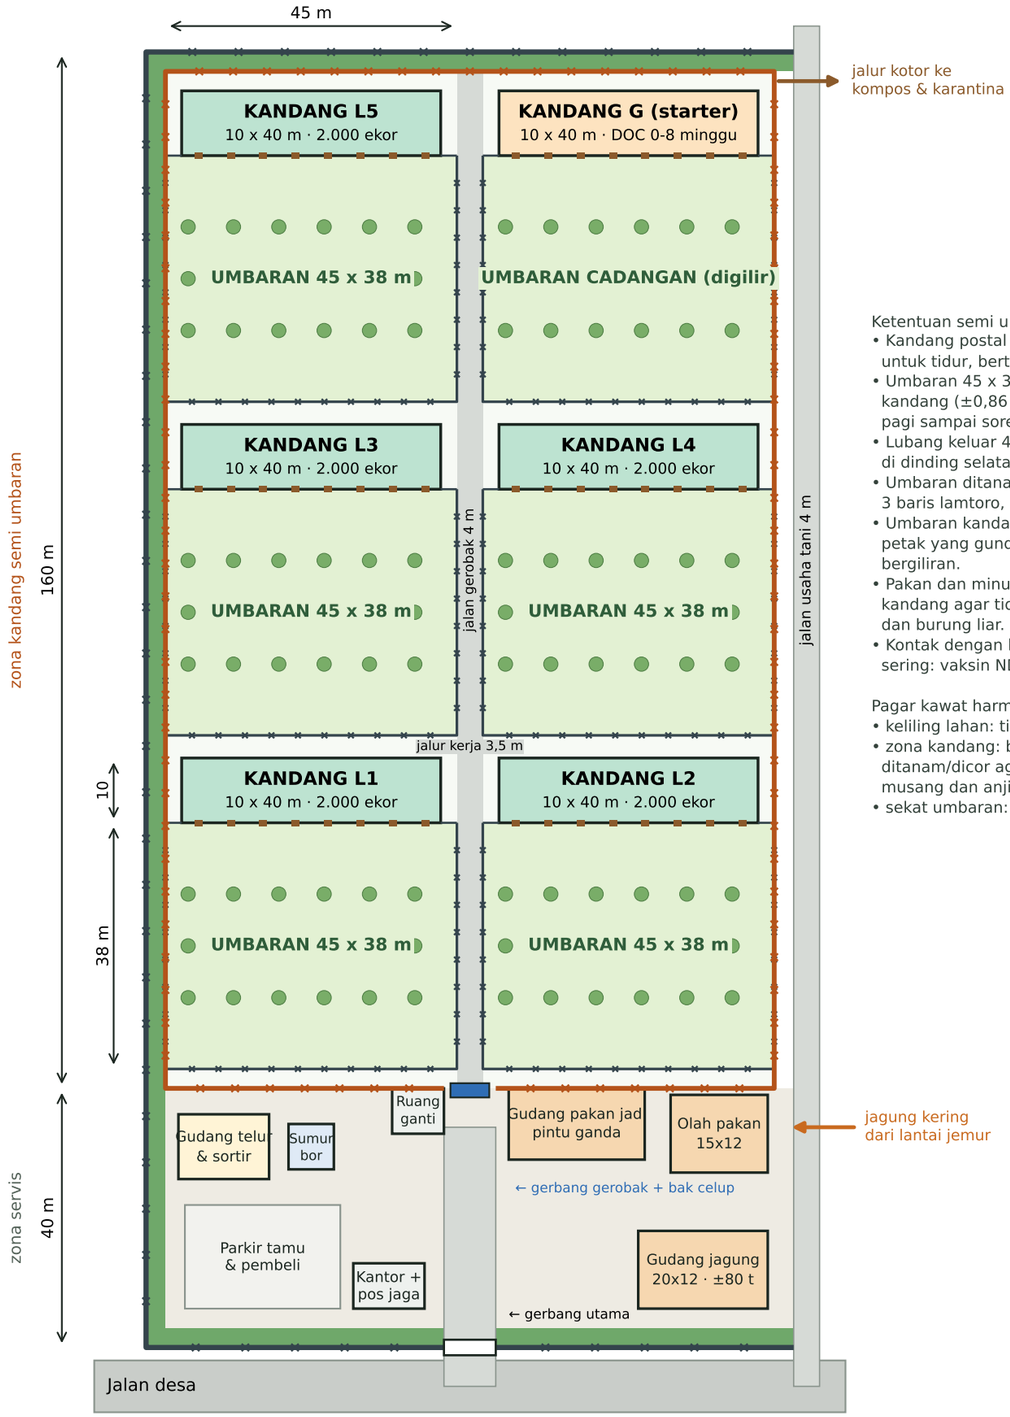

Ketentuan semi umbaran:
- Kandang postal 10 x 40 m, 5 ekor/m², untuk tidur, bertelur, dan makan.
- Umbaran 45 x 38 m = 1.710 m² per kandang (±0,86 m²/ekor), dibuka pagi sampai sore.
- Lubang keluar 40 x 45 cm tiap 5 m di dinding selatan, ditutup malam.
- Umbaran ditanami rumput/legum + 3 baris lamtoro, indigofera, gamal.
- Umbaran kandang G jadi petak cadangan: petak yang gundul diistirahatkan bergiliran.
- Pakan dan minum tetap di dalam kandang agar tidak mengundang tikus dan burung liar.
- Kontak dengan burung liar lebih sering: vaksin ND dan AI teratur.

Pagar kawat harmonika 1,8 m:
- keliling lahan: tiang beton tiap 2,5 m
- zona kandang: bagian bawah 30 cm ditanam/dicor agar tidak digali musang dan anjing
- sekat umbaran: tiang kayu/bambu

PROYEK	NO. GAMBAR	STATUS
Masterplan Lahan 4 Ha Adeva Farm - Ayam KUB Petelur 10.000 ekor - Kab. Konawe Selatan	**MP-02**	Rencana awal. Bentuk lahan diasumsikan persegi 200 x 200 m, sesuaikan dengan lahan asli.


Neraca Lahan, Alur Pakan, dan Perkiraan Penghematan (Semi Umbaran)

Perkiraan untuk 10.000 ekor dengan racikan T2 (jagung 60%). Angka produksi dan biaya adalah taksiran perencanaan.

A. Neraca pemanfaatan lahan

Pemanfaatan	m²	ha	porsi
Kandang (6 unit 10 x 40 m)	2.400	0,24	6%
Umbaran berpohon peneduh (6 x 45 x 38 m)	10.260	1,03	26%
Jalan, jalur kerja, pagar hidup zona kandang	3.340	0,33	8%
Zona servis (kantor, gudang, olah pakan)	4.000	0,40	10%
Jagung blok A, B, C	12.070	1,21	30%
Lantai jemur, embung, halaman kebun	3.810	0,38	9%
Zona kotor (kompos, maggot BSF, karantina)	1.040	0,10	3%
Jalan usaha tani dan pagar hidup kebun	3.080	0,31	8%
Total	**40.000**	**4,00**	**100%**

B. Alur sirkular: kotoran jadi pupuk, kebun jadi pakan

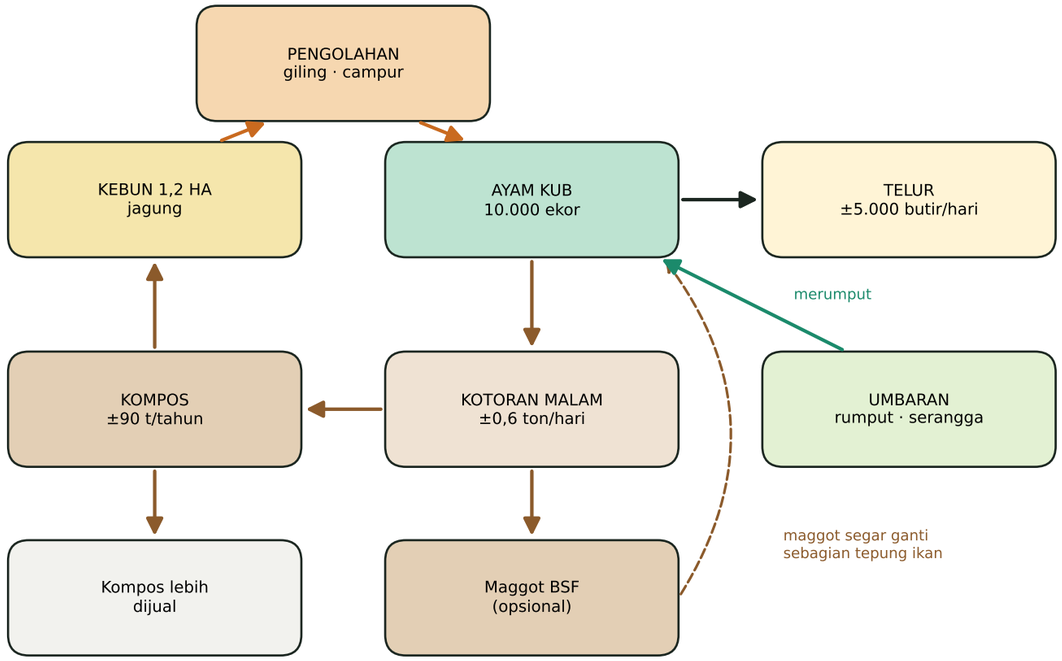

Jagung dari petani sekitar dibeli saat panen raya, disimpan di gudang jagung (±80 t), lalu diolah bersama hasil kebun sendiri.

C. Perkiraan hasil dan penghematan per tahun

Sumber	Hasil	Keterangan	Manfaat
Jagung kebun 1,2 ha, 2-3 musim	13-17 t	6-8% kebutuhan	Rp 56-70 jt
Ayam merumput di umbaran	3-5% pakan	rumput, serangga	Rp 75-125 jt
Lamtoro & indigofera (tepung daun)	±1,5 t	pagar hidup	Rp 5 jt
Kompos dari kotoran malam	±90 t	jual ±75 t	Rp 45-47 jt
Maggot BSF segar (opsional)	±10 t	ganti ±10% t. ikan	Rp 15-25 jt
Beli jagung panen raya + gudang	±120 t	Rp 5.000 vs 6.500	Rp 180 jt
Total manfaat			**Rp 376-452 jt**

Kebutuhan jagung 10.000 ekor ±208 t/tahun. Biaya pakan racikan ±Rp 2,5 miliar/tahun, jadi manfaat di atas setara ±15-18% biaya pakan. Tanpa strategi gudang jagung: Rp 196-272 juta (±8-11%). Hemat dari merumput hanya tercapai bila umbaran ditanami rumput/legum dan digilir; kalau umbaran gundul, anggap nol. Sebagian kotoran jatuh di umbaran, jadi kompos lebih sedikit.

D. Perkiraan investasi pagar, kebun, dan pengolahan pakan

Komponen	Biaya
Embung 36x32x3 m (alat berat, tanpa geomembran)	Rp 60-90 jt
Sumur bor, pompa, pipa irigasi	Rp 40-60 jt
Bangunan pengolahan pakan 15x12 m	Rp 90-110 jt
Mesin: hammer mill, mixer 500 kg, pemipil, timbangan	Rp 60-75 jt
Gudang jagung 20x12 m + palet	Rp 150-180 jt
Lantai jemur 40x18 m	Rp 65-85 jt
Hand traktor dan alat tani	Rp 16 jt

Komponen	Biaya
Pagar harmonika keliling lahan ±800 m (tiang beton)	Rp 80-104 jt
Pagar harmonika zona kandang ±500 m	Rp 50-65 jt
Pagar sekat umbaran ±530 m (tiang kayu)	Rp 37-48 jt
Peneduh, rumput, lamtoro, gamal	Rp 8-12 jt
Rumah kompos 16x10 m	Rp 45-60 jt
Unit maggot BSF (opsional)	Rp 25-40 jt
Total	**Rp 726-945 jt**
Balik modal (manfaat Rp 376-452 jt/th)	**±1,6-2,5 tahun**

Harga pagar harmonika 1,8 m dihitung Rp 100-130 ribu/m terpasang dengan tiang beton, Rp 70-90 ribu/m dengan tiang kayu. Belum termasuk modal kerja stok jagung (±Rp 300 juta) dan bangunan kandang (RAB hemat ±Rp 1,78 miliar).

PROYEK

Masterplan Lahan 4 Ha Adeva Farm - Ayam KUB Petelur 10.000 ekor - Kab. Konawe Selatan

NO. GAMBAR

MP-03

STATUS

Rencana awal. Bentuk lahan diasumsikan persegi 200 x 200 m, sesuaikan dengan lahan asli.