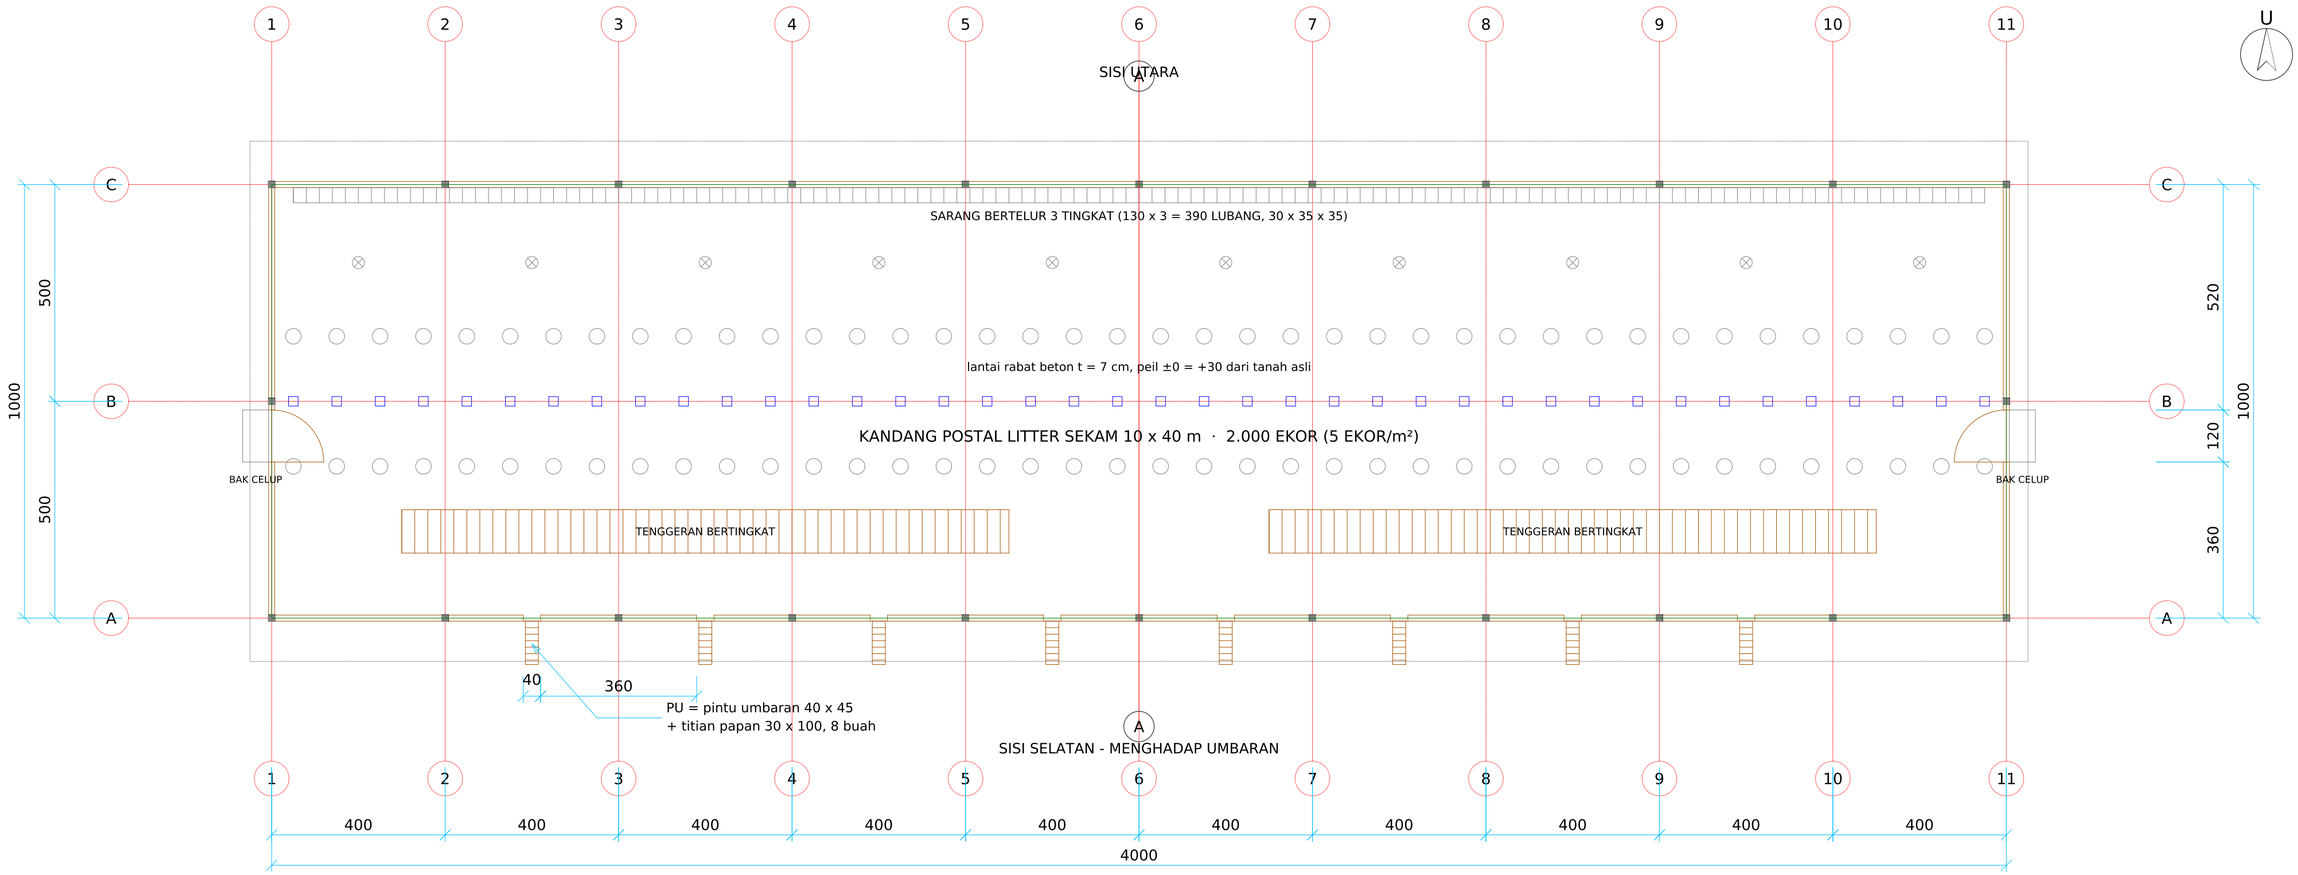



LEGENDA

- Tempat pakan gantung 7-10 kg (80 buah)
- Tempat minum galon 5 liter (40 buah)
- Lampu LED 15 W (10 titik)
- Kolom beton 15 x 15 (24 buah)
- Kawat harmonika 1" galvanis

SPESIFIKASI UMUM

1. Kandang membujur timur-barat, sisi selatan menghadap umbaran 45 x 38 m.
2. Struktur: footplat 70x70x20, kolom 15/15, sloof 15/25, ring balk 15/20, beton K-225.
3. Dinding bata merah 1/2 bata tinggi 50 cm, plester + aci dua sisi.
4. Di atas dinding: kawat harmonika galvanis 1" tinggi 200 cm pada rangka hollow 40x40.
5. Tirai terpal sisi panjang dan sisi pendek, digulung dari bawah dengan tali dan katrol.
6. Atap rangka baja ringan C75 jarak 120, penutup galvalum 0,30 TCT, atap monitor (celah 40 cm).
7. Lantai rabat beton K-175 t = 7 cm di atas pasir 5 cm dan urugan tanah dipadatkan.
8. Pintu umbaran 40 x 45 cm (8 buah) dibuka pagi, ditutup sore hari.
9. Lihat K-04 potongan, K-05 s/d K-09 detail.

PROYEK PETERNAKAN AYAM KUB PETELUR SEMI UMBARAN 10.000 EKOR ADEVA FARM - KAB. KONAWE SELATAN, SULAWESI TENGGARA		KERTAS A2
JUDUL GAMBAR DENAH KANDANG POSTAL SEMI UMBARAN		
CATATAN Satuan cm, elevasi terhadap lantai (±0). Periksa ulang oleh ahli sipil.		SKALA 1 : 100
TANGGAL OKTOBER 2026	STATUS GAMBAR PERENCANAAN	NO. GAMBAR K-01

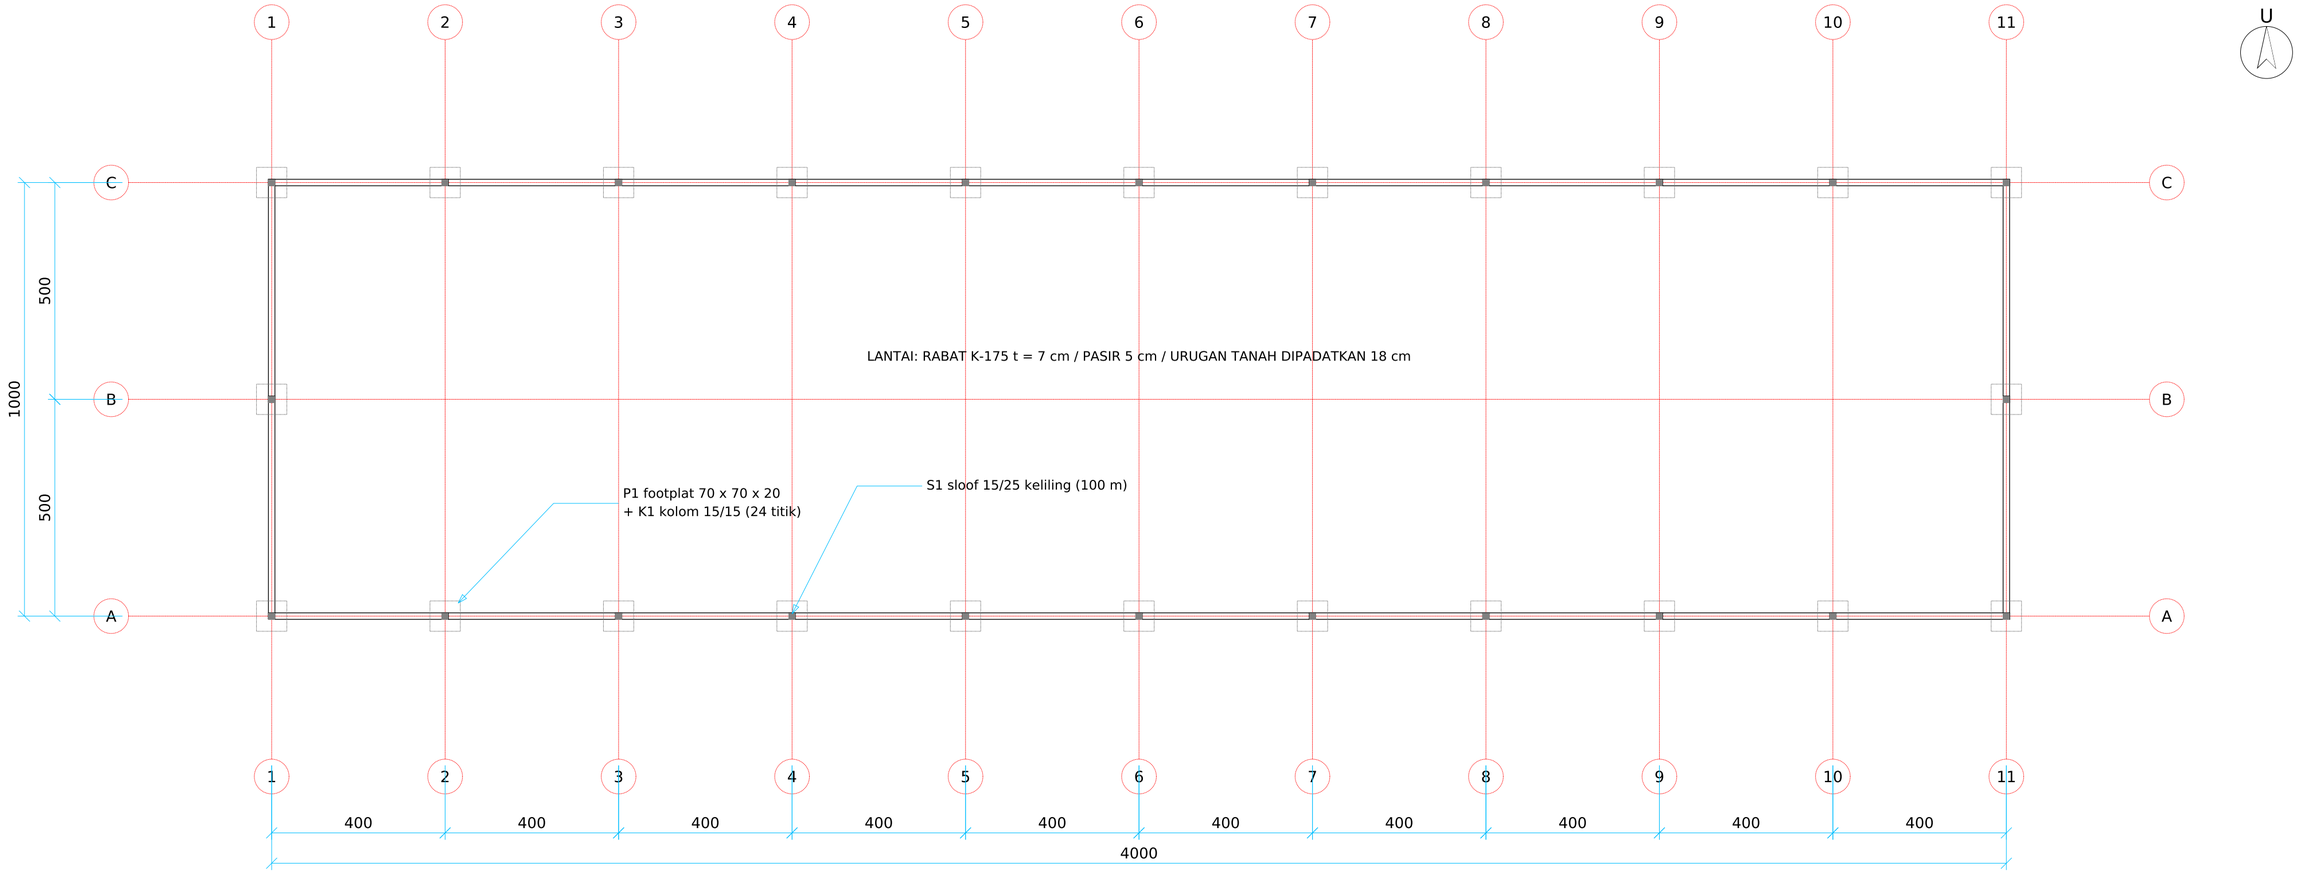

TABEL ELEMEN STRUKTUR

KODE	ELEMEN / UKURAN (cm)	PENULANGAN	MUTU	JUMLAH
P1	Footplat 70 x 70 x 20	D10 - 150 dua arah, selimut 5	K-225	24 bh
K1	Kolom 15 x 15, tinggi ±320	4 D10, sengkang ⌀8-150 (⌀8-100 ujung 50)	K-225	24 bh
S1	Sloof 15 x 25	4 D10, sengkang ⌀8-150	K-225	100 m'
RB	Ring balk 15 x 20	4 D10, sengkang ⌀8-150	K-225	100 m'
LK	Lantai kerja t = 5 di bawah P1	-	K-100	24 bh
LT	Lantai rabat t = 7	-	K-175	392 m²

Besi D = ulir BJTS 420, ⌀ = polos BJTP 280. Overlap sambungan 40 D. Stek kolom ke footplat ditekuk 10 cm. Selimut beton: footplat 5 cm, kolom/sloof/ring balk 2,5 cm.

PROYEK
PETERNAKAN AYAM KUB PETELUR SEMI UMBARAN 10.000 EKOR
ADEVA FARM - KAB. KONAWE SELATAN, SULAWESI TENGGARA

KERTAS A2

JUDUL GAMBAR
DENAH PONDASI, SLOOF DAN KOLOM

CATATAN
Satuan cm, elevasi terhadap lantai (±0).
Periksa ulang oleh ahli sipil.

SKALA
1 : 100


TANGGAL
OKTOBER 2026

STATUS
GAMBAR PERENCANAAN

NO. GAMBAR
K-02


TAMPAK SELATAN (SISI UMBARAN)

skala 1 : 100

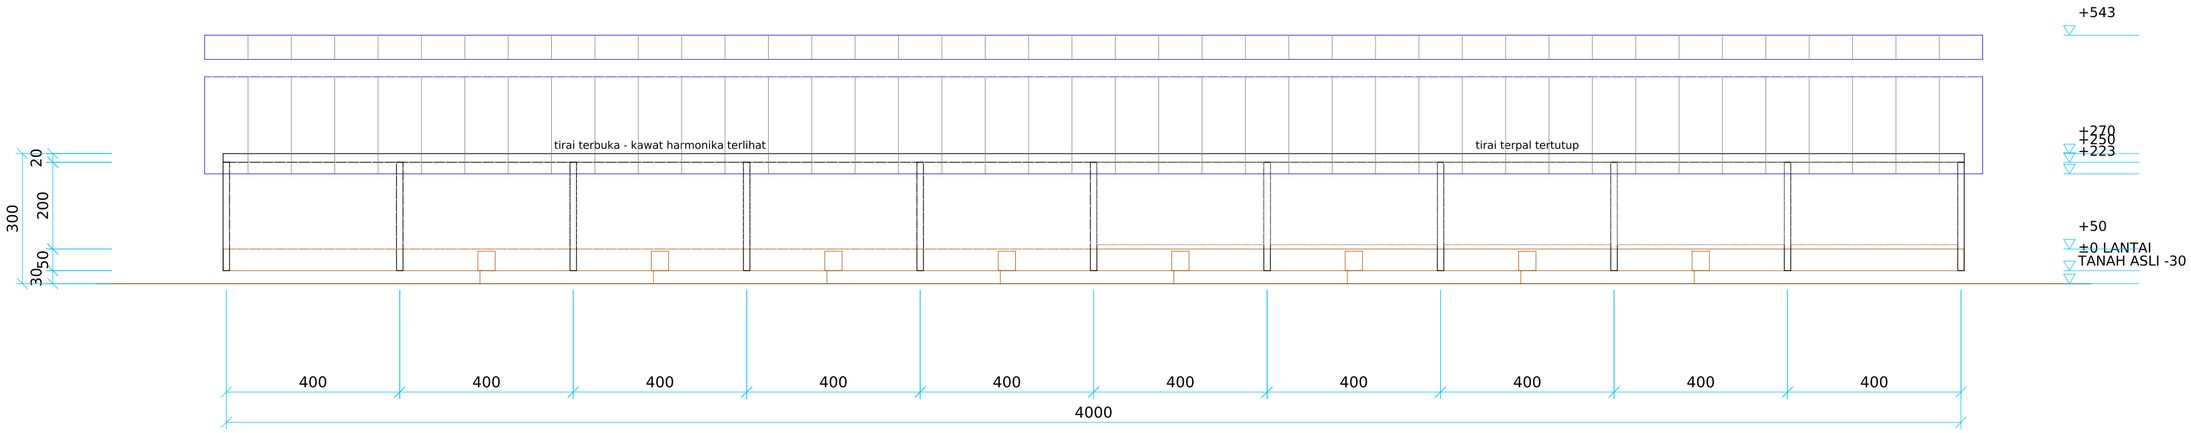

TAMPAK BARAT (SISI PINTU)

skala 1 : 100 · tampak timur sama

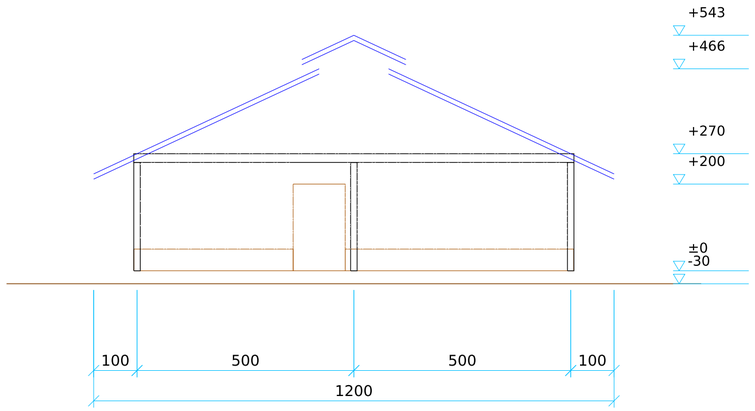


CATATAN TAMPAK

- Bidang segitiga di bawah atap (gevel) ditutup kawat harmonika 1".
- Celah atap monitor 40 cm ditutup kawat harmonika agar burung liar tidak masuk.
- Tirai terpal dipasang di sisi luar, digulung dari bawah; buka pagi-siang, tutup malam dan saat hujan angin.
- Dinding bata dicat kapur/cat tembok putih di kedua sisi.
- Pintu umbaran 40 x 45 cm hanya di sisi selatan.

PROYEK PETERNAKAN AYAM KUB PETELUR SEMI UMBARAN 10.000 EKOR ADEVA FARM - KAB. KONAWE SELATAN, SULAWESI TENGGARA		KERTAS A2
JUDUL GAMBAR TAMPAK SELATAN DAN TAMPAK BARAT		
CATATAN Satuan cm, elevasi terhadap lantai (±0). Periksa ulang oleh ahli sipil.		SKALA 1 : 100
TANGGAL OKTOBER 2026	STATUS GAMBAR PERENCANAAN	NO. GAMBAR K-03

POTONGAN A-A


skala 1 : 50 · dipotong pada as 6

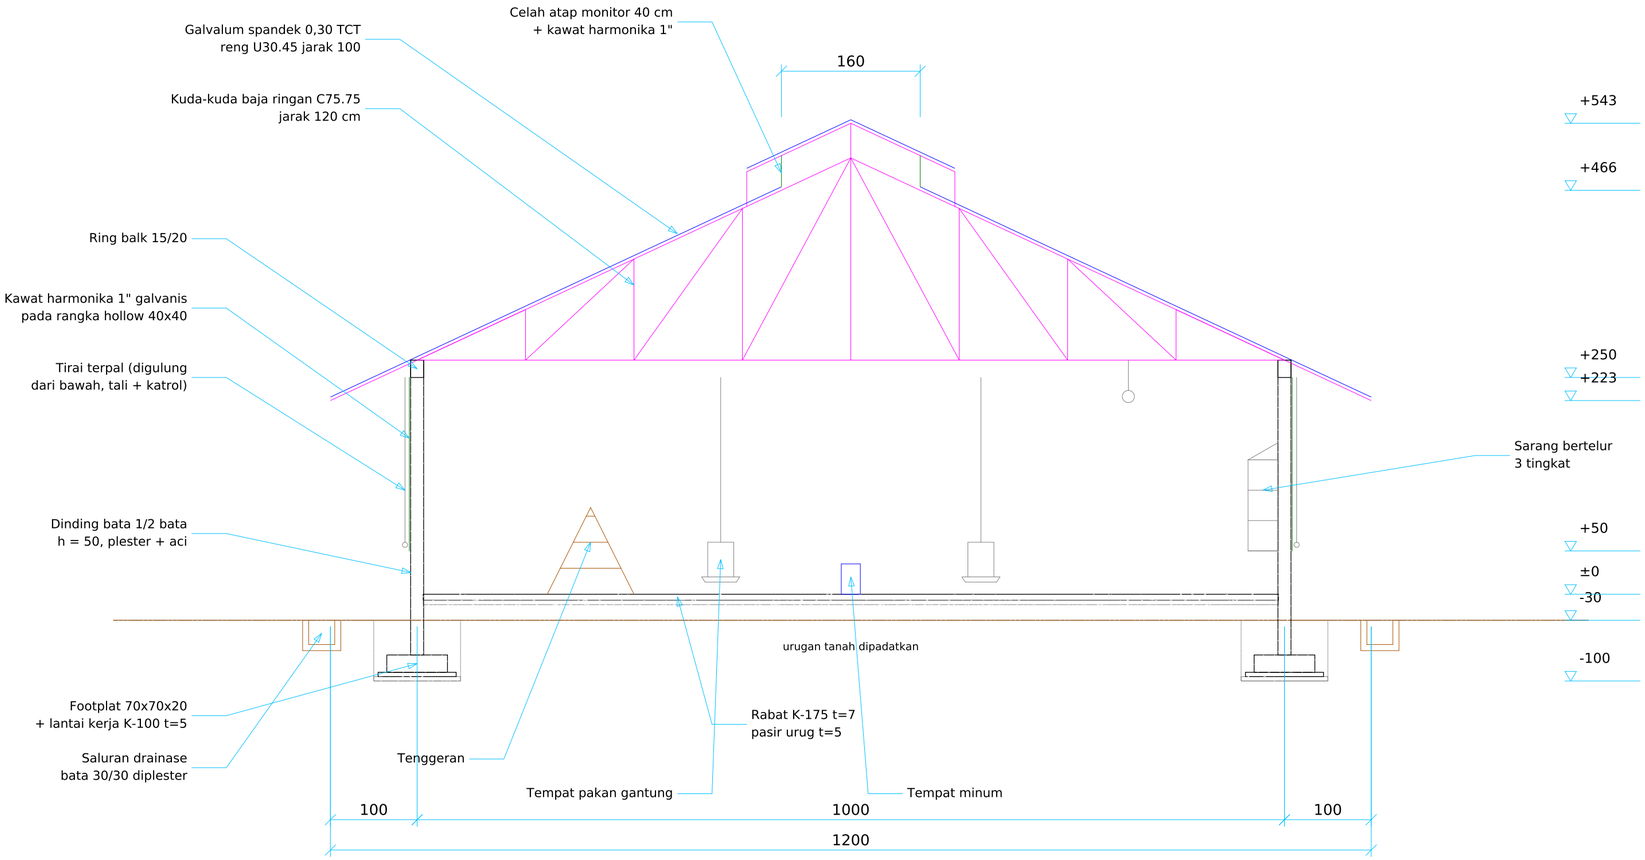

PROYEK	KERTAS A2
PETERNAKAN AYAM KUB PETELUR SEMI UMBARAN 10.000 EKOR ADEVA FARM - KAB. KONAWE SELATAN, SULAWESI TENGGARA	
JUDUL GAMBAR POTONGAN MELINTANG A-A	
CATATAN Satuan cm, elevasi terhadap lantai (±0). Periksa ulang oleh ahli sipil.	SKALA 1 : 50
TANGGAL OKTOBER 2026	STATUS GAMBAR PERENCANAAN
	NO. GAMBAR K-04


DETAIL 1 - PONDASI KOLOM (P1 + K1)

skala 1 : 20 · dipotong pada as kolom

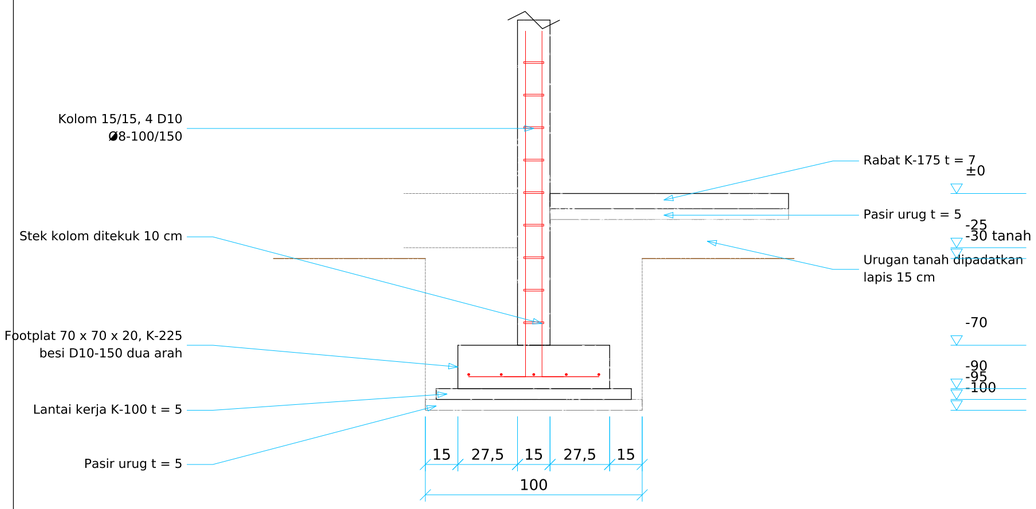

DETAIL 2 - SLOOF, DINDING DAN DRAINASE

skala 1 : 20 · tengah bentang sisi panjang

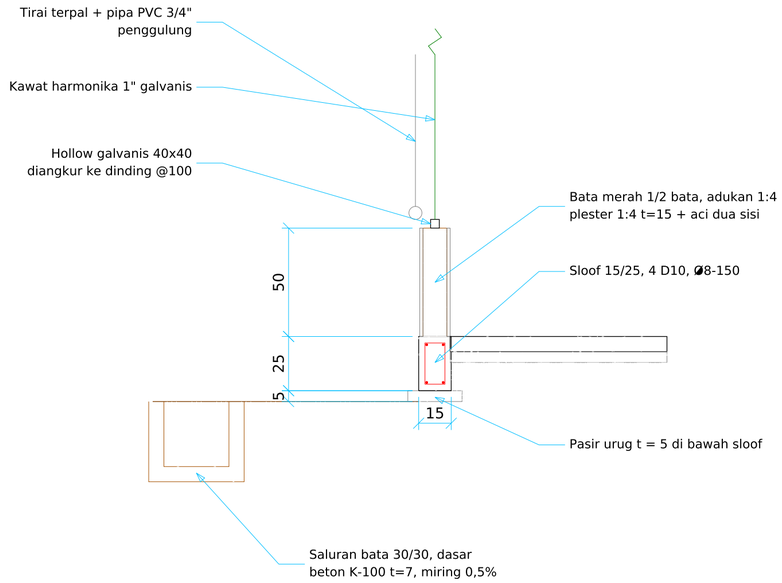

PROYEK
PETERNAKAN AYAM KUB PETELUR SEMI UMBARAN 10.000 EKOR
ADEVA FARM - KAB. KONAWE SELATAN, SULAWESI TENGGARA

KERTAS A2

JUDUL GAMBAR
DETAIL PONDASI FOOTPLAT, SLOOF DAN DINDING

CATATAN
Satuan cm, elevasi terhadap lantai (±0).
Periksa ulang oleh ahli sipil.


SKALA
1 : 20

TANGGAL
OKTOBER 2026

STATUS
GAMBAR PERENCANAAN


NO. GAMBAR
K-05

K1 KOLOM 15/15

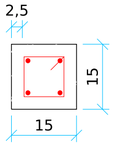


4 D10 · Ø8-150 (Ø8-100 ujung)

S1 SLOOF 15/25

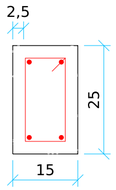


4 D10 · Ø8-150

RB RING BALK 15/20

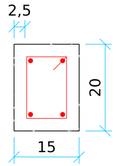


4 D10 · Ø8-150

P1 FOOTPLAT 70 x 70 x 20 (DENAH)

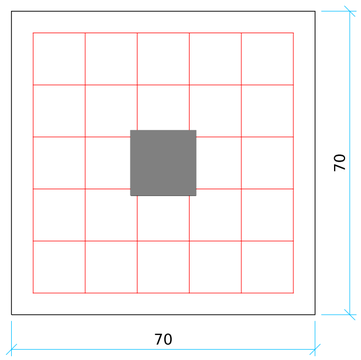


D10-150 dua arah, selimut 5 cm

POTONGAN FOOTPLAT

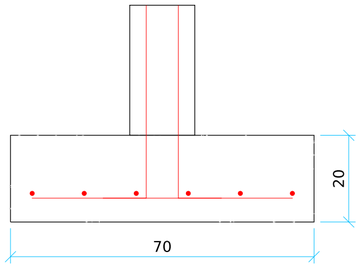

TAMPAK KOLOM K1

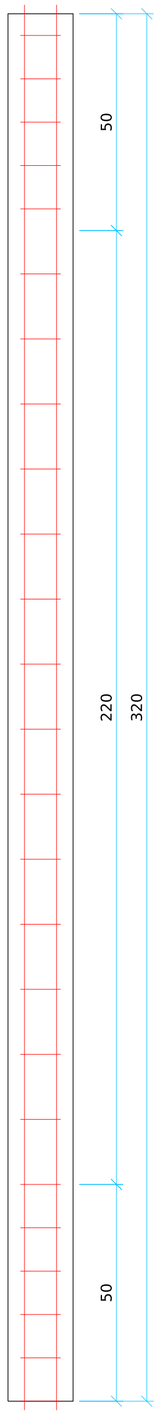

Ø8-100

Ø8-150

Ø8-100

dari atas footplat (-70) s/d bawah ring balk (+250)


CATATAN PEMBESIAN

1. D = besi ulir BJTS 420, Ø = besi polos BJTP 280.
2. Selimut beton: footplat 5 cm, kolom/sloof/ring balk 2,5 cm.
3. Sambungan lewatan 40 D (40 cm untuk D10), tidak pada satu potongan.
4. Kait sengkang 135°, panjang kait 6 Ø (5 cm).
5. Beton K-225 (fc' 19 MPa): 1 semen : 2 pasir : 3 kerikil, air secukupnya.
6. Bekisting dibongkar: kolom 3 hari, sloof 7 hari, ring balk 14 hari.
7. Siram/rawat beton 7 hari agar tidak retak.

PROYEK: PETERNAKAN AYAM KUB PETELUR SEMI UMBARAN 10.000 EKOR ADEVA FARM - KAB. KONAWE SELATAN, SULAWESI TENGGARA			KERTAS A2
JUDUL GAMBAR: DETAIL PENULANGAN KOLOM, SLOOF, RING BALK, FOOTPLAT			
CATATAN Satuan cm, elevasi terhadap lantai (±0). Periksa ulang oleh ahli sipil.		SKALA 1 : 10	
TANGGAL OKTOBER 2026	STATUS GAMBAR PERENCANAAN		NO. GAMBAR K-06

KUDA-KUDA BAJA RINGAN TIPIKAL (KK)

skala 1 : 50 · kemiringan 25°

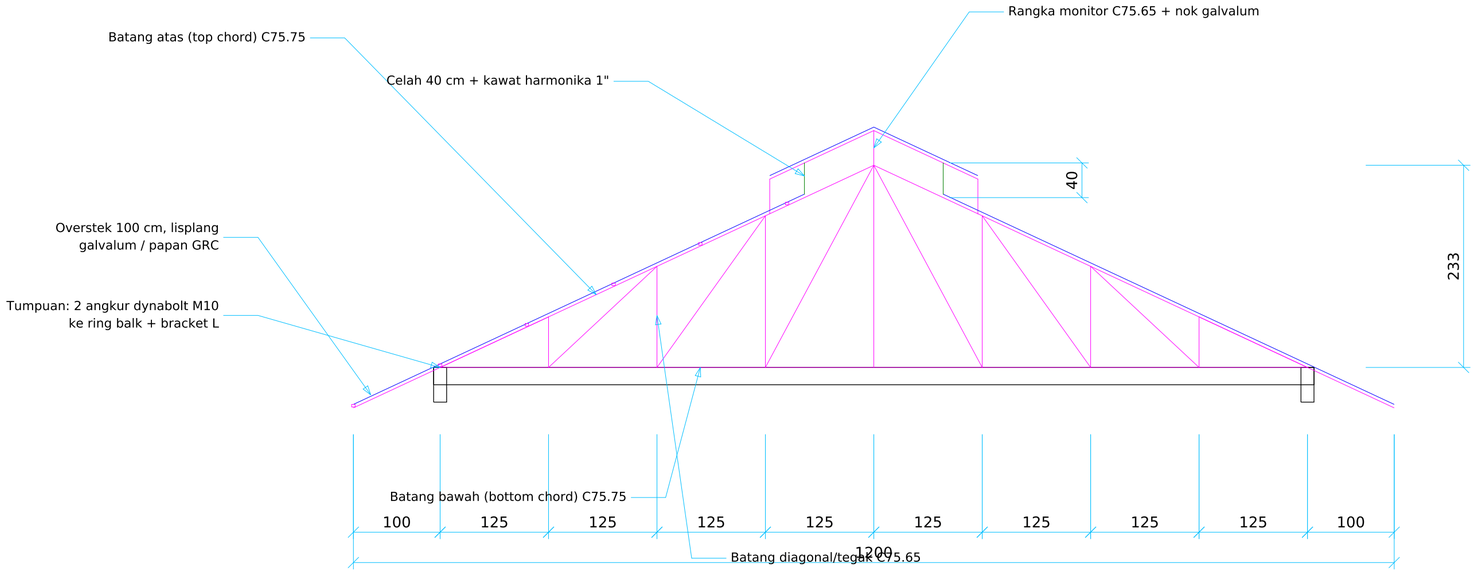


SPESIFIKASI RANGKA ATAP

- Kuda-kuda baja ringan G550 AZ100, profil C75.75 (batang atas/bawah) dan C75.65 (diagonal).
- Jarak kuda-kuda 120 cm: 35 kuda-kuda per kandang, bentang 10 m + overstek 100 cm kiri-kanan.
- Reng U30.45 jarak 100 cm (galvalum spandek boleh bentang reng s.d. 120 cm).
- Ikatan angin (bracing) diagonal di bentang ujung dan setiap 4 bentang.
- Sekrup self drilling 12-14 x 20, minimal 4 sekrup tiap sambungan.
- Penutup: galvalum/zincalume spandek 0,30 TCT AZ100 (lebih tahan amonia daripada seng biasa).

PROYEK PETERNAKAN AYAM KUB PETELUR SEMI UMBARAN 10.000 EKOR ADEVA FARM - KAB. KONAWE SELATAN, SULAWESI TENGGARA			KERTAS A2
JUDUL GAMBAR DETAIL RANGKA ATAP BAJA RINGAN DAN ATAP MONITOR			
CATATAN Satuan cm, elevasi terhadap lantai (±0). Periksa ulang oleh ahli sipil.		SKALA 1 : 50	
TANGGAL OKTOBER 2026	STATUS GAMBAR PERENCANAAN		NO. GAMBAR K-07


DETAIL A - DINDING, KAWAT DAN TIRAI

skala 1 : 20

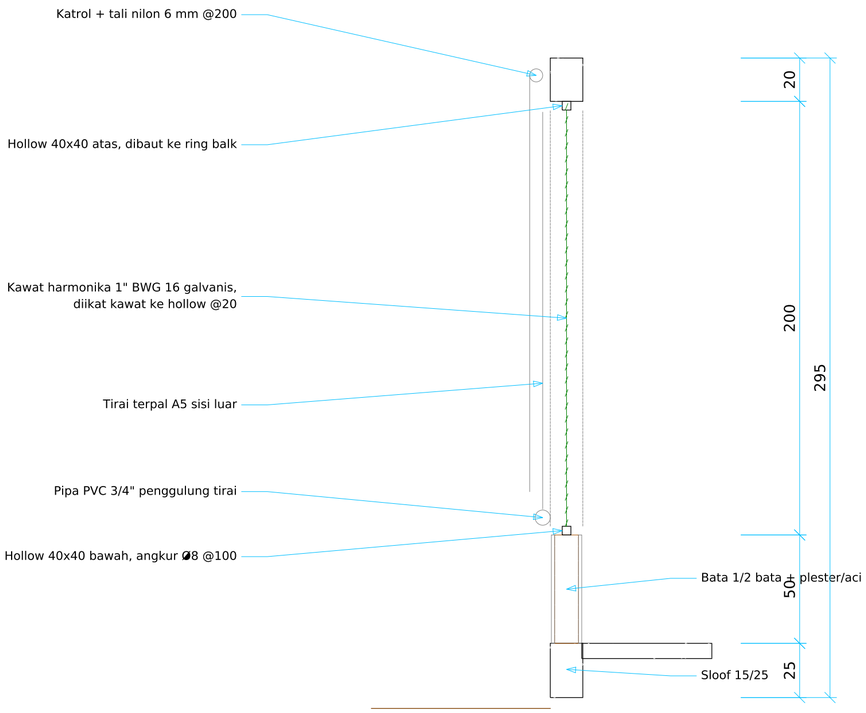


DETAIL B - TAMPAK PINTU UMBARAN

skala 1 : 20 · 8 buah sisi selatan

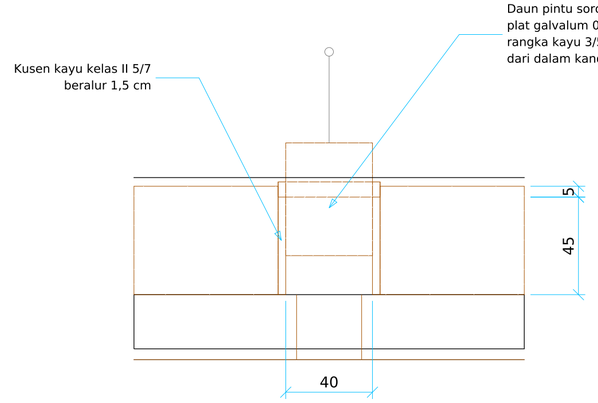

DETAIL C - POTONGAN PINTU UMBARAN


skala 1 : 20

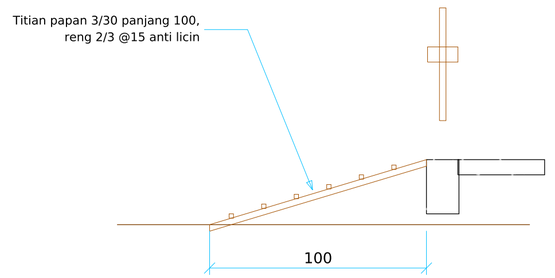

PROYEK PETERNAKAN AYAM KUB PETELUR SEMI UMBARAN 10.000 EKOR ADEVA FARM - KAB. KONAWE SELATAN, SULAWESI TENGGARA			KERTAS A2
JUDUL GAMBAR DETAIL DINDING, KAWAT, TIRAI DAN PINTU UMBARAN			
CATATAN Satuan cm, elevasi terhadap lantai (±0). Periksa ulang oleh ahli sipil.		SKALA 1 : 20	
TANGGAL OKTOBER 2026	STATUS GAMBAR PERENCANAAN		NO. GAMBAR K-08


DETAIL D - PINTU UTAMA

skala 1 : 20 · 2 buah (barat-timur)

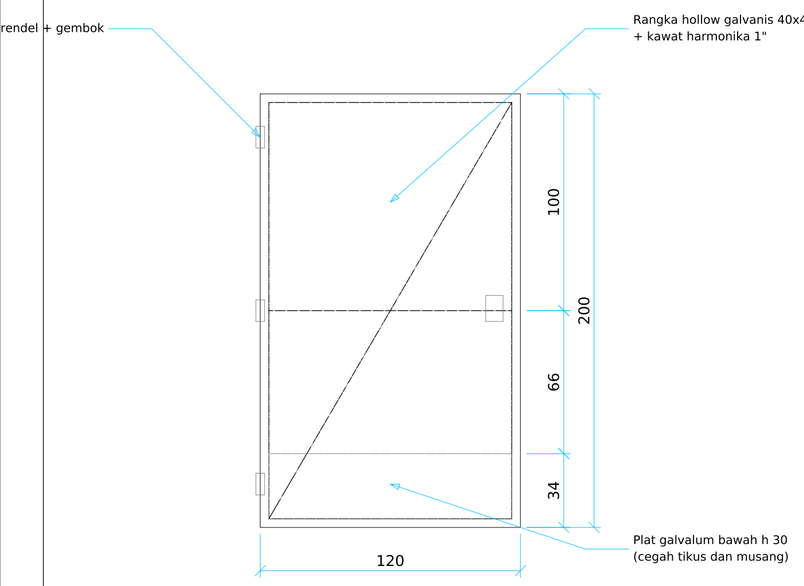


DETAIL E - SARANG BERTELUR

skala 1 : 20 · papan kayu kelas III t=2 / multipleks 9 mm

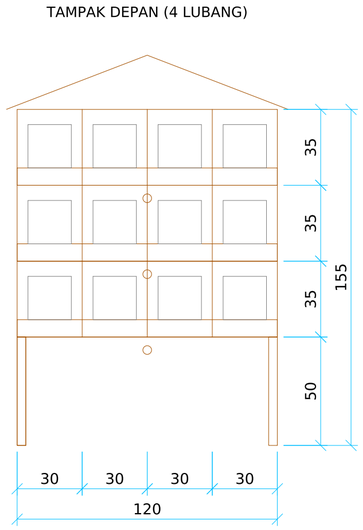

DETAIL F - TENGGERAN

skala 1 : 20 · 2 x 14 m per kandang

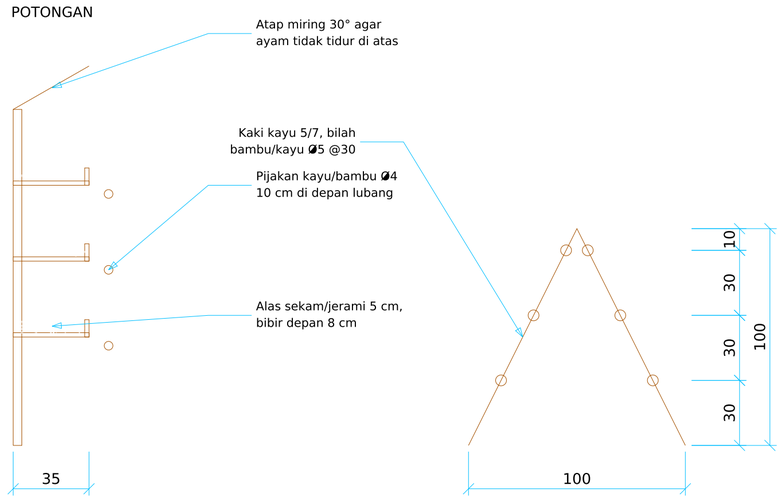

PROYEK	KERTAS A2
PETERNAKAN AYAM KUB PETELUR SEMI UMBARAN 10.000 EKOR ADEVA FARM - KAB. KONAWE SELATAN, SULAWESI TENGGARA	
JUDUL GAMBAR	
DETAIL PINTU UTAMA, SARANG BERTELUR DAN TENGGERAN	
CATATAN Satuan cm, elevasi terhadap lantai (±0). Periksa ulang oleh ahli sipil.	SKALA 1 : 20
TANGGAL OKTOBER 2026	STATUS GAMBAR PERENCANAAN
	NO. GAMBAR K-09