


Rencana Tapak 1 Ha


Lahan 100 m x 100 m. Zona produksi berpagar 70 m x 60 m, dua kandang 10 m x 20 m, sisanya lahan hijauan dan cadangan perluasan. Skala grafis di bawah.

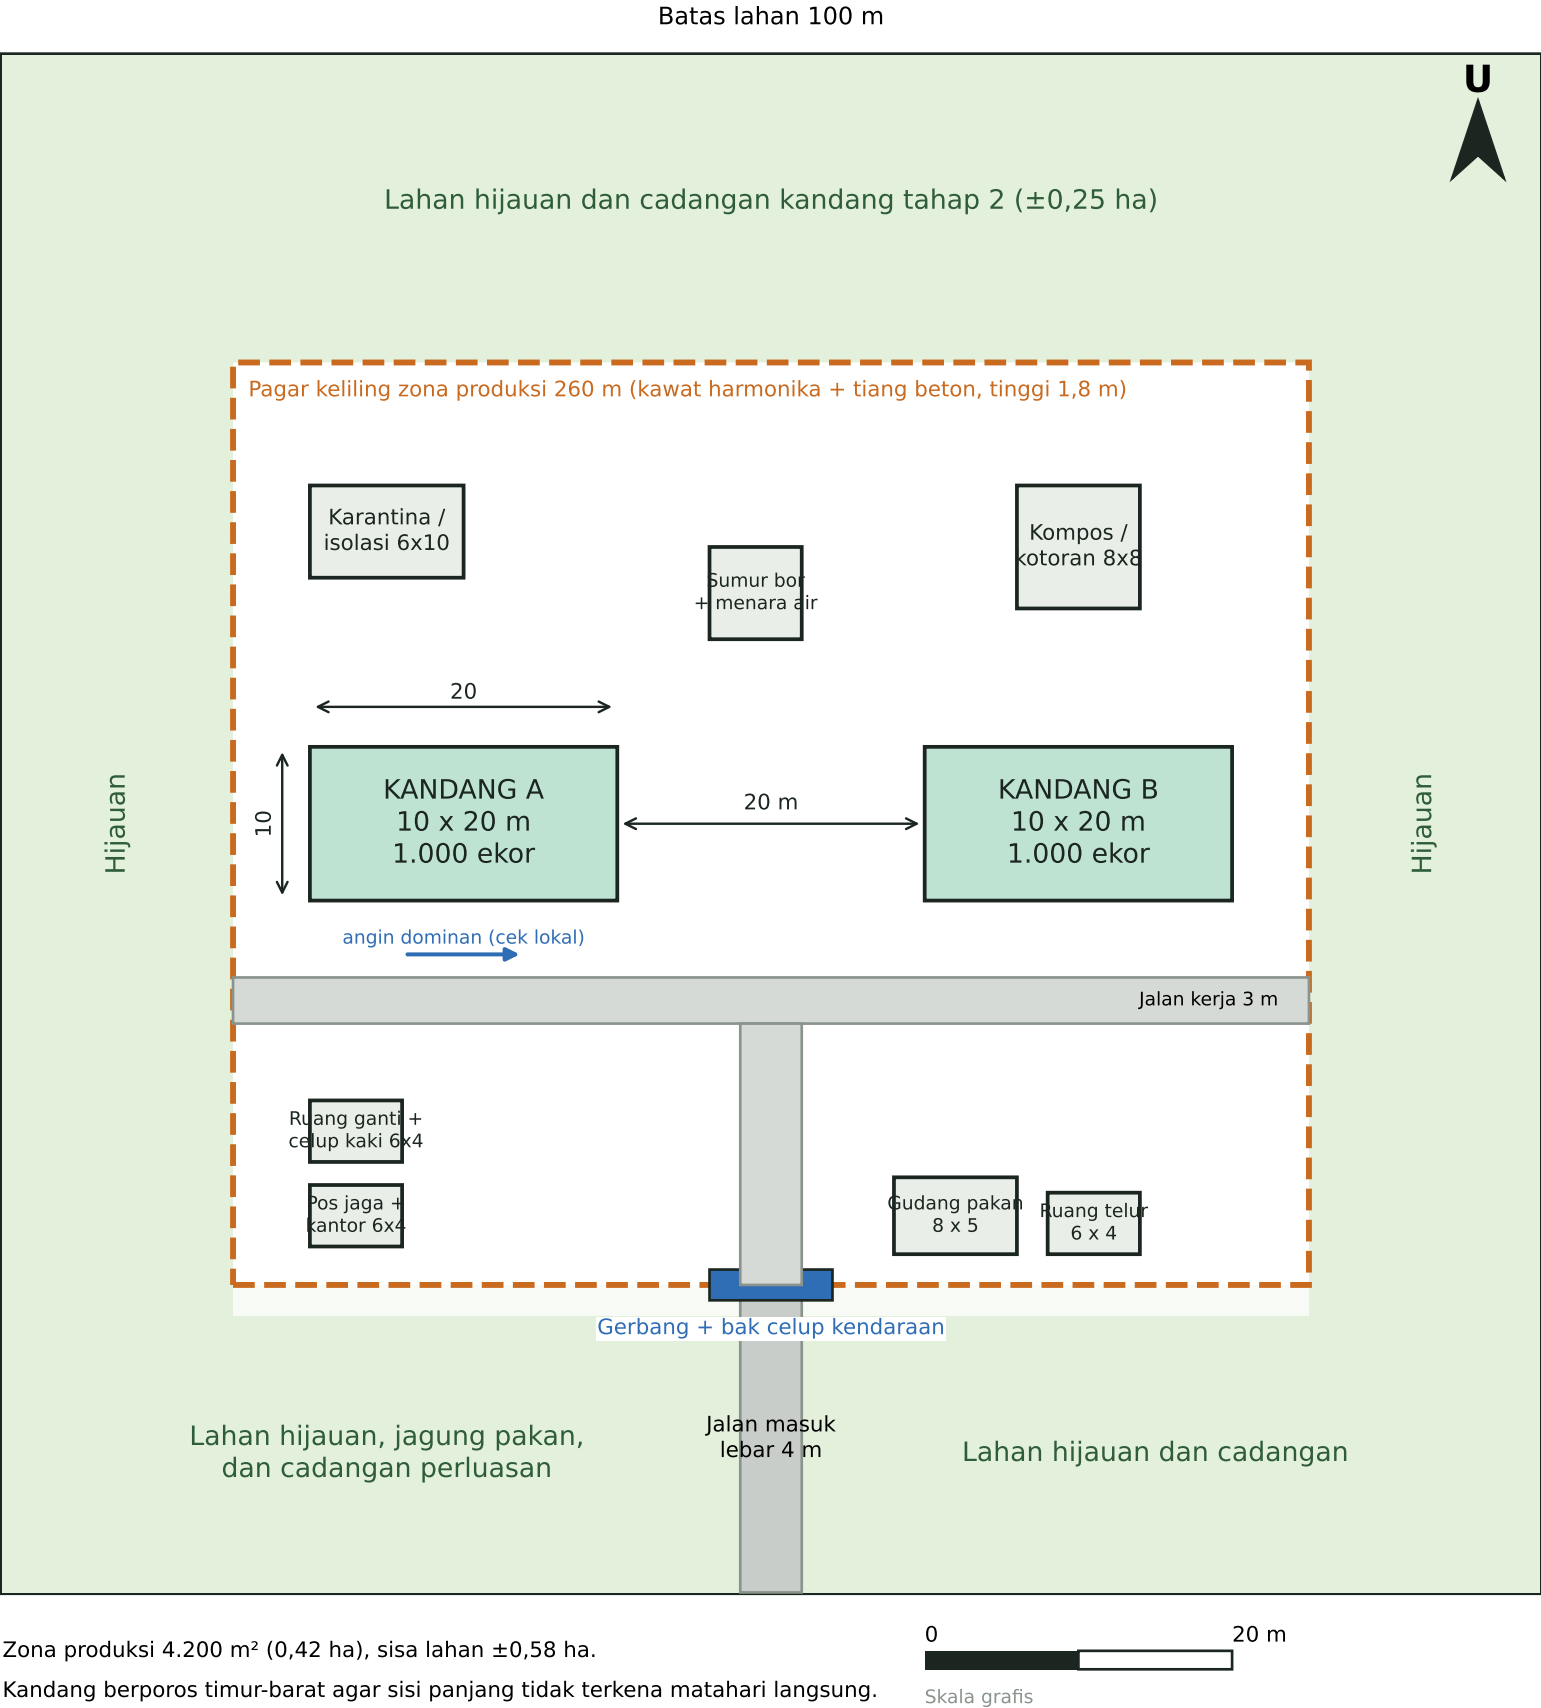

Denah Kandang Tipe Postal (Litter) 10 m x 20 m

Satu unit untuk 1.000 ekor (5 ekor/m²). Sistem litter sekam, dinding bawah bata 0,5 m, kawat harmonika, tirai terpal. Dua unit identik untuk 2.000 ekor.

U

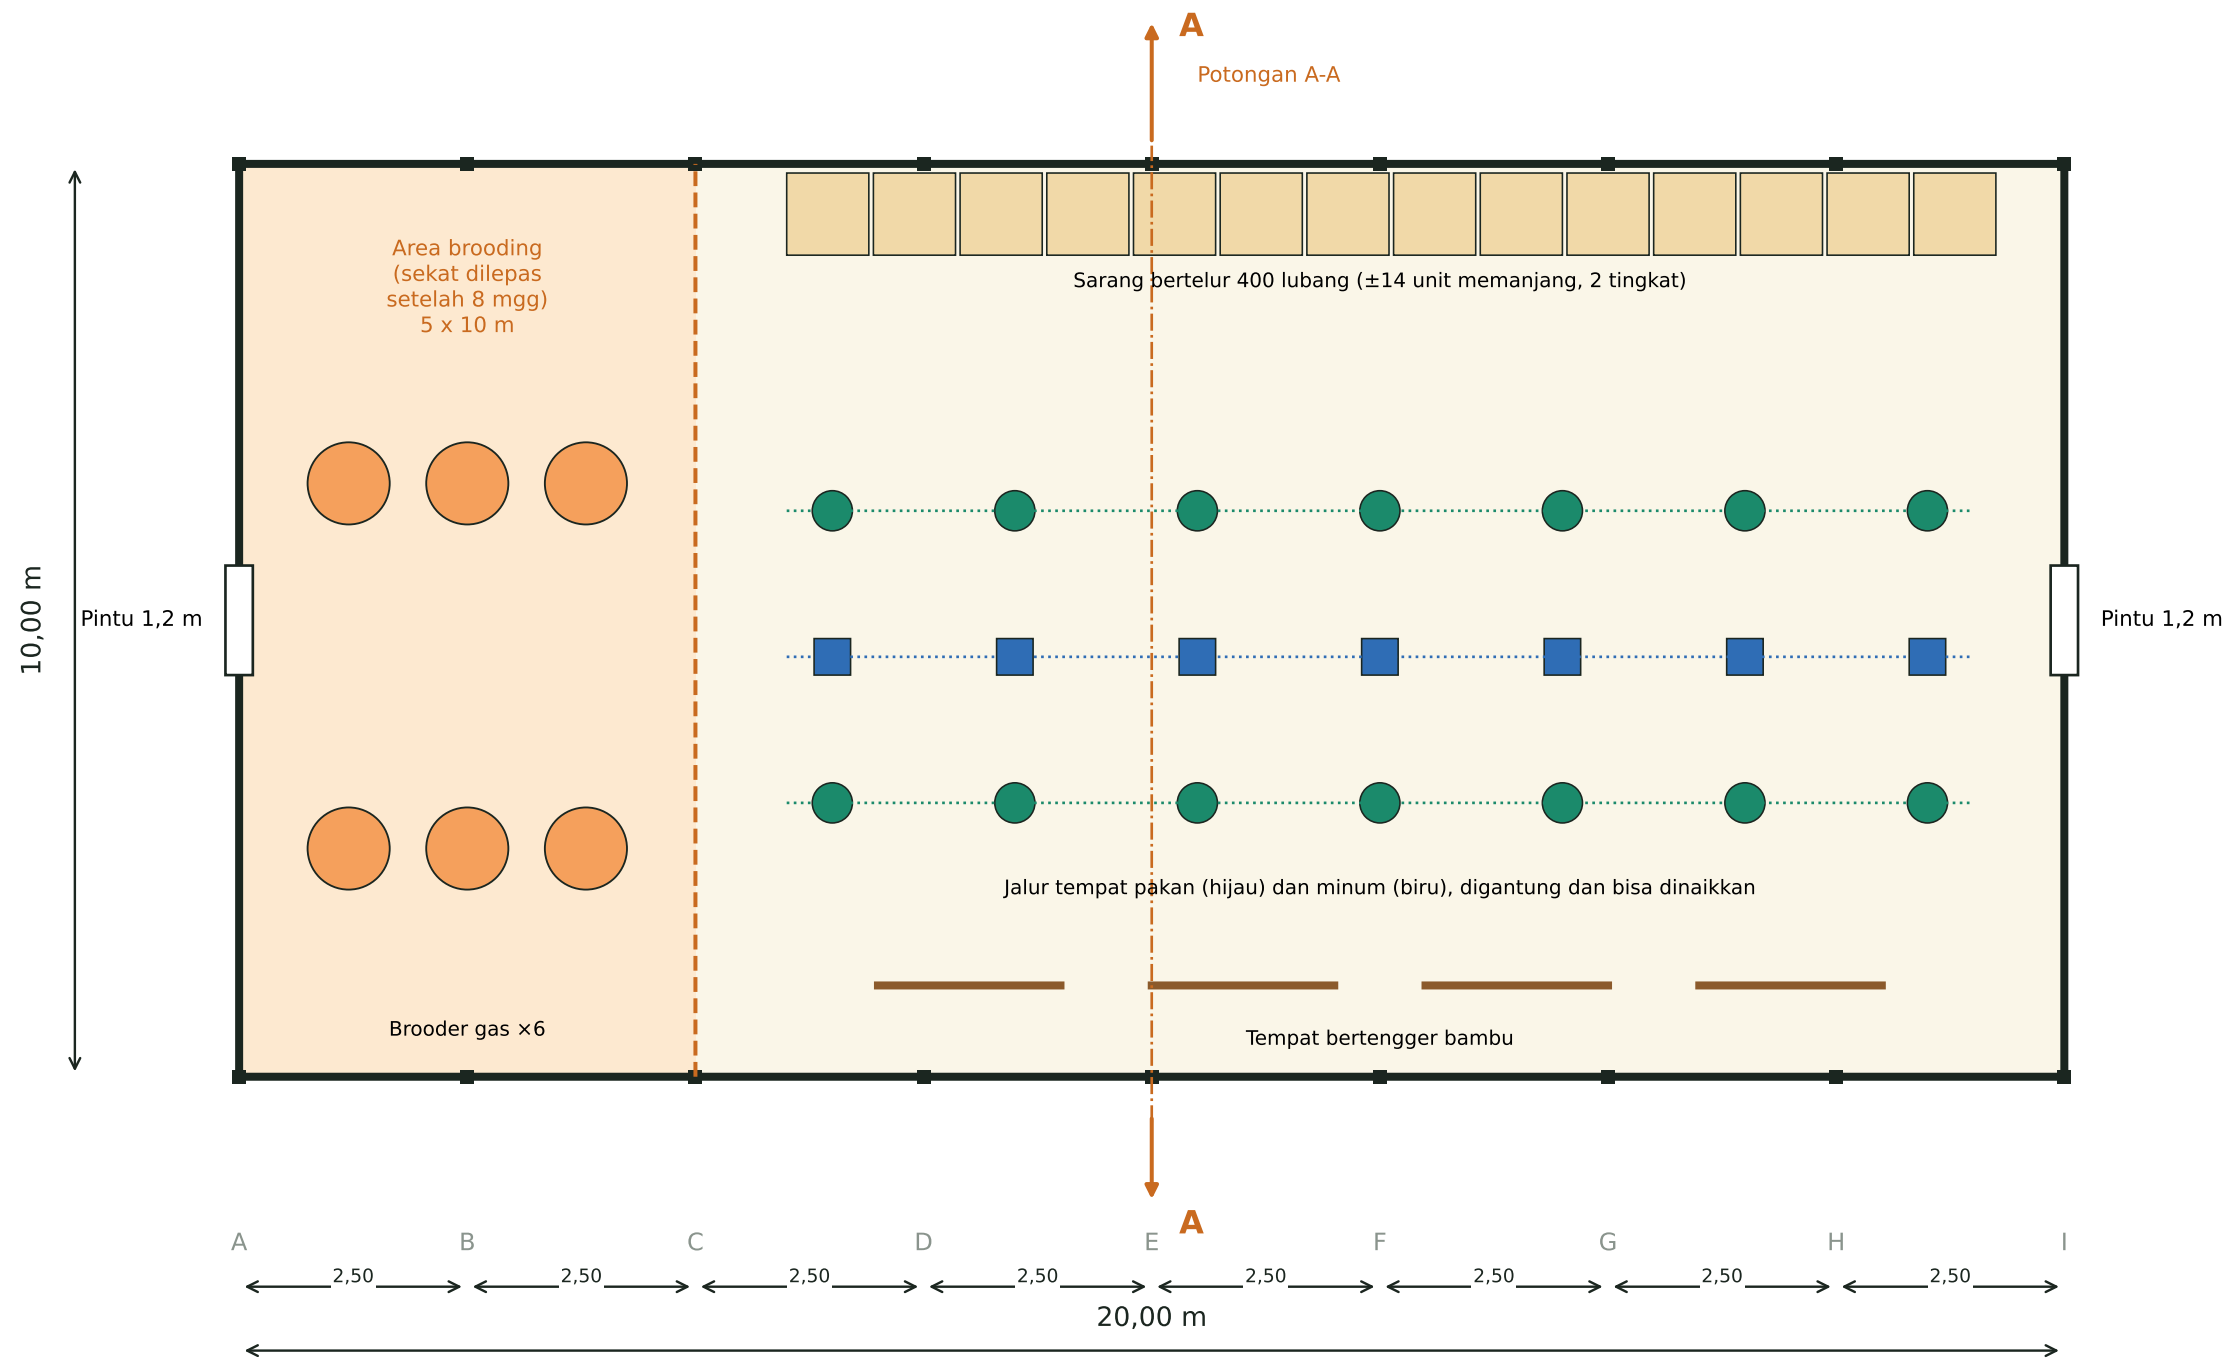


Keterangan: kolom beton 15x15 cm (18 titik) · dinding bata 1/2 bata tinggi 0,5 m · kawat harmonika setinggi 2,5 m di atasnya · tirai terpal 1,6 m dapat digulung · lantai beton t=7 cm miring 1% ke luar · kepadatan 5 ekor/m².

PROYEK	NO. GAMBAR	STATUS
Kandang Ayam KUB 2.000 ekor - Kab. Konawe Selatan, Sulawesi Tenggara	G-02	Desain awal untuk RAB, bukan gambar konstruksi final

Potongan Melintang A-A

Lebar 10 m, rangka atap baja ringan, atap galvalum gelombang, kemiringan 20°, ventilasi nok terbuka. Ukuran dalam meter, tanpa skala cetak.

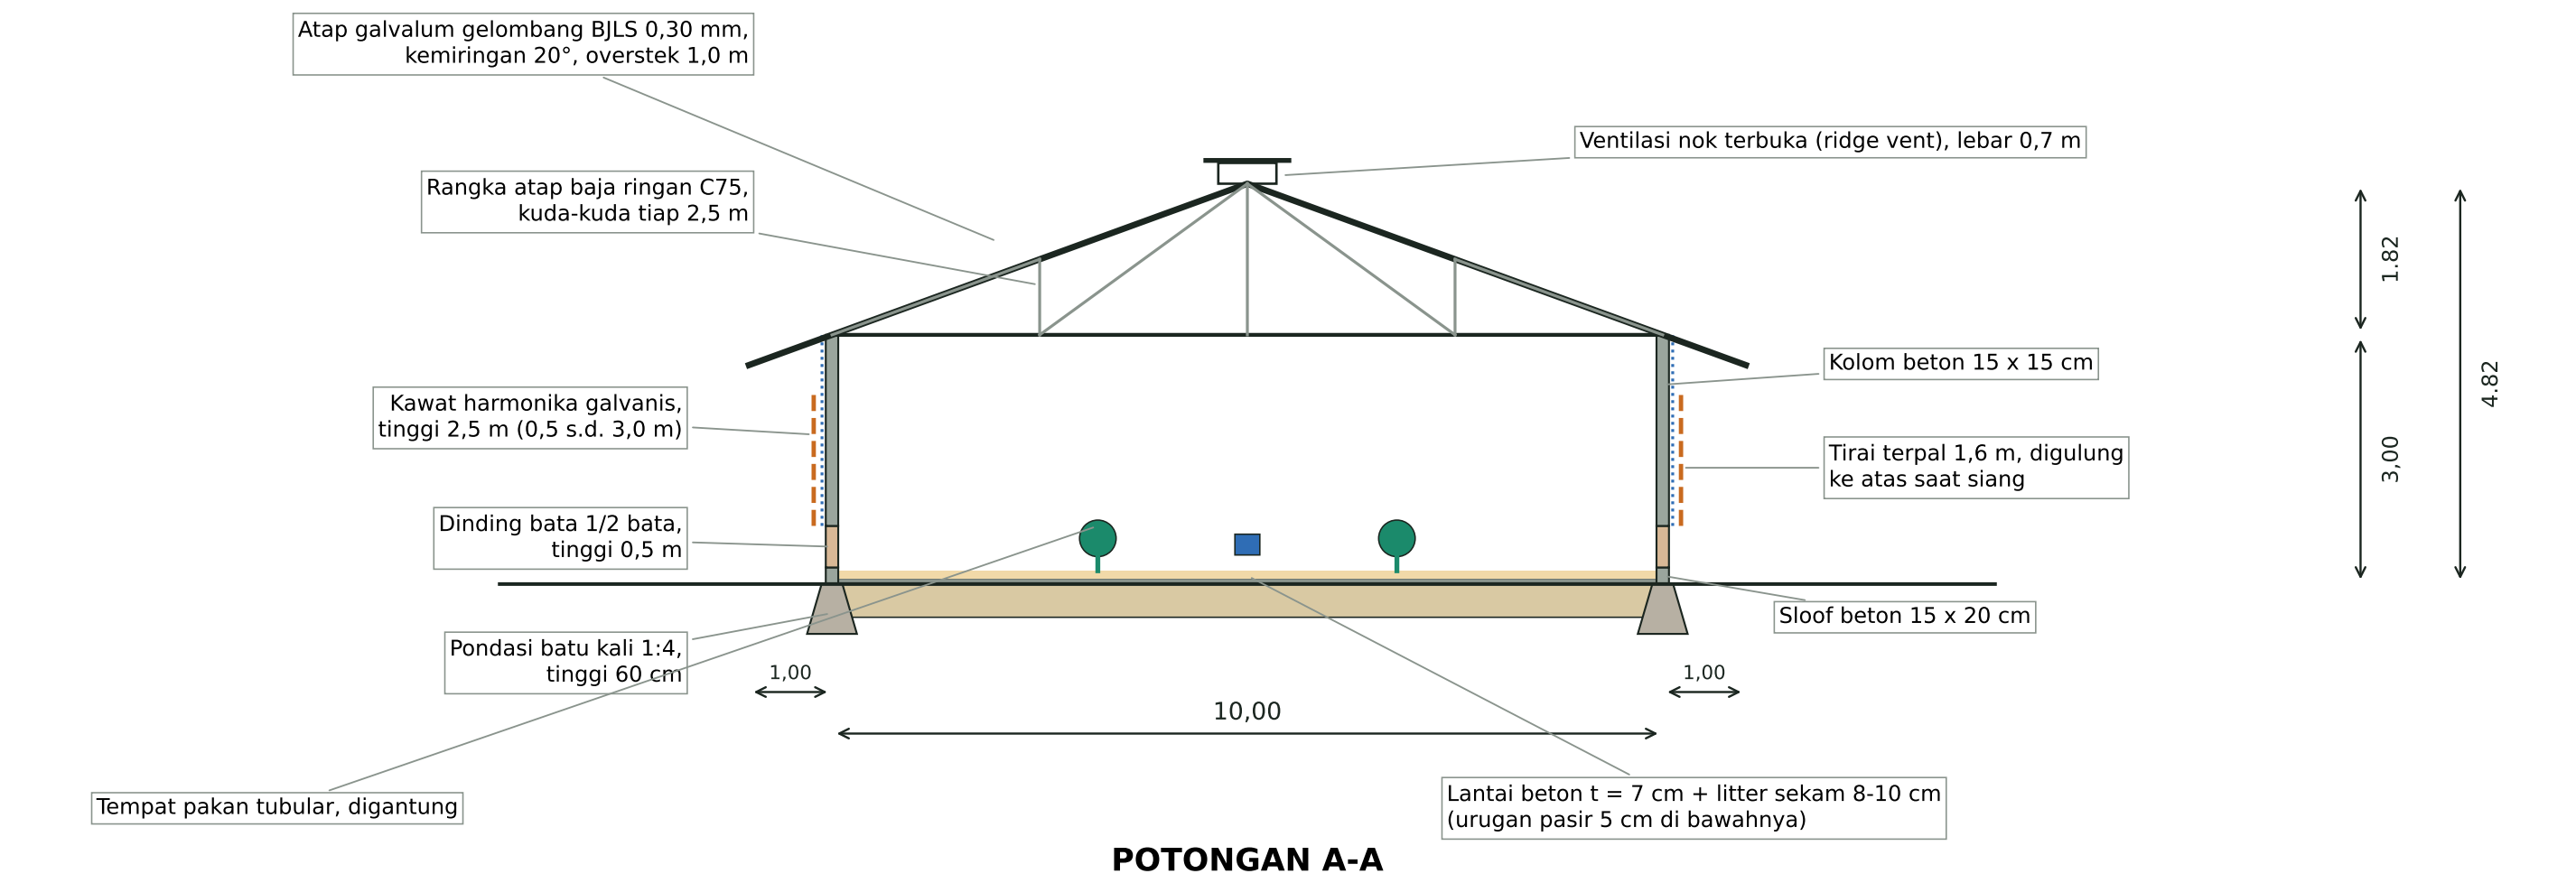


PROYEK	NO. GAMBAR	STATUS
Kandang Ayam KUB 2.000 ekor - Kab. Konawe Selatan, Sulawesi Tenggara	G-03	Desain awal untuk RAB, bukan gambar konstruksi final


Tampak Samping dan Tampak Depan

Tampak samping panjang 20 m dengan 9 as kolom berjarak 2,5 m, dan tampak depan sisi gable 10 m.

Nok dengan ridge vent sepanjang 20 m

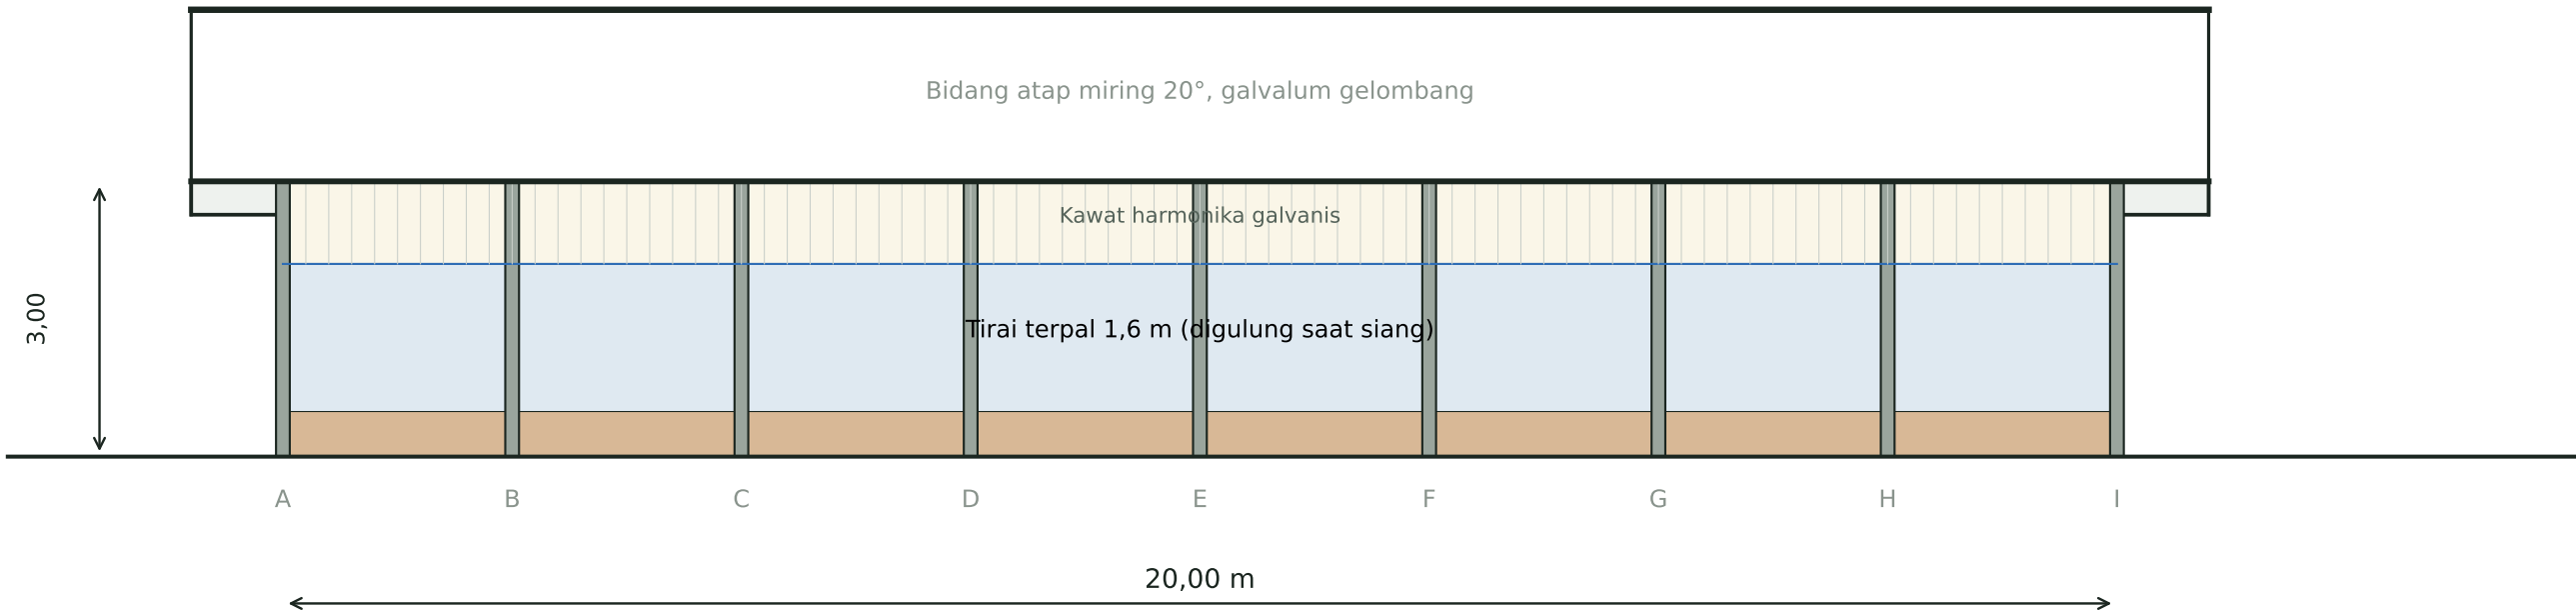

TAMPAK SAMPING

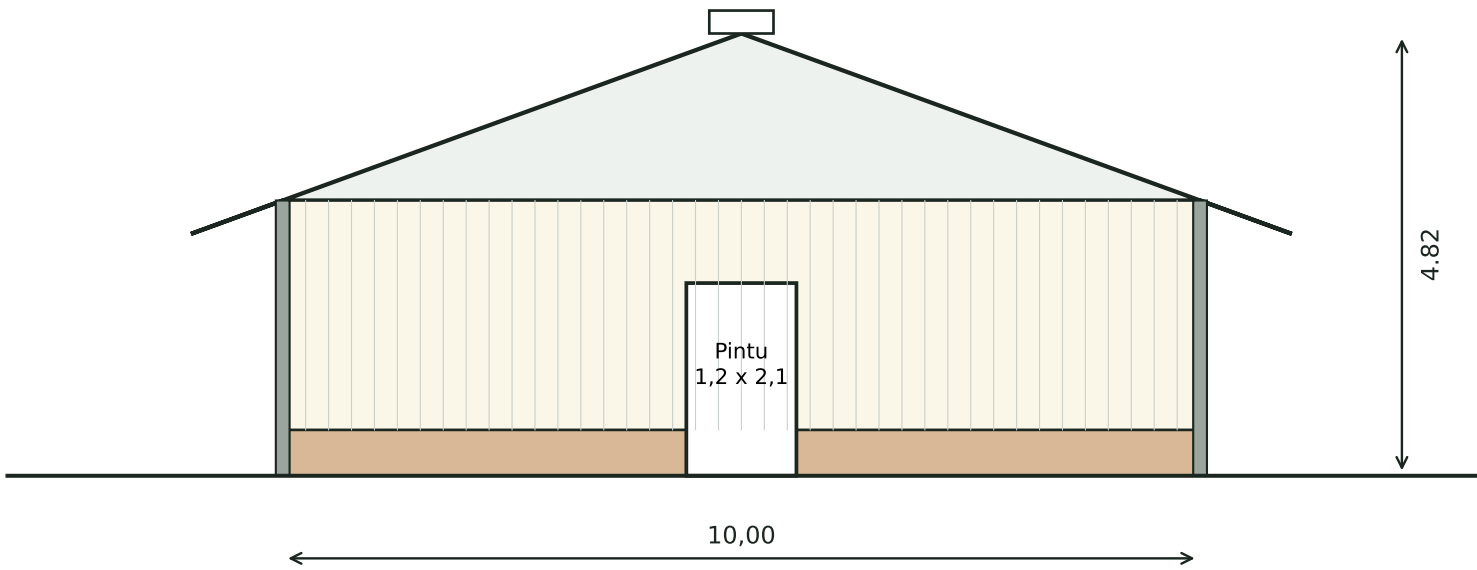


TAMPAK DEPAN (SISI GABLE)

PROYEK	NO. GAMBAR	STATUS
Kandang Ayam KUB 2.000 ekor - Kab. Konawe Selatan, Sulawesi Tenggara	G-04	Desain awal untuk RAB, bukan gambar konstruksi final

Detail Pondasi, Sloof, Dinding, dan Lantai

Pondasi batu kali menerus di bawah dinding bata dan kolom. Ukuran dalam cm kecuali disebut lain.

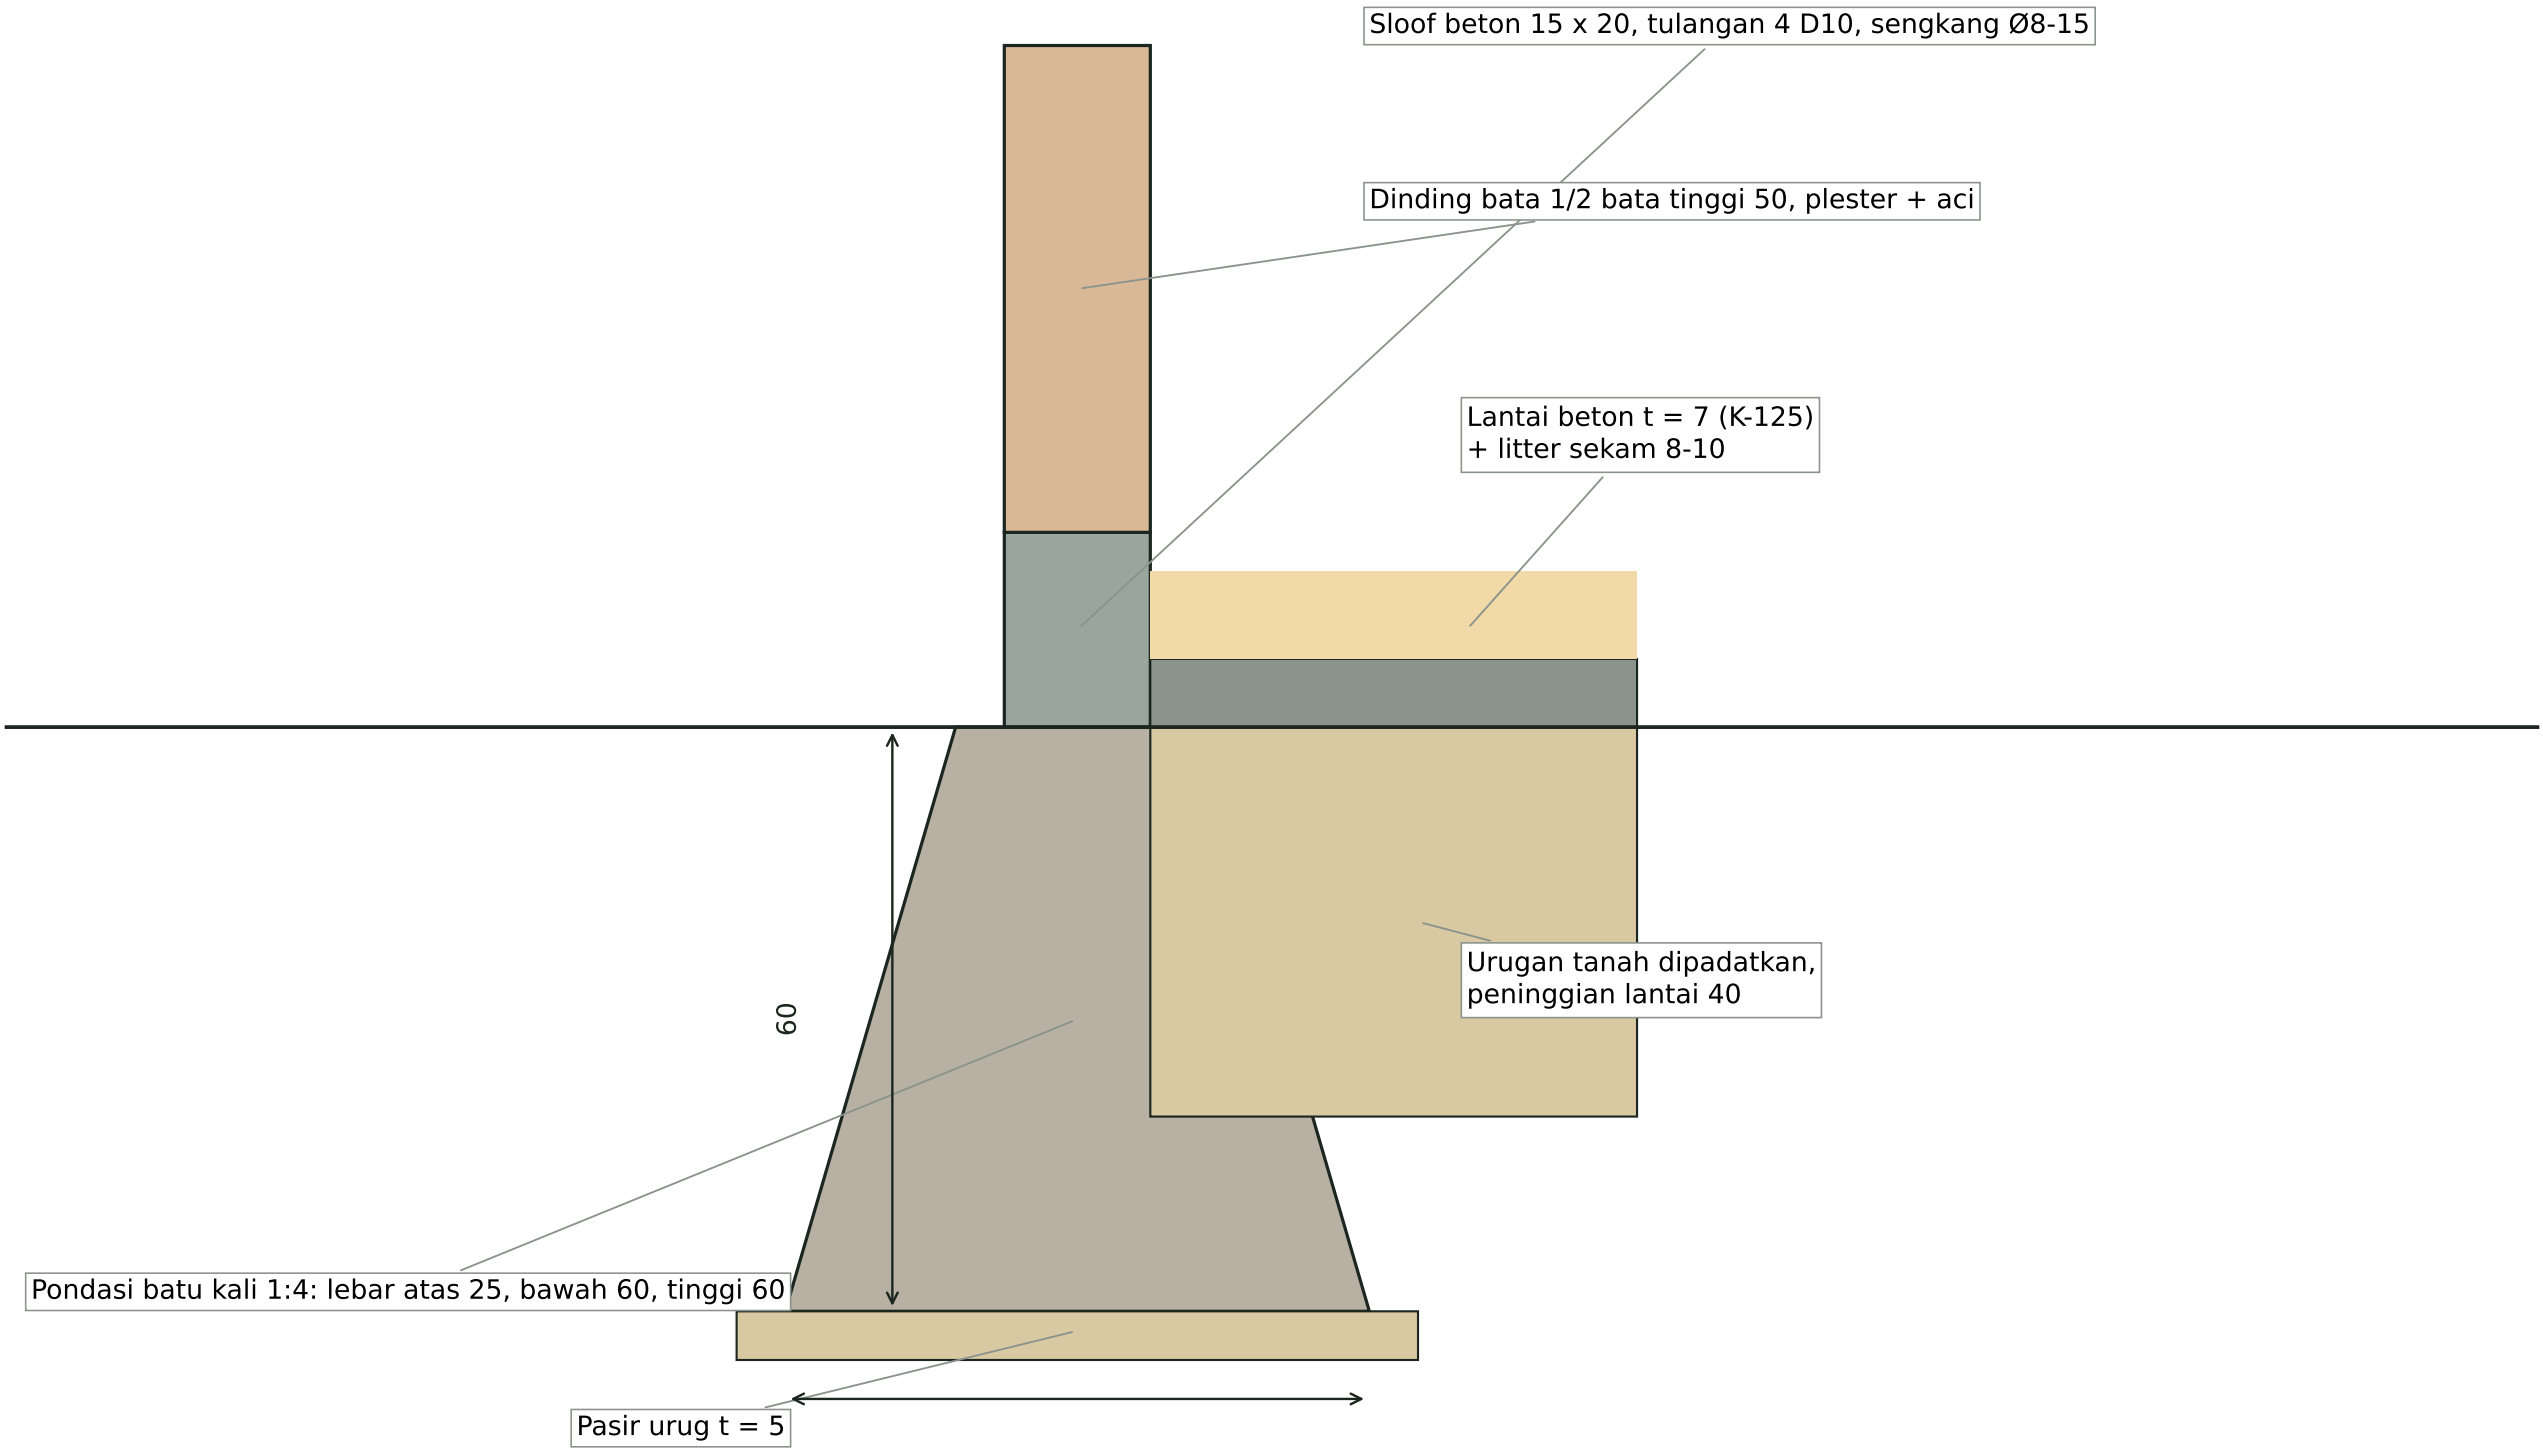

Kolom 15 x 15: 4 D10, sengkang Ø8-15, jarak 250, berdiri di atas sloof dengan stek tulangan 40.
Ring balk 12 x 15 di atas kolom sebagai dudukan rangka baja ringan. Beton K-175 untuk sloof, kolom, ring balk.

PROYEK	NO. GAMBAR	STATUS
Kandang Ayam KUB 2.000 ekor - Kab. Konawe Selatan, Sulawesi Tenggara	G-05	Desain awal untuk RAB, bukan gambar konstruksi final